
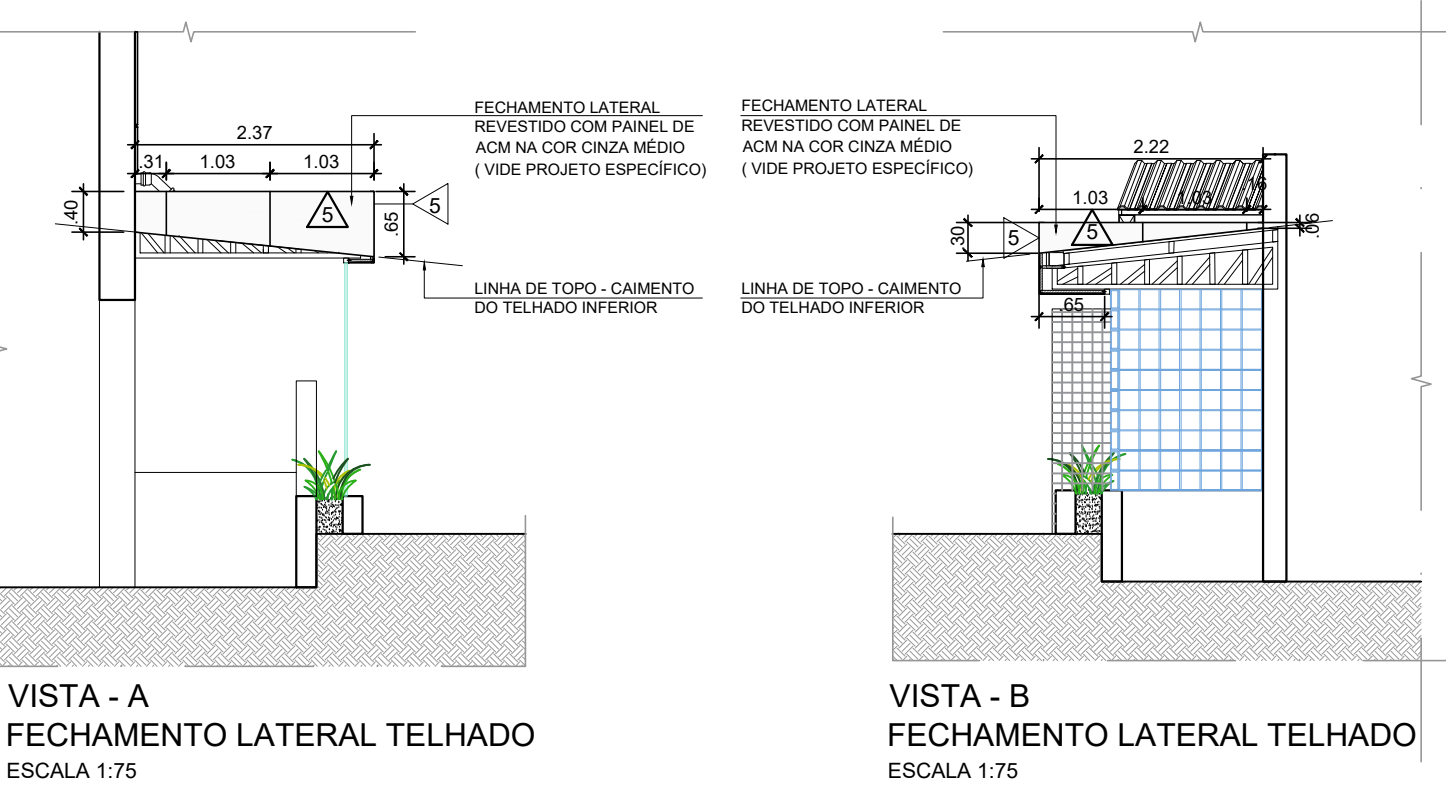


IMPORTANTE:
 ** NOTA TÉCNICA - PROJETO DE FACHADA, INSTALAÇÃO DE ACM **
 A INSTALAÇÃO DE ACM NA FACHADA DO EDIFÍCIO REQUER A ELABORAÇÃO DE UM PROJETO ESPECÍFICO, QUE CONTEMPLE TODOS OS DETALHES TÉCNICOS E ESTRUTURAIS NECESSÁRIOS PARA GARANTIR A EXECUÇÃO SEGURA, EFICIENTE E ESTETICAMENTE SATISFATÓRIA DO MATERIAL. O PROJETO DEVERÁ ESPECIFICAR AS CONDIÇÕES DE FIXAÇÃO, INCLUINDO SUPORTES, ANCORAGENS E DETALHES DE ACABAMENTO, RESPEITANDO AS NORMAS DE SEGURANÇA E DESEMPENHO.


LEGENDA DE ACABAMENTOS

△ PAREDES EXTERNAS	
1	REVESTIMENTO FULGET NA COR CINZA MÉDIO COM JUNTAS DE DILATAÇÃO HORIZONTAIS DE 1" (2,54CM)
2	REVESTIMENTO FULGET NA COR CINZA CLARO COM JUNTAS DE DILATAÇÃO HORIZONTAIS DE 1" (2,54CM)
3	REVESTIMENTO FULGET NA COR VERMELHO
4	ESTRUTURA METÁLICA - FIXADA NA FACHADA REVESTIDA COM PAINEL DE ACM NA COR VERMELHO PADRÃO SÃO CAMILO (VIDE PROJETO ESPECÍFICO)
5	ESTRUTURA METÁLICA - FIXADA NA FACHADA REVESTIDA COM PAINEL DE ACM NA CINZA MÉDIO (VIDE PROJETO ESPECÍFICO)
6	TUJOLO DE VIDRO 190X190X80MM ONDULADO INCOLOR, E BARRAS DE AÇO DE 5MM DE DIÂMETRO PARA TRAVAMENTO VERTICAL E HORIZONTAL.A INSTALAR
7	TUJOLO DE VIDRO 200X200X80MM COM VENTILAÇÃO, INCOLOR E BARRAS DE AÇO DE 5MM DE DIÂMETRO PARA TRAVAMENTO VERTICAL E HORIZONTAL.A INSTALAR
8	CERÂMICA 100X100 EXISTENTE.A MANTER
9	MARQUISE EXISTENTE REVESTIDA EM CHAPA METÁLICA, PREVER NOVA PINTURA NA COR VERMELHO PADRÃO SÃO CAMILO
10	RECOMPOSIÇÃO EM MASSA COM PINTURA NA COR CINZA MÉDIO

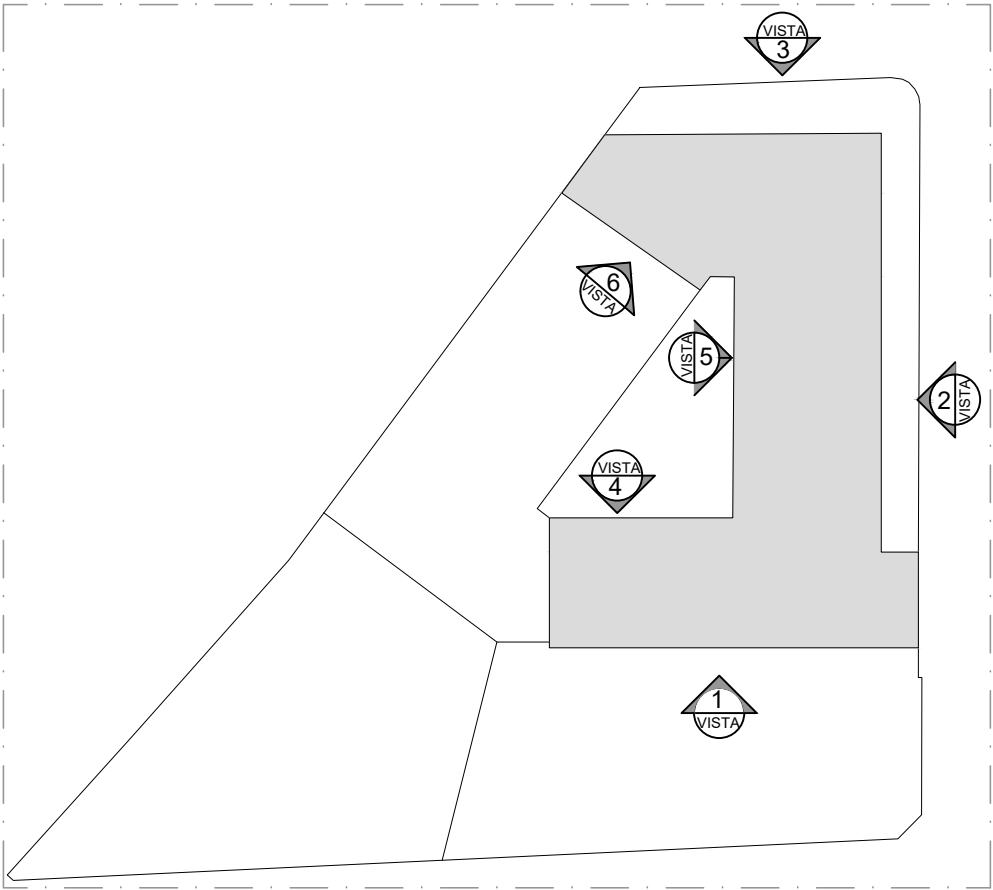


VISTA - A
 FECHAMENTO LATERAL TELHADO
 ESCALA 1:75


VISTA - B
 FECHAMENTO LATERAL TELHADO
 ESCALA 1:75

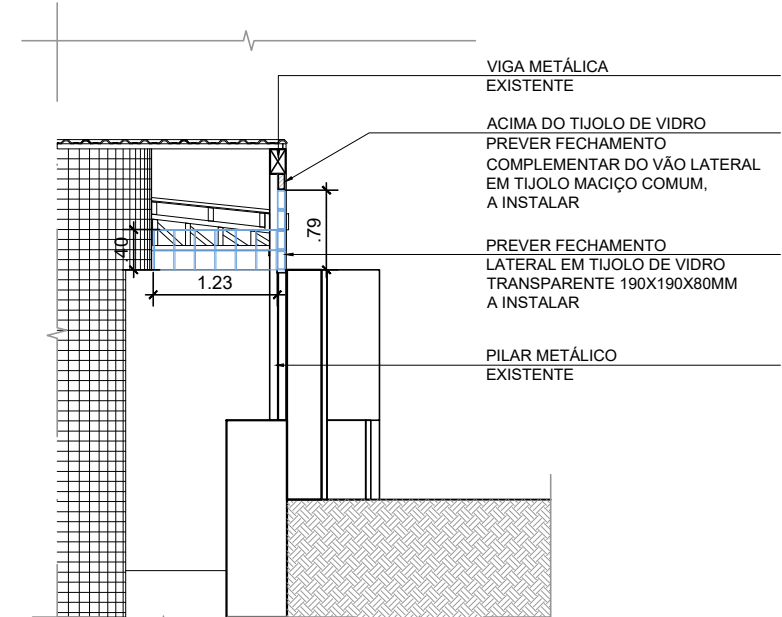


CORTE A-A
 ESCALA 1:75

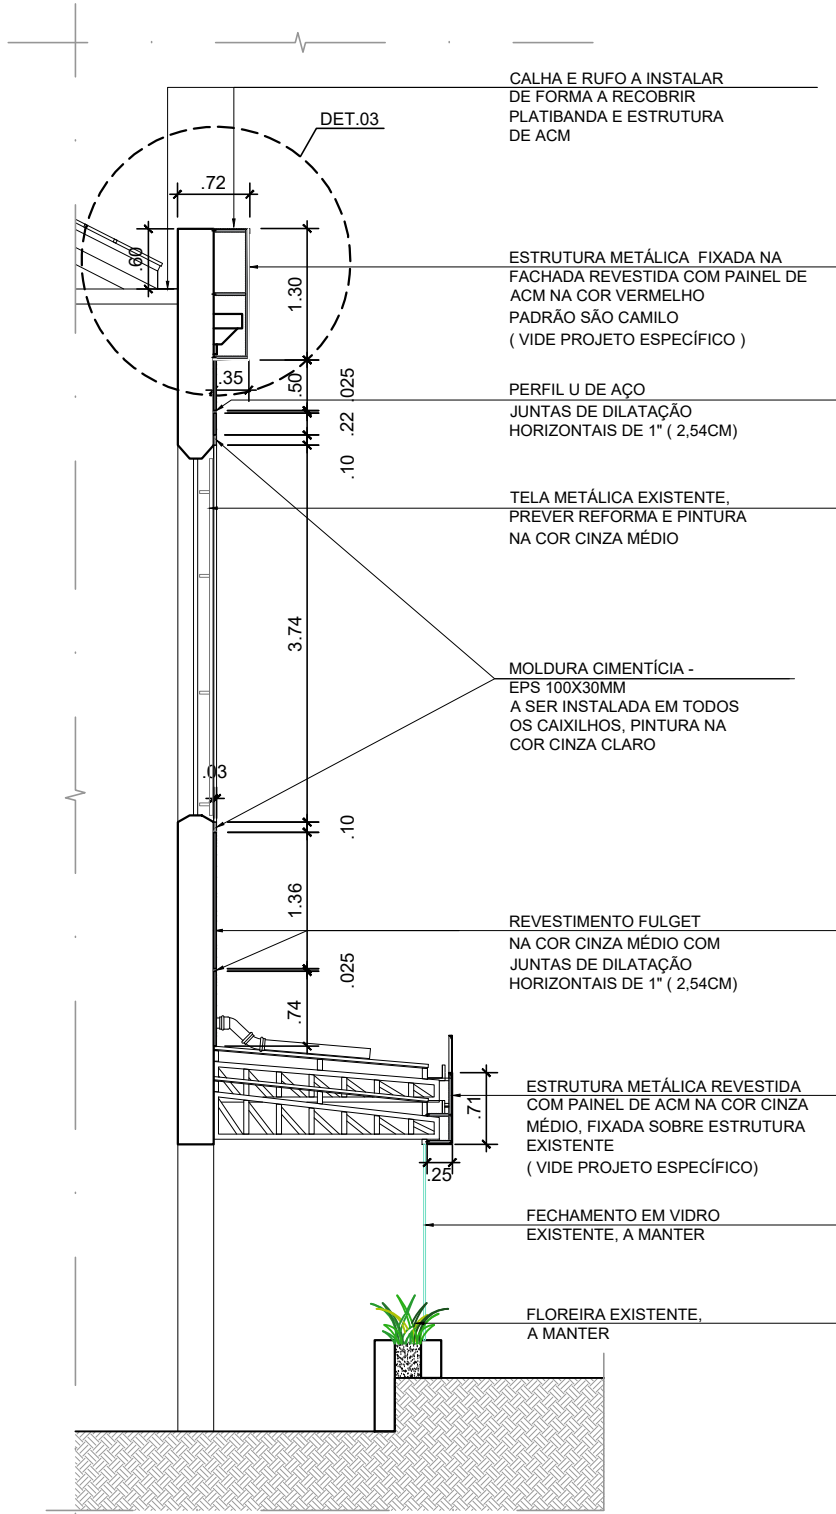


CORTE B-B
 ESCALA 1:75

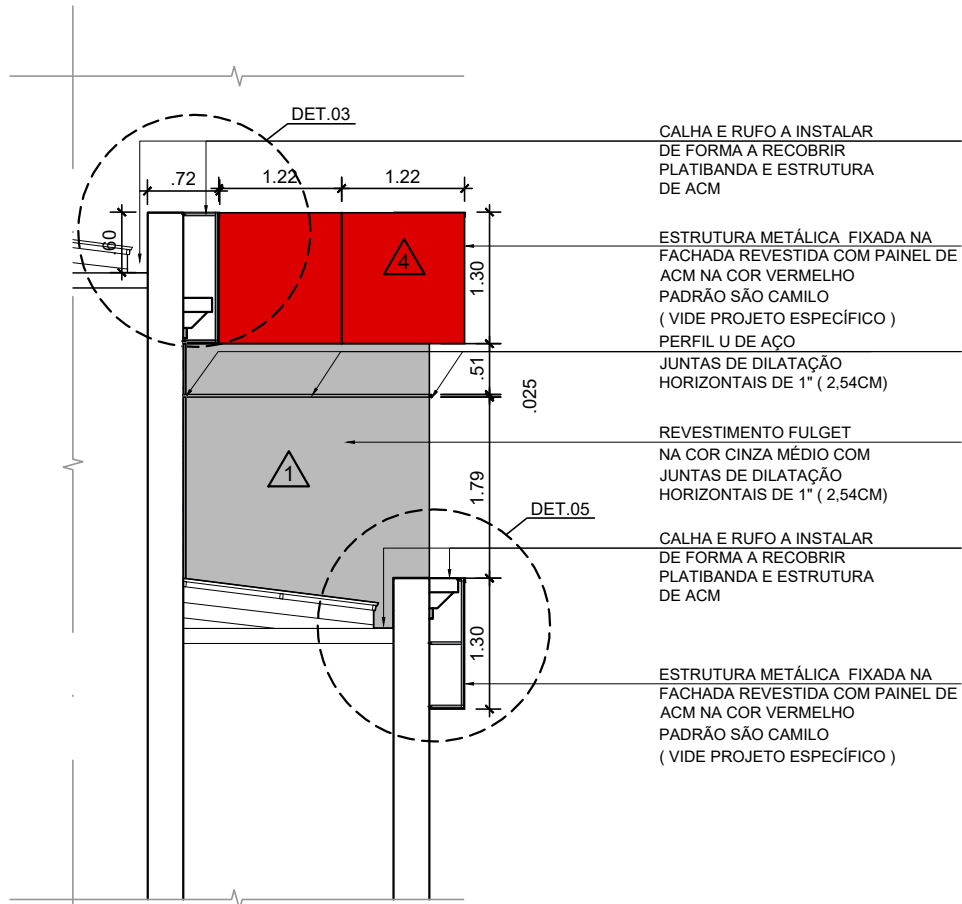




CORTE D-D
 ESCALA 1:75

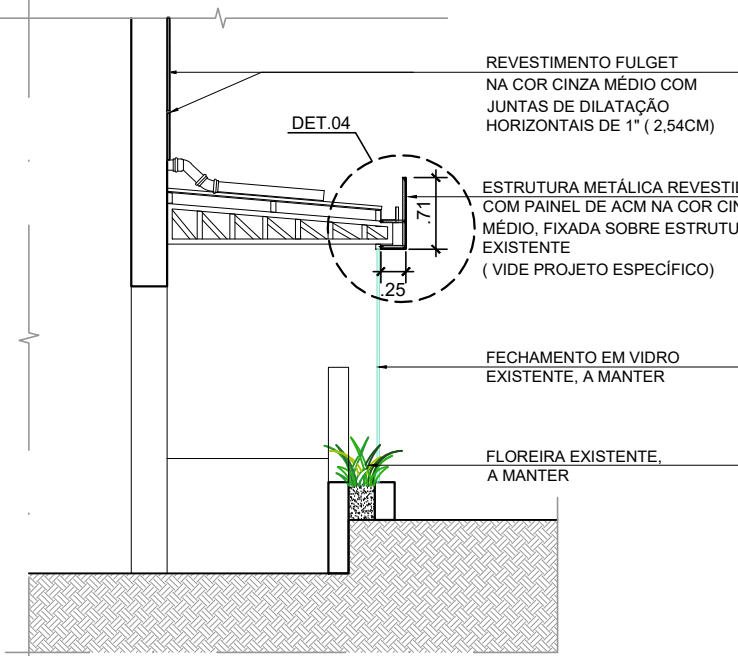

CORTE C-C
 ESCALA 1:75


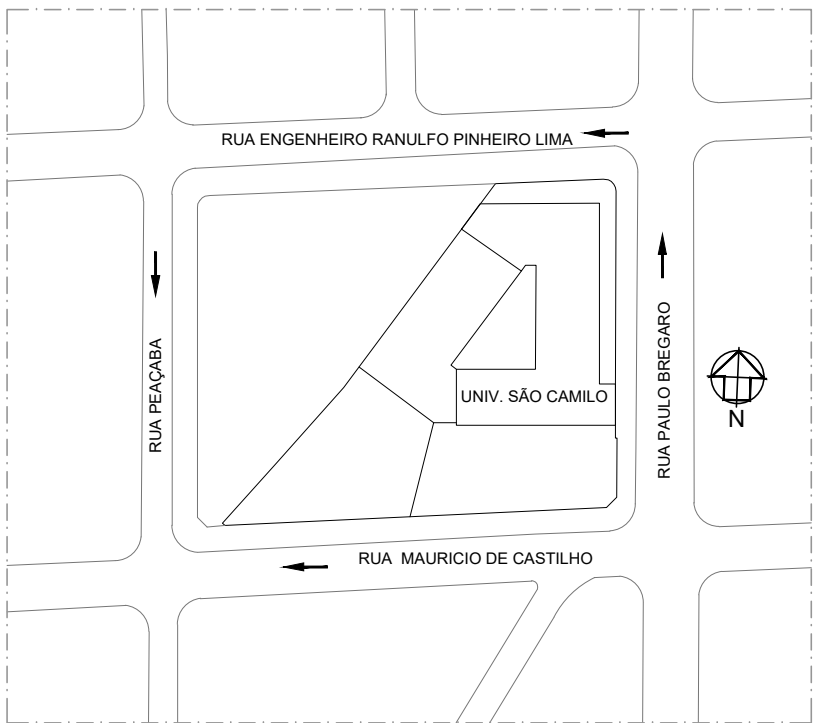




02	27.07.26	MUDANÇA NOS FORMATOS CONF. SOLICITAÇÃO DA ENGª DO SÃO CAMILO
01	07.11.24	REVISÃO GERAL CONFORME APONTAMENTOS
REVISÃO:	DATA:	DESCRIÇÃO:
PROJETISTA:  MP ARQUITETURA ARQUITETURA & CONSULTORIA		CLIENTE:  CENTRO UNIVERSITÁRIO SÃO CAMILO
PROJETO: UNIVERSIDADE SÃO CAMILO - UNIDADE IPIRANGA PROMOVE		REVISÃO:
ASSUNTO: REFORMA DE FACHADA / EXECUTIVO		02
PISO/ FACHADA 01- CORTES	ESC.: INDICADA	FOLHA: 02 / 12
RESPONSÁVEL TÉCNICO: MAURO PEREIRA FILHO	DATA: 04.05.23	
CAU DO RESPONSÁVEL TÉCNICO A - 7458-6	RRT	

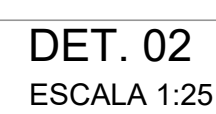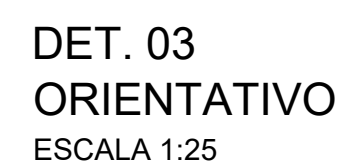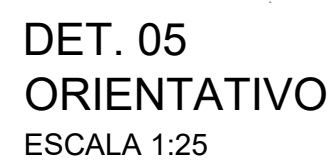


A INSTALAÇÃO DE ACM NA FACHADA DO EDIFÍCIO REQUER A ELABORAÇÃO DE UM PROJETO ESPECÍFICO, QUE CONTEMPLE TODOS OS DETALHES TÉCNICOS E ESTRUTURAIS NECESSÁRIOS PARA GARANTIR A EXECUÇÃO SEGURA, EFICIENTE E ESTETICAMENTE SATISFATÓRIA DO MATERIAL. O PROJETO DEVERÁ ESPECIFICAR AS CONDIÇÕES DE FIXAÇÃO, INCLUINDO SUPORTES, ÂNCORAGENS E DETALHES DE ACABAMENTO, RESPEITANDO AS NORMAS DE SEGURANÇA E DESEMPENHO.


PARADES EXTERNAS	
1	REVESTIMENTO FULGET NA COR CINZA MÉDIO COM JUNTAS DE DILATAÇÃO HORIZONTAIS DE 1" (2,54CM)
2	REVESTIMENTO FULGET NA COR CINZA CLARO COM JUNTAS DE DILATAÇÃO HORIZONTAIS DE 1" (2,54CM)
3	REVESTIMENTO FULGET NA COR VERMELHO
4	ESTRUTURA METÁLICA FIXADA NA FACHADA REVESTIDA COM PAINEL DE ACM NA COR VERMELHO PADRÃO SÃO CAMILO (VIDE PROJETO ESPECÍFICO)
5	ESTRUTURA METÁLICA FIXADA NA FACHADA REVESTIDA COM PAINEL DE ACM NA CINZA MÉDIO (VIDE PROJETO ESPECÍFICO)
6	TIJULO DE VIDRO 190X190X80MM ONDULADO INCOLOR, E BARRAS DE AÇO DE 5MM DE DIÂMETRO PARA TRAVAMENTO VERTICAL E HORIZONTAL_A INSTALAR
7	TIJULO DE VIDRO 200X200X60MM COM VENTILAÇÃO, INCOLOR E BARRAS DE AÇO DE 5MM DE DIÂMETRO PARA TRAVAMENTO VERTICAL E HORIZONTAL_A INSTALAR
8	CERÂMICA 100X100 EXISTENTE_A MANTER
9	MARQUISE EXISTENTE REVESTIDA EM CHAPA METÁLICA, PREVER NOVA PINTURA NA COR VERMELHO PADRÃO SÃO CAMILO
10	RECOMPOSIÇÃO EM MASSA COM PINTURA NA COR CINZA MÉDIO

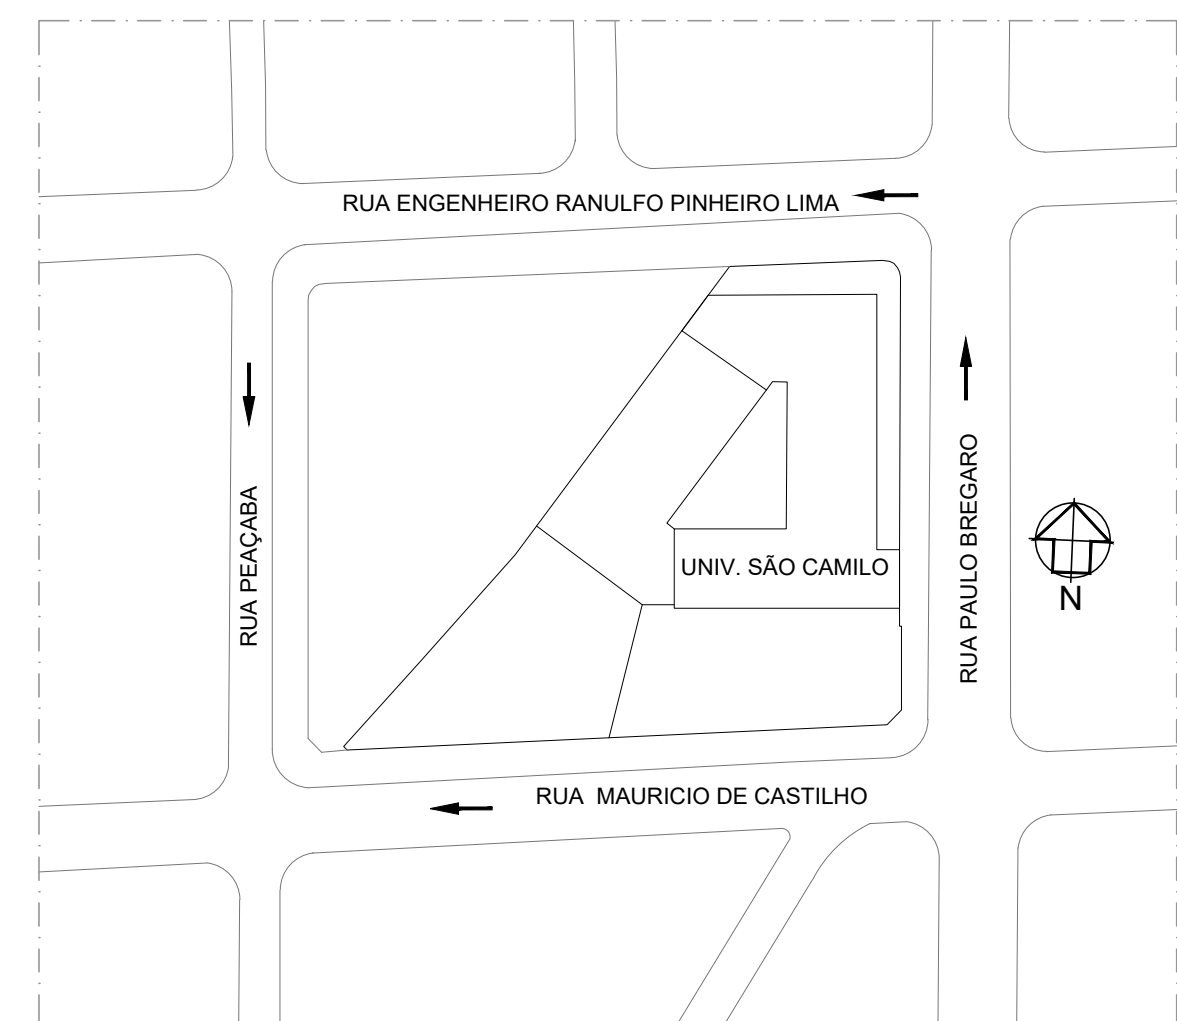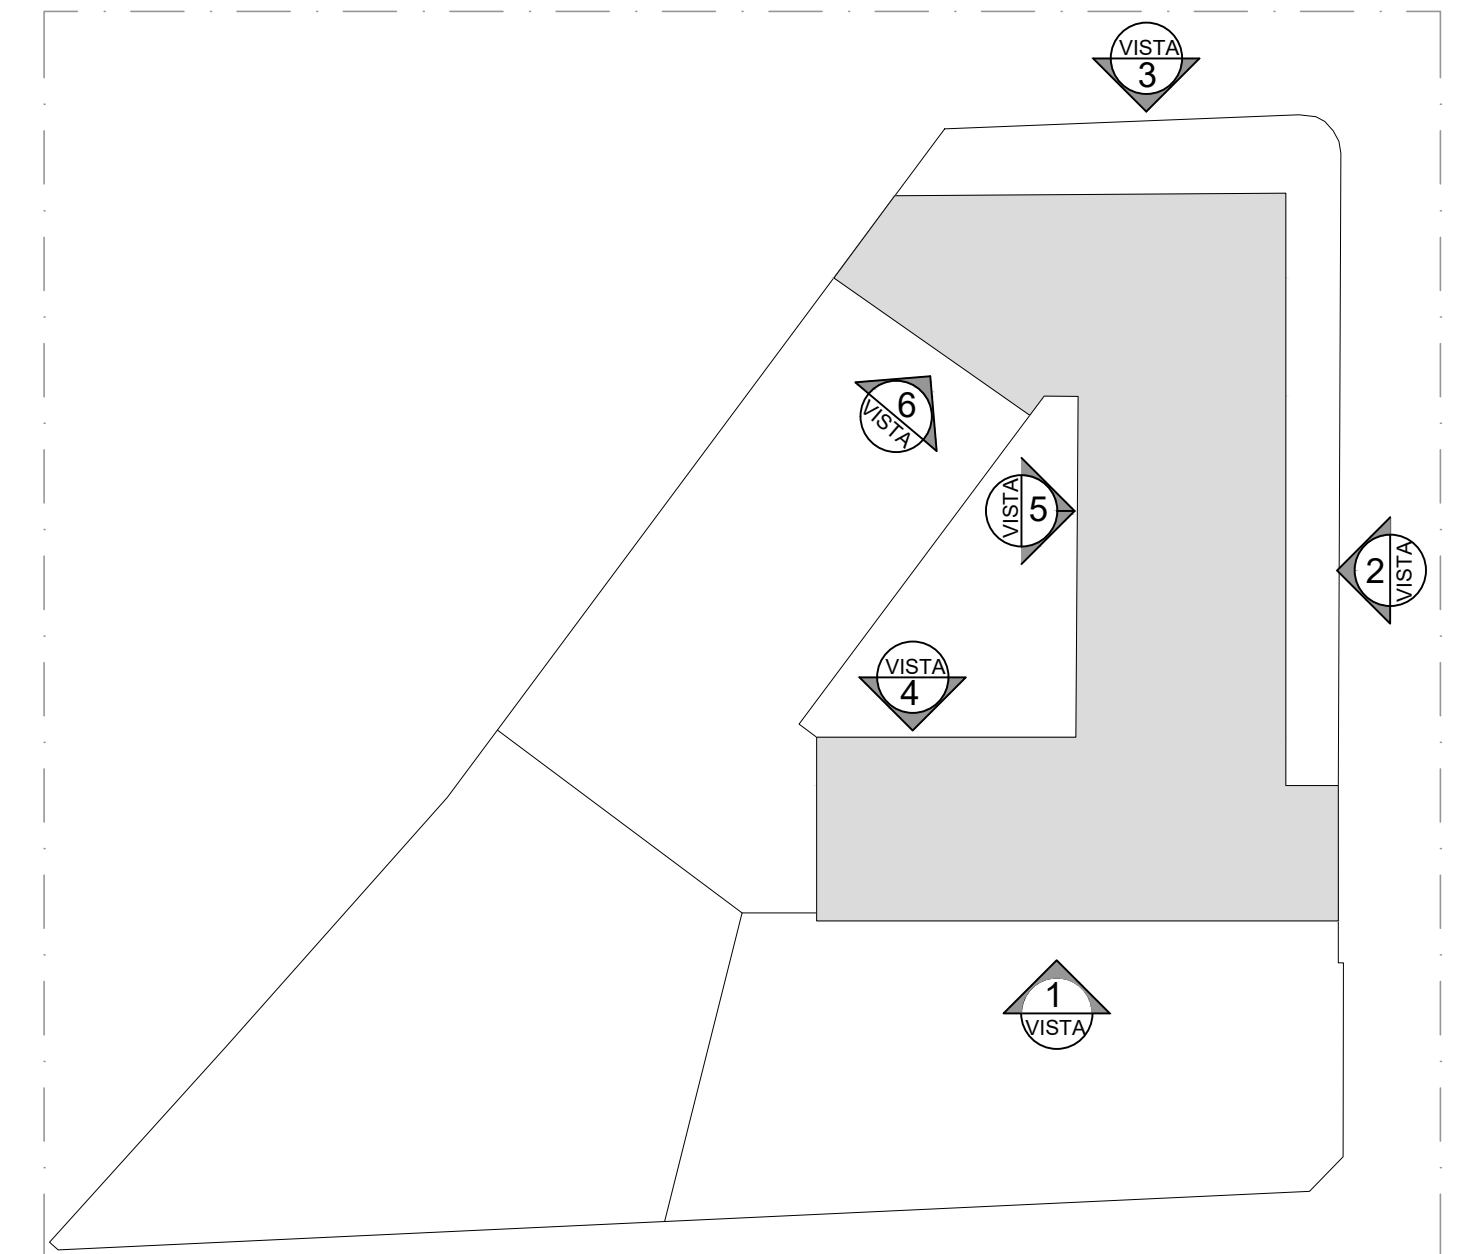

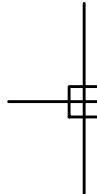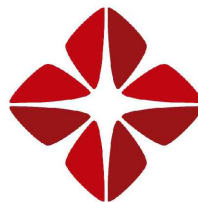
02	27.07.26	MUDANÇA NOS FORMATOS CONF. SOLICITAÇÃO DA ENGª DO SÃO CAMILO
01	07.11.24	REVISÃO GERAL CONFORME APONTAMENTOS
REVISÃO:	DATA:	DESCRIÇÃO:
PROJETISTA:  MP ARQUITETURA ARQUITETURA & CONSULTORIA		CLIENTE:  CENTRO UNIVERSITÁRIO SÃO CAMILO
PROJETO: UNIVERSIDADE SÃO CAMILO - UNIDADE IPIRANGA PROMOVE		REVISÃO: 02
ASSUNTO: REFORMA DE FACHADA / EXECUTIVO		
PISO/ FACHADA 01- DETALHES		FOLHA: 03 / 12
RESPONSÁVEL TÉCNICO: MAURO PEREIRA FILHO		
CAU DO RESPONSÁVEL TÉCNICO A - 7458-6		
		RRT

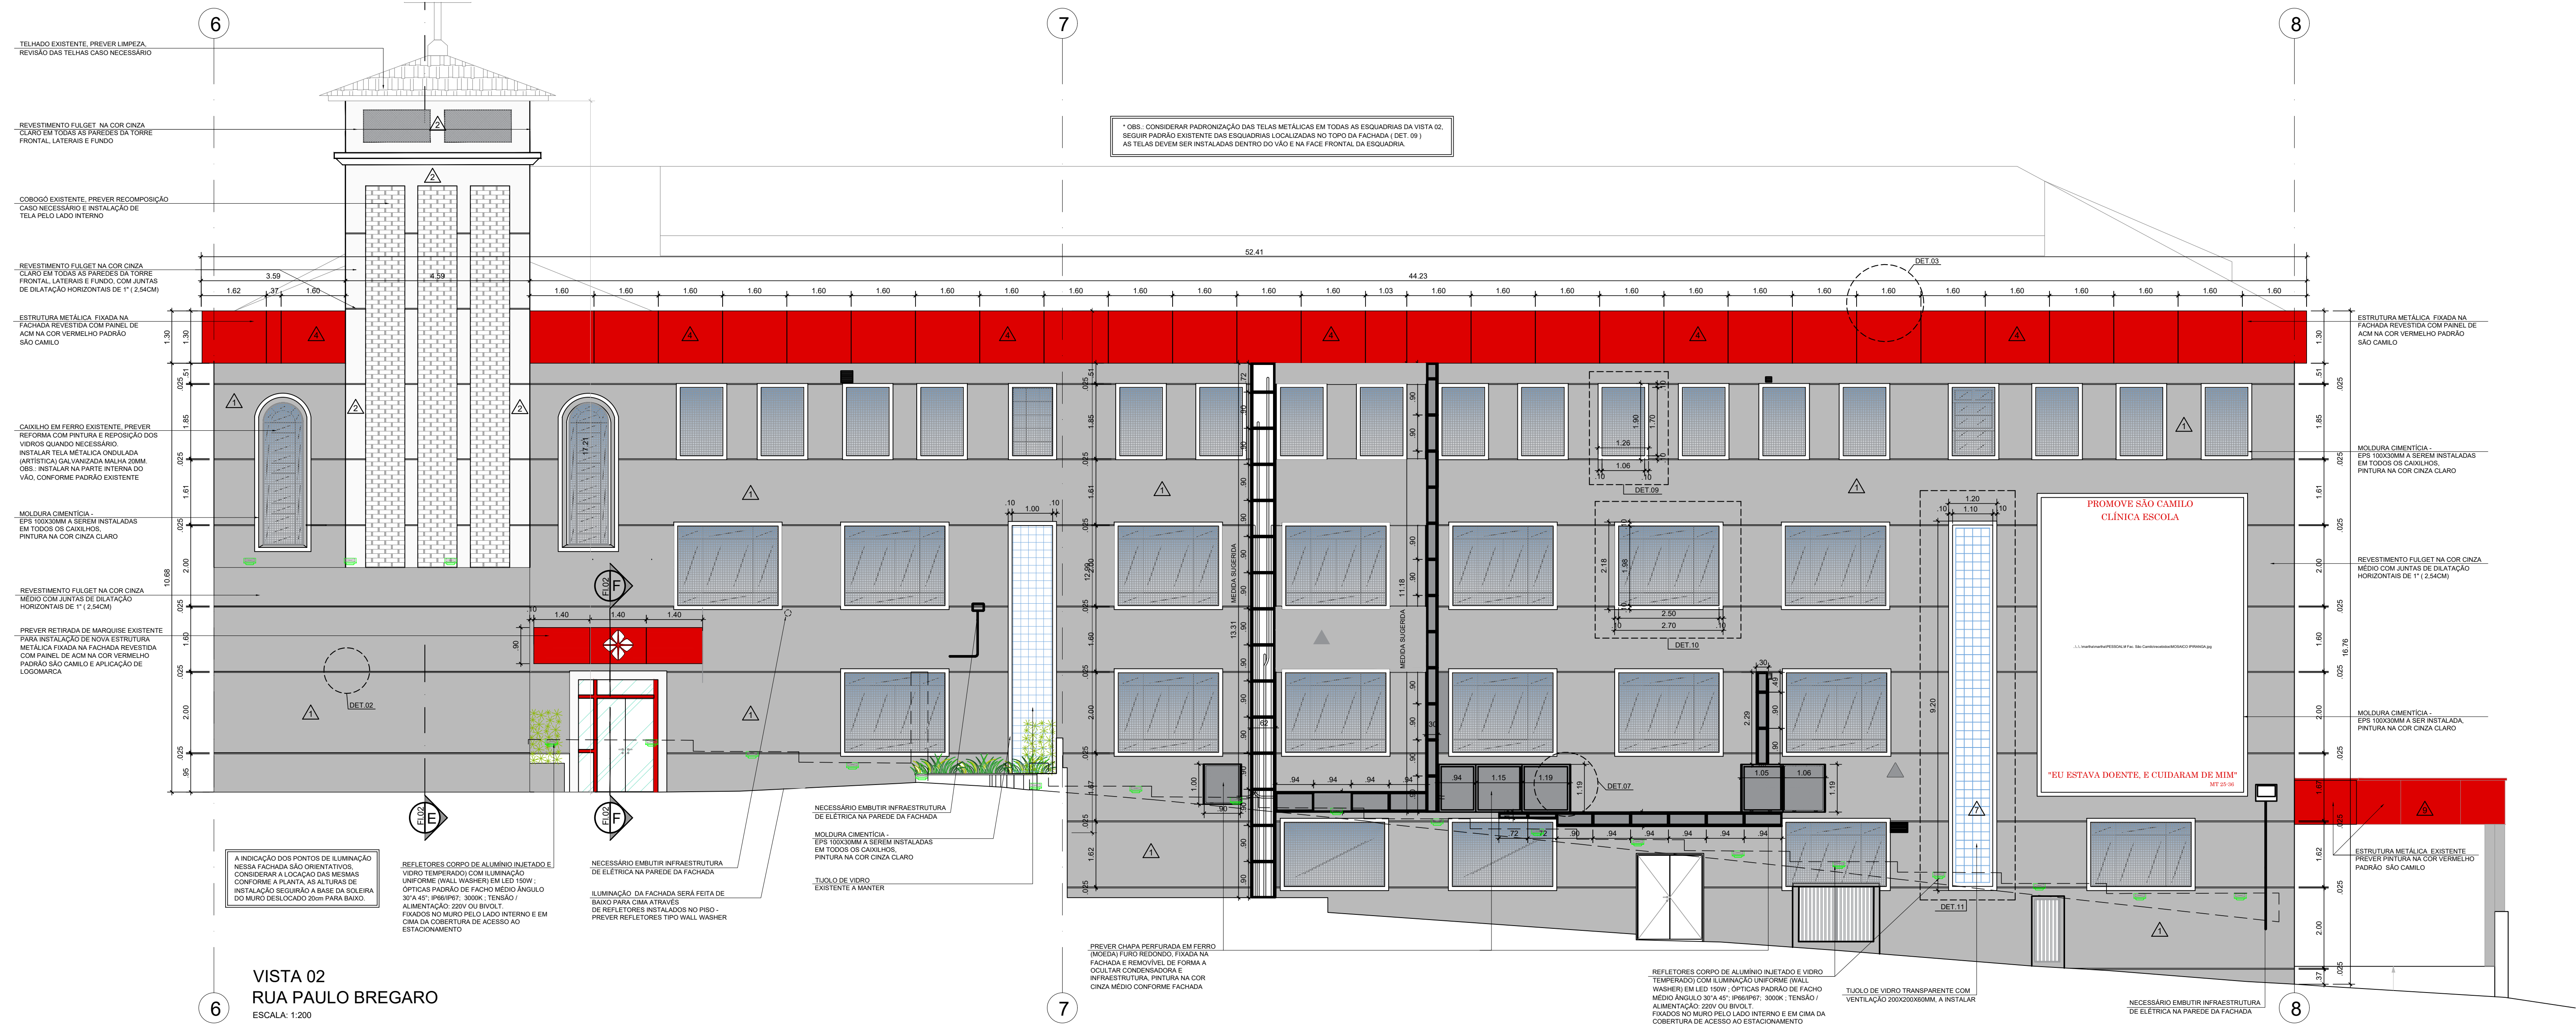

VISTA 02
RUA PAULO BREGARO
ESCALA: 1:200

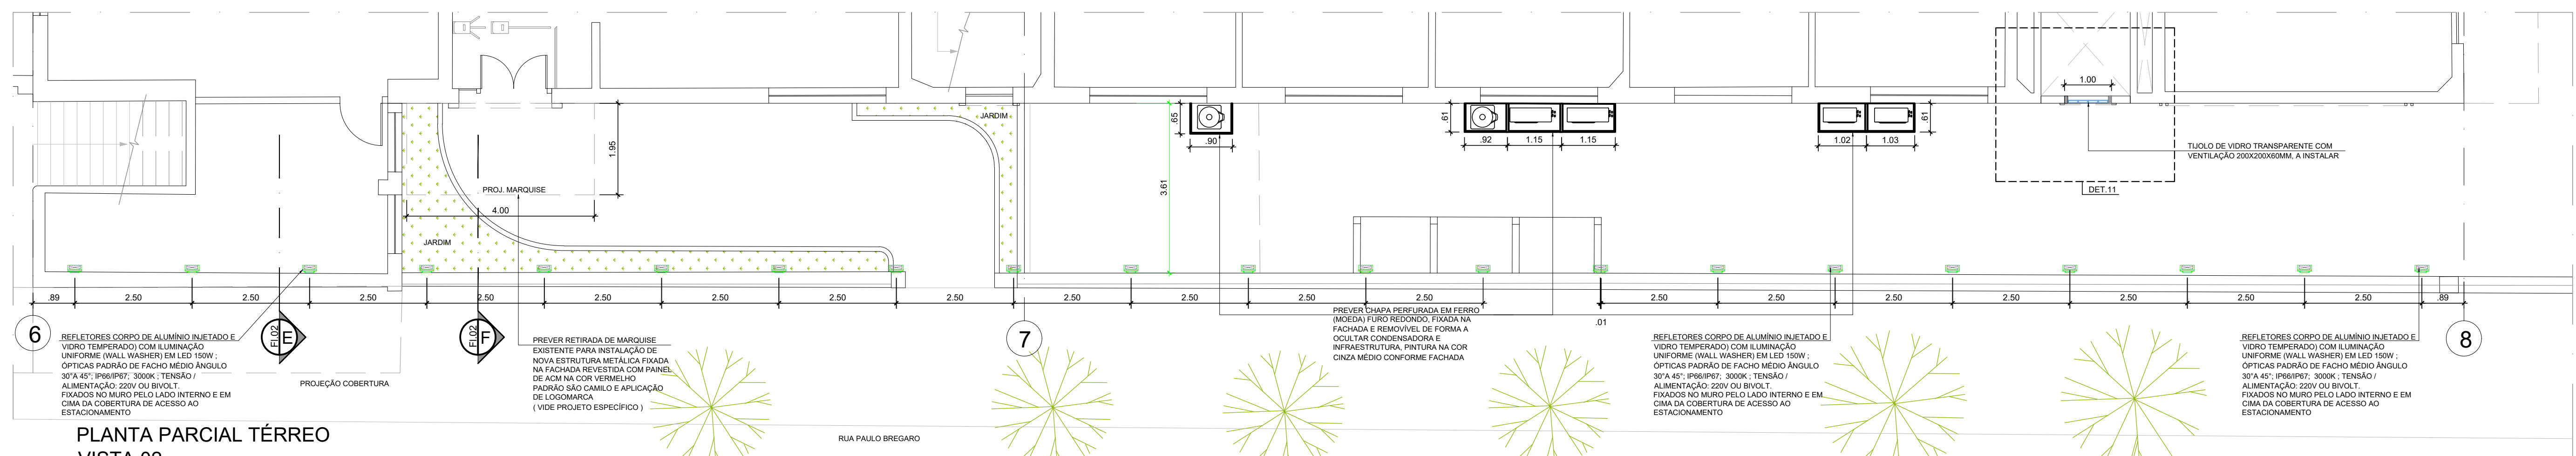

PLANTA PARCIAL TÉRREO
VISTA 02
ESCALA: 1:200

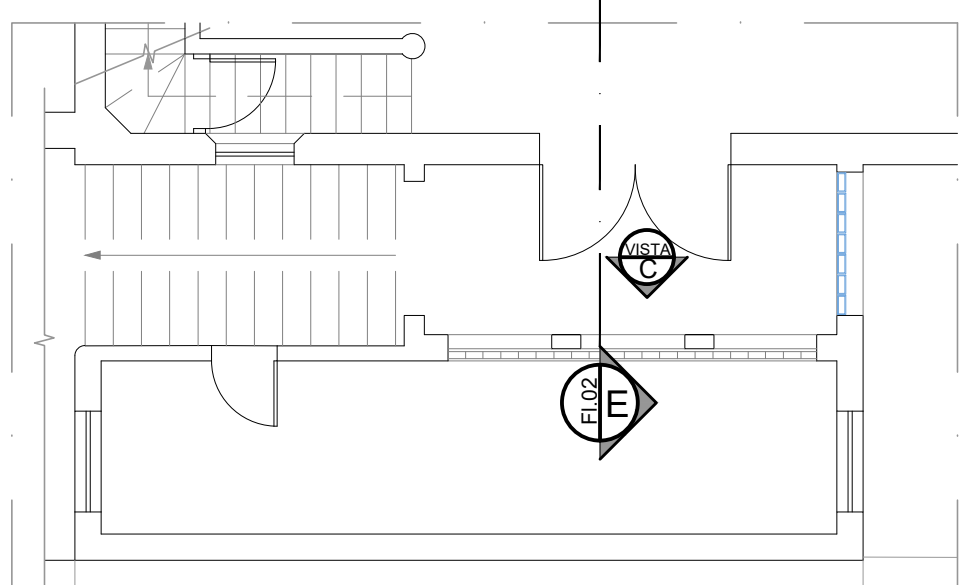



PLANTA PARCIAL 1º ANDAR
VISTA 02
ESCALA: 1:200

IMPORTANTE:
NOTA TÉCNICA: PROJETO DE FACHADA INSTALAÇÃO DE ACM **
A INSTALAÇÃO DE ACM NA FACHADA DO EDIFÍCIO REQUER A ELABORAÇÃO DE UM PROJETO ESPECÍFICO, QUE CONTEMPLE TODOS OS DETALHES TÉCNICOS E ESTRUTURAS NECESSÁRIAS PARA GARANTIR A EXECUÇÃO SEGURA, EFICIENTE E ESTETICAMENTE SATISFATORIA DO MATERIAL. O PROJETO DEVERÁ ESPECIFICAR AS CONDIÇÕES DE FACHADA, INCLUINDO SUPORTES, ANCORAGENS E DETALHES DE ACABAMENTO, RESPEITANDO AS NORMAS DE SEGURANÇA E DESEMPENHO.


LEGENDA DE ACABAMENTOS

PAREDES EXTERNAS


- 1 REVESTIMENTO FLISSET NA COR CINZA CLARO COM JUNTAS DE DILATAÇÃO HORIZONTAIS DE 1" (2,54CM)
- 2 REVESTIMENTO FLISSET NA COR CINZA CLARO COM JUNTAS DE DILATAÇÃO HORIZONTAIS DE 1" (2,54CM)
- 3 REVESTIMENTO FLISSET NA COR VERMELHO
- 4 ESTRUTURA METÁLICA FIXADA NA FACHADA REVESTIDA COM PAINEL DE ACM NA COR VERMELHO PADRÃO SÃO CAMILO (VER PROJETO ESPECÍFICO)
- 5 ESTRUTURA METÁLICA FIXADA NA FACHADA REVESTIDA COM PAINEL DE ACM NA COR CINZA MÉDIO (VER PROJETO ESPECÍFICO)
- 6 TUBO DE VÍDEO TRANSPARENTE INCLINADO 90GRº E BARRAS DE AÇO DE 3MM DE DIÂMETRO PARA TRATAMENTO VERTICAL E HORIZONTAL A INSTALAR
- 7 TUBO DE VÍDEO TRANSPARENTE COM VENTILAÇÃO INCLINADO E BARRAS DE AÇO DE 3MM DE DIÂMETRO PARA TRATAMENTO VERTICAL E HORIZONTAL A INSTALAR
- 8 CORDOEA VERMELHO EXISTENTE A MANEIRAR
- 9 MARQUESE EXISTENTE REVESTIDA EM CHAPA METÁLICA, PREVER NOVA PINTURA NA COR VERMELHO PADRÃO SÃO CAMILO
- 10 RECOMPOSIÇÃO EM MASSA COM PINTURA NA COR CINZA MÉDIO

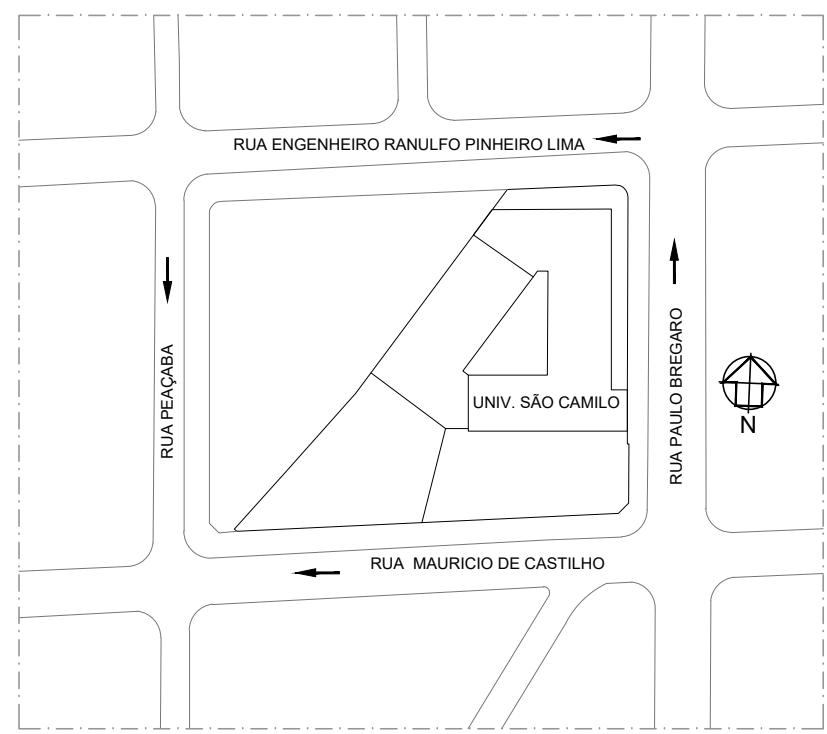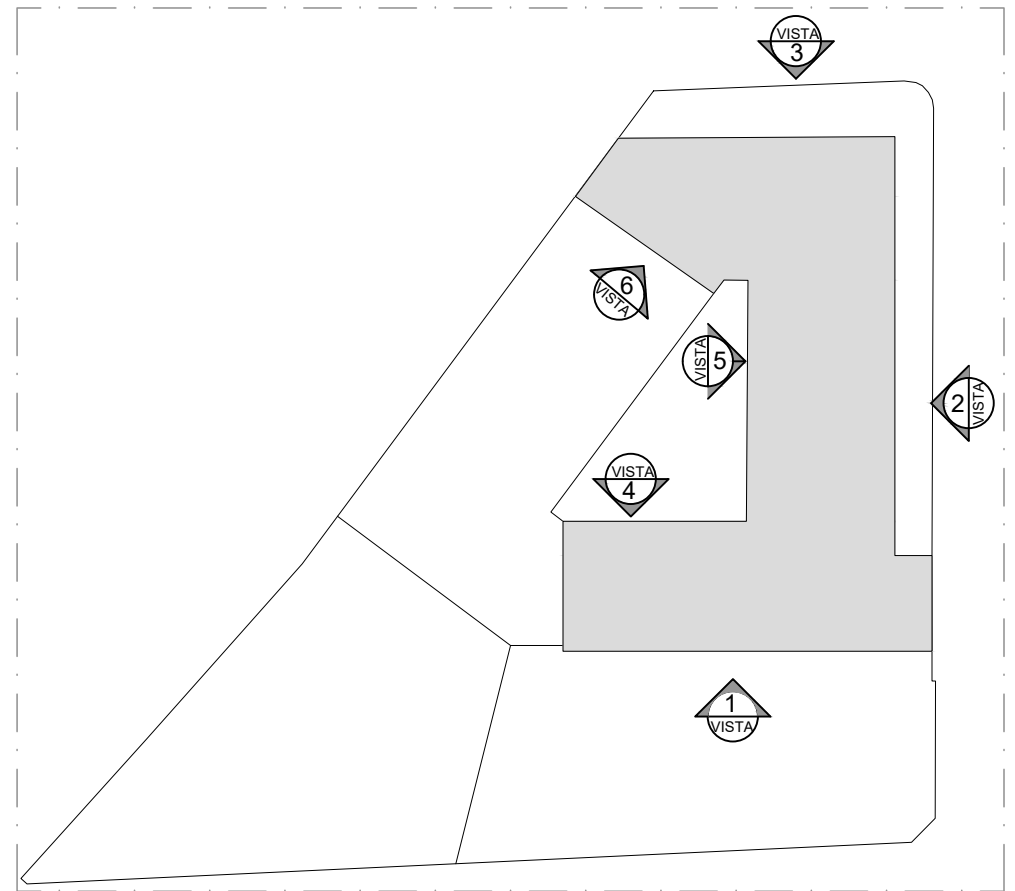


02	27.07.28	MUDANÇA NOS FORMATOS CONF. SOLICITAÇÃO DA ENGº DO SÃO CAMILO
01	07.11.24	REVISÃO GERAL CONFORME APONTAMENTOS
REVISÃO:	DATA:	DESCRIÇÃO:
PROJETISTA:	CLIENTE:	
MP ARQUITETURA ARQUITETURA & CONSULTORIA	CENTRO UNIVERSITÁRIO SÃO CAMILO	
PROJETO:	UNIVERSIDADE SÃO CAMILO - UNIDADE IPIRANGA PROMOVE	
ASSUNTO:	REFORMA DE FACHADA / EXECUTIVO	
PROJ:	FACHADA 02- PLANTAS PARCIAIS	ESQ: INDICADA
RESPONSÁVEL TÉCNICO:	MAURO PEREIRA FILHO	DATA: 04.05.23
CAU DO RESPONSÁVEL TÉCNICO:	A - 74586	RTT
REVISÃO:	02	FOLHA: 04/12

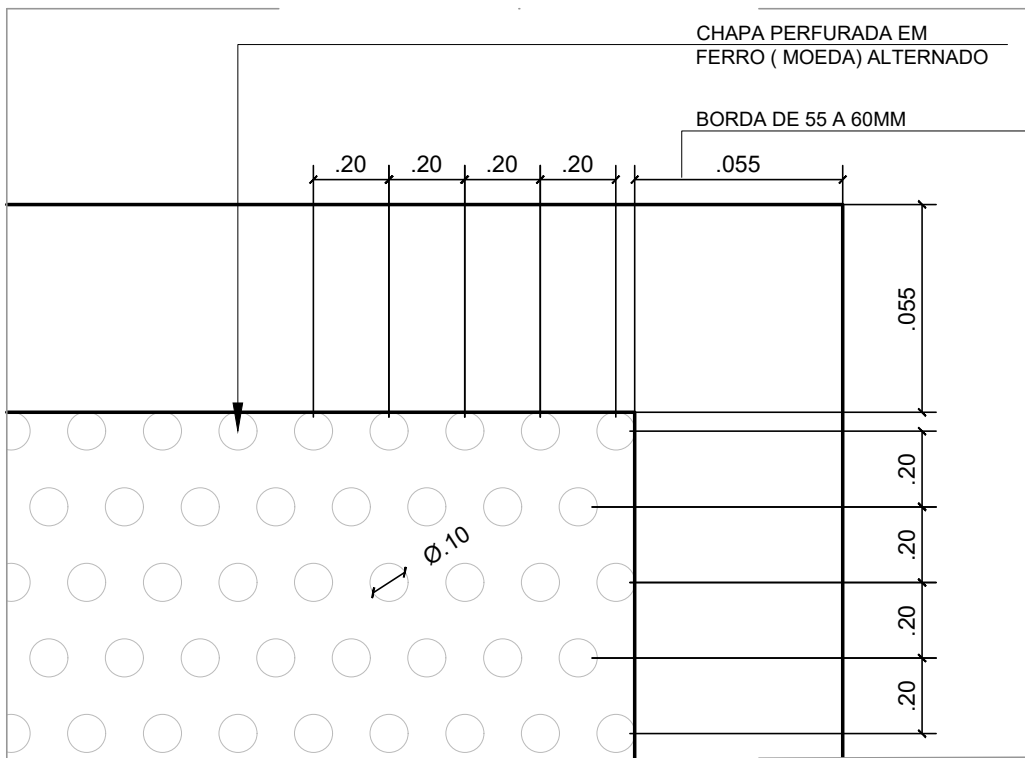



DET. 07
ESCALA 1:25

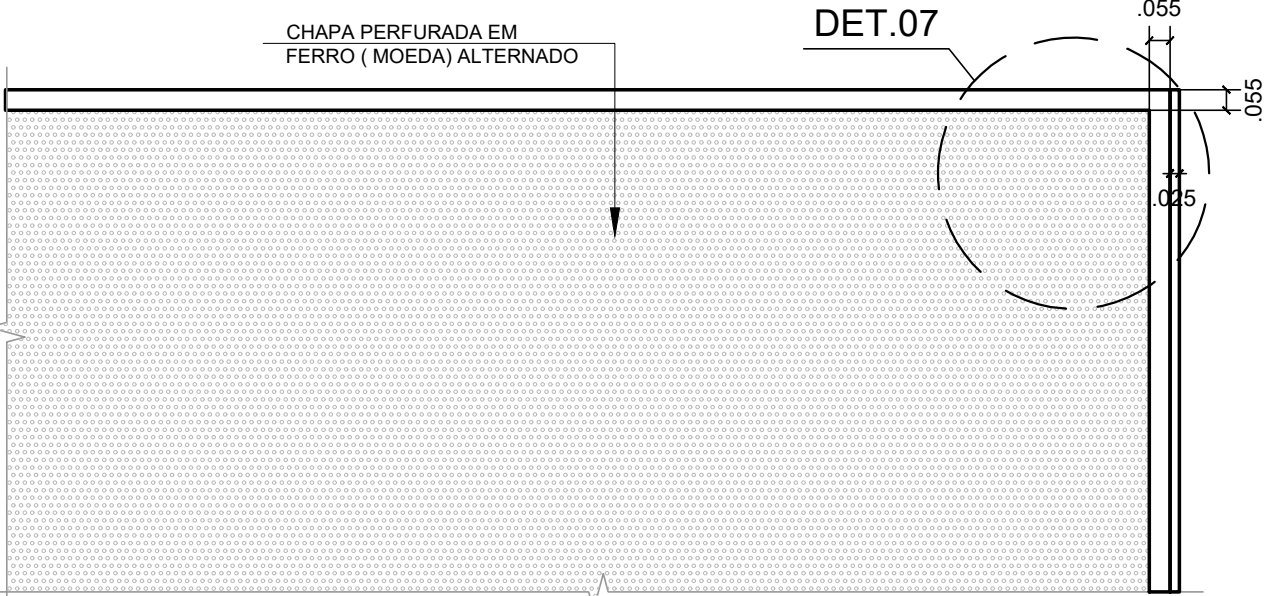


DET. 07
VISTA DA CHAPA PERFORADA
ESCALA 1:25

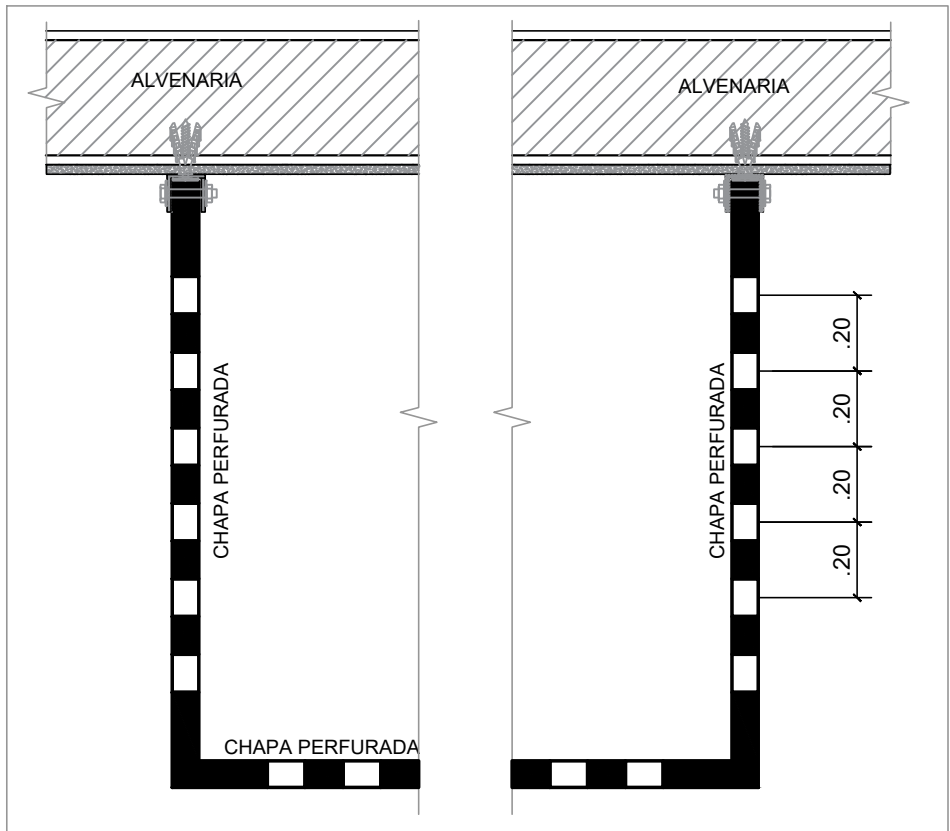


DET. 07- GENÉRICO
FIXAÇÃO DA CHAPA PERFORADA
ESCALA 1:25

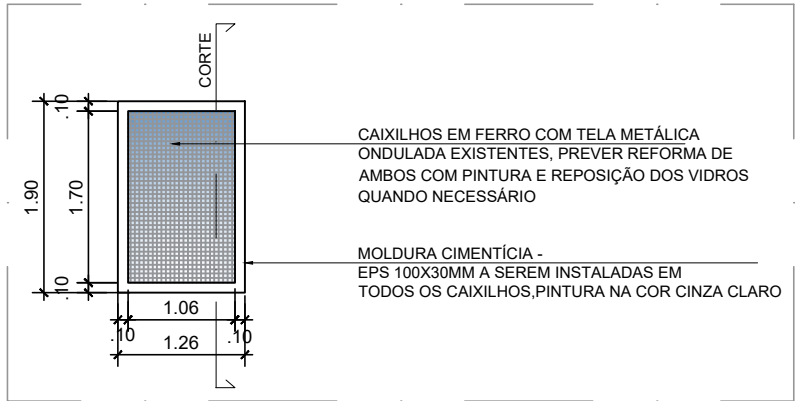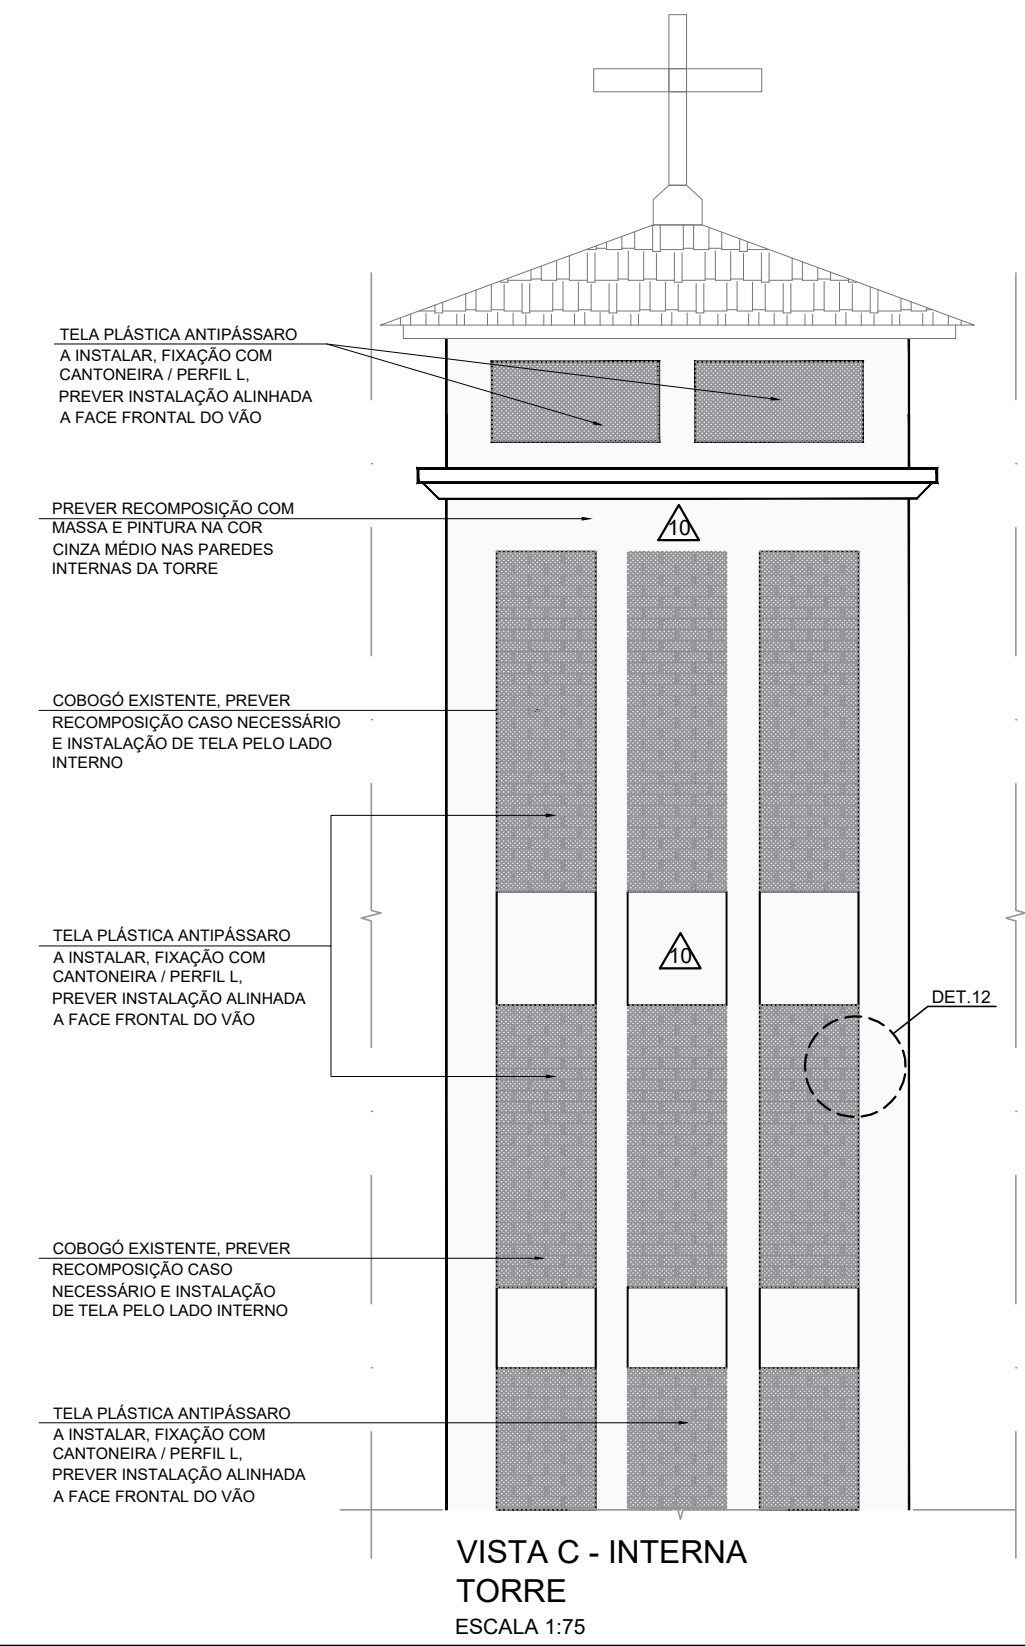

DET. 09
VISTA 1
(COM TELA METÁLICA)
ESCALA 1:75

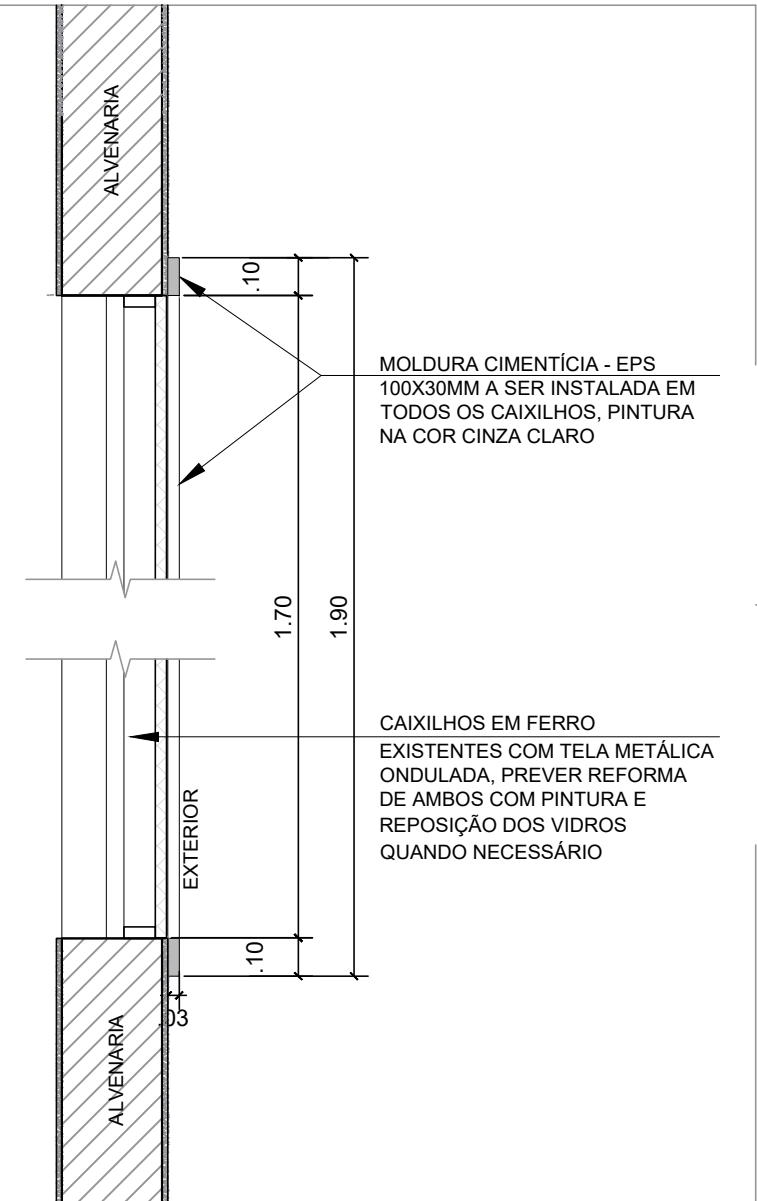


DET. 09
CORTE
(COM TELA METÁLICA)
ESCALA 1:25

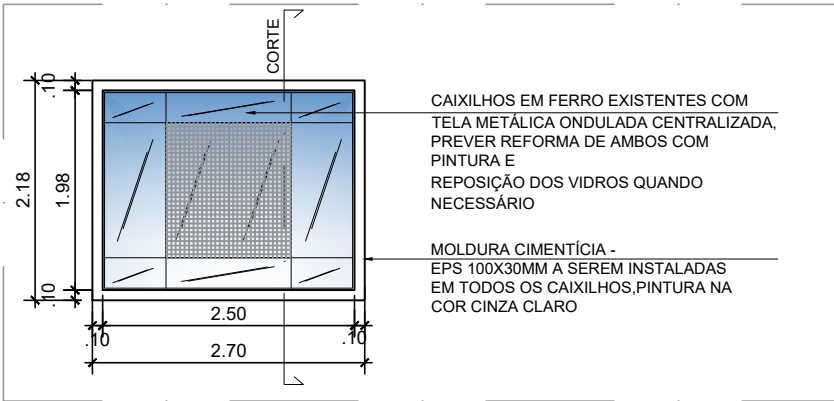


DET. 10
VISTA 3
(COM TELA METÁLICA)
ESCALA 1:75




DET. 10
CORTE
(COM TELA METÁLICA)
ESCALA 1:25

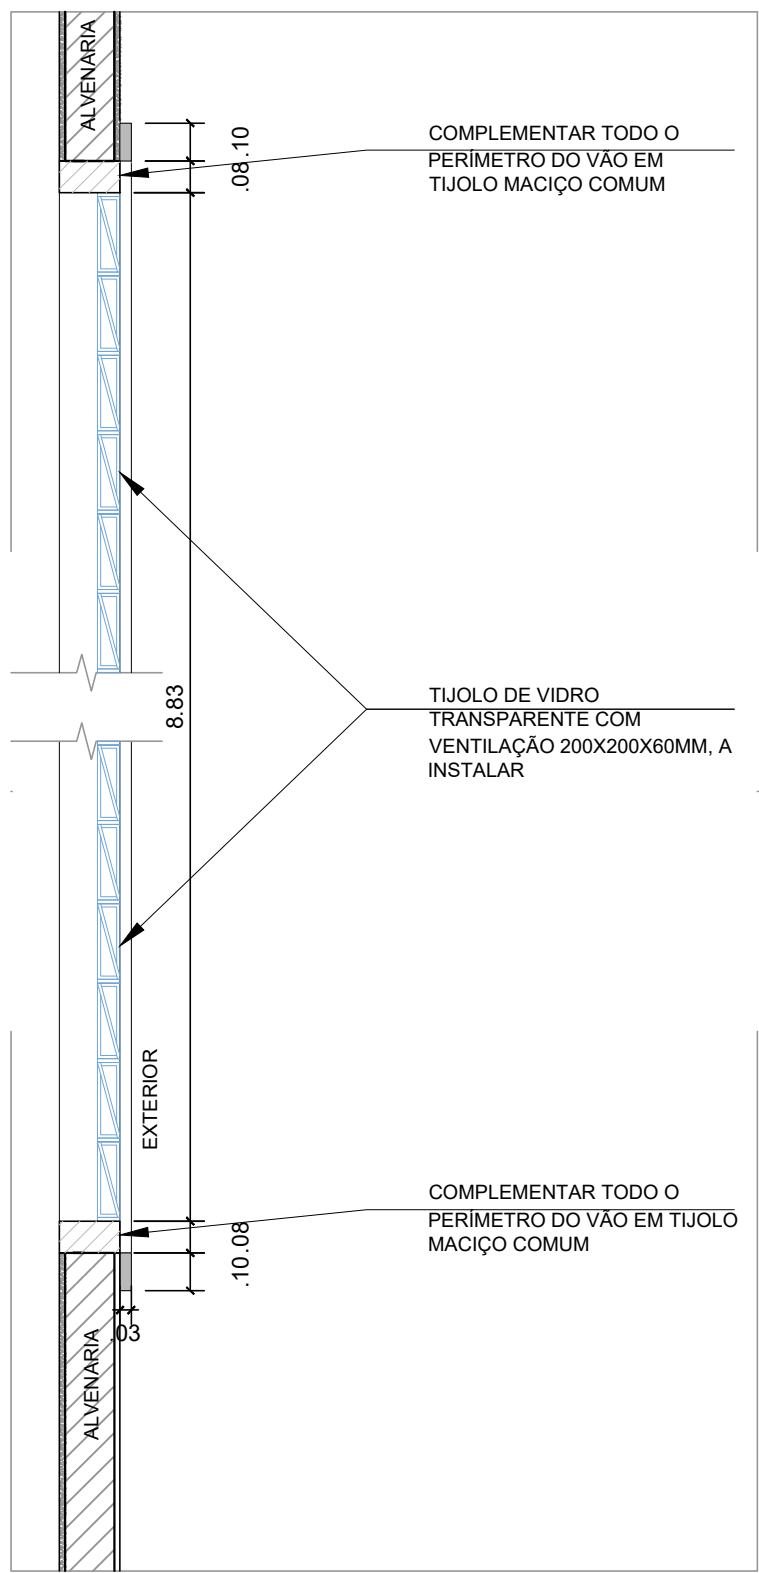


DET. 11- CORTE
(TIJOLO DE VIDRO)
ESCALA 1:25

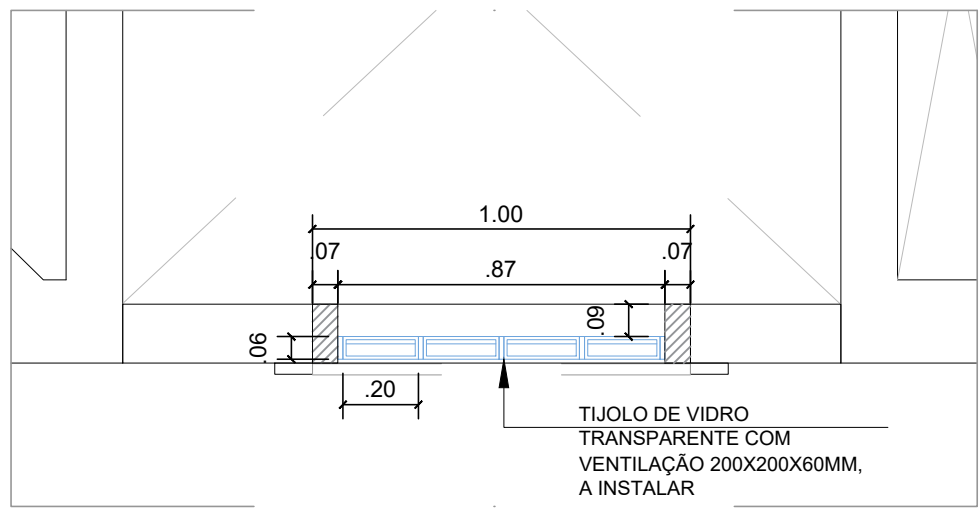


DET. 11- PLANTA
(TIJOLO DE VIDRO)
ESCALA 1:25

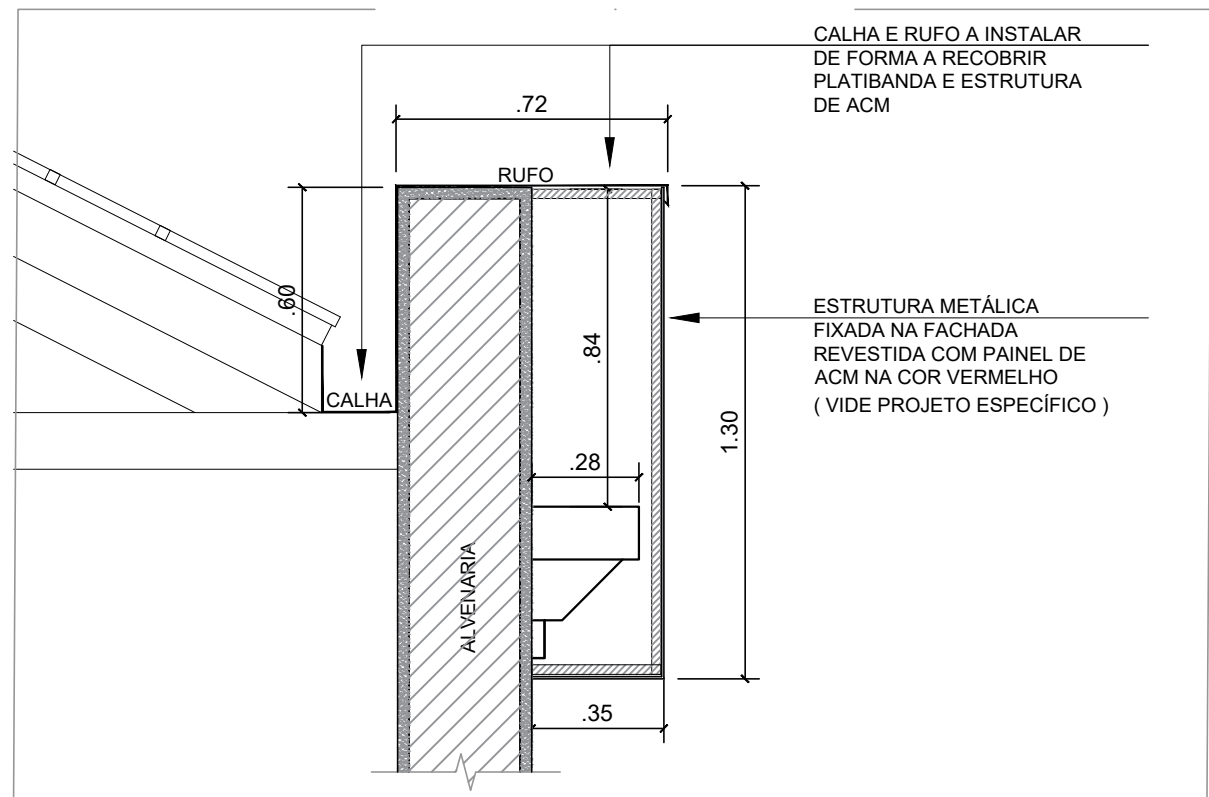


DET. 03
ORIENTATIVO
ESCALA 1:25

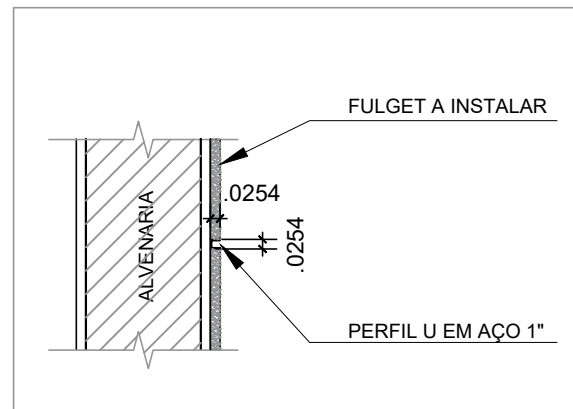


DET. 02
ESCALA 1:25

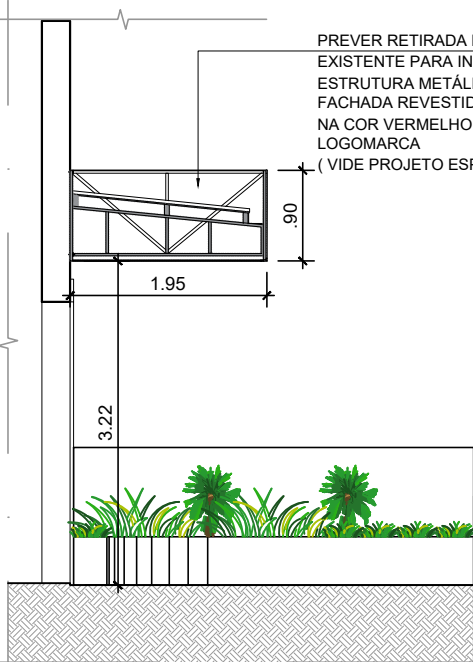


CORTE F-F
ESCALA 1:75

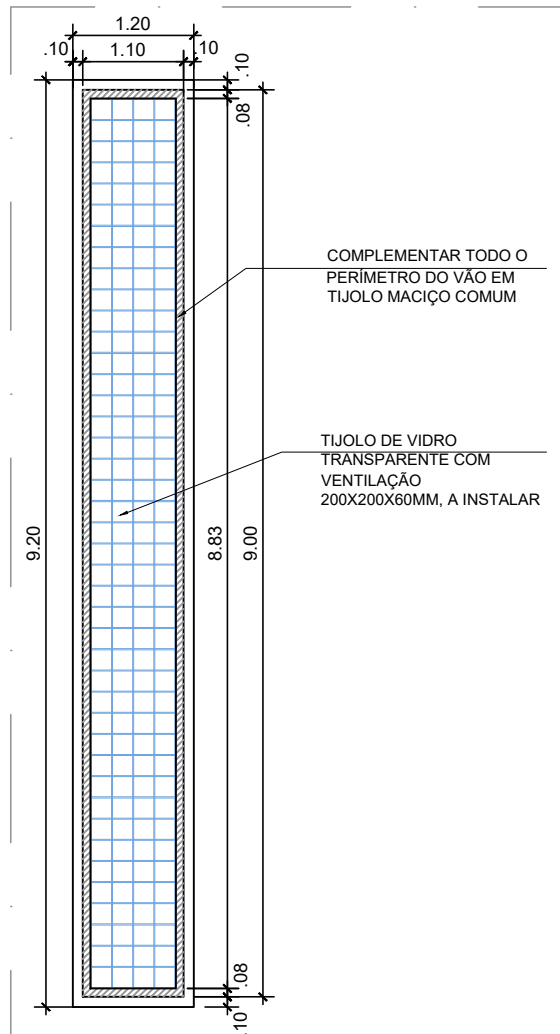

DET. 11
VISTA 2
ESCALA 1:75

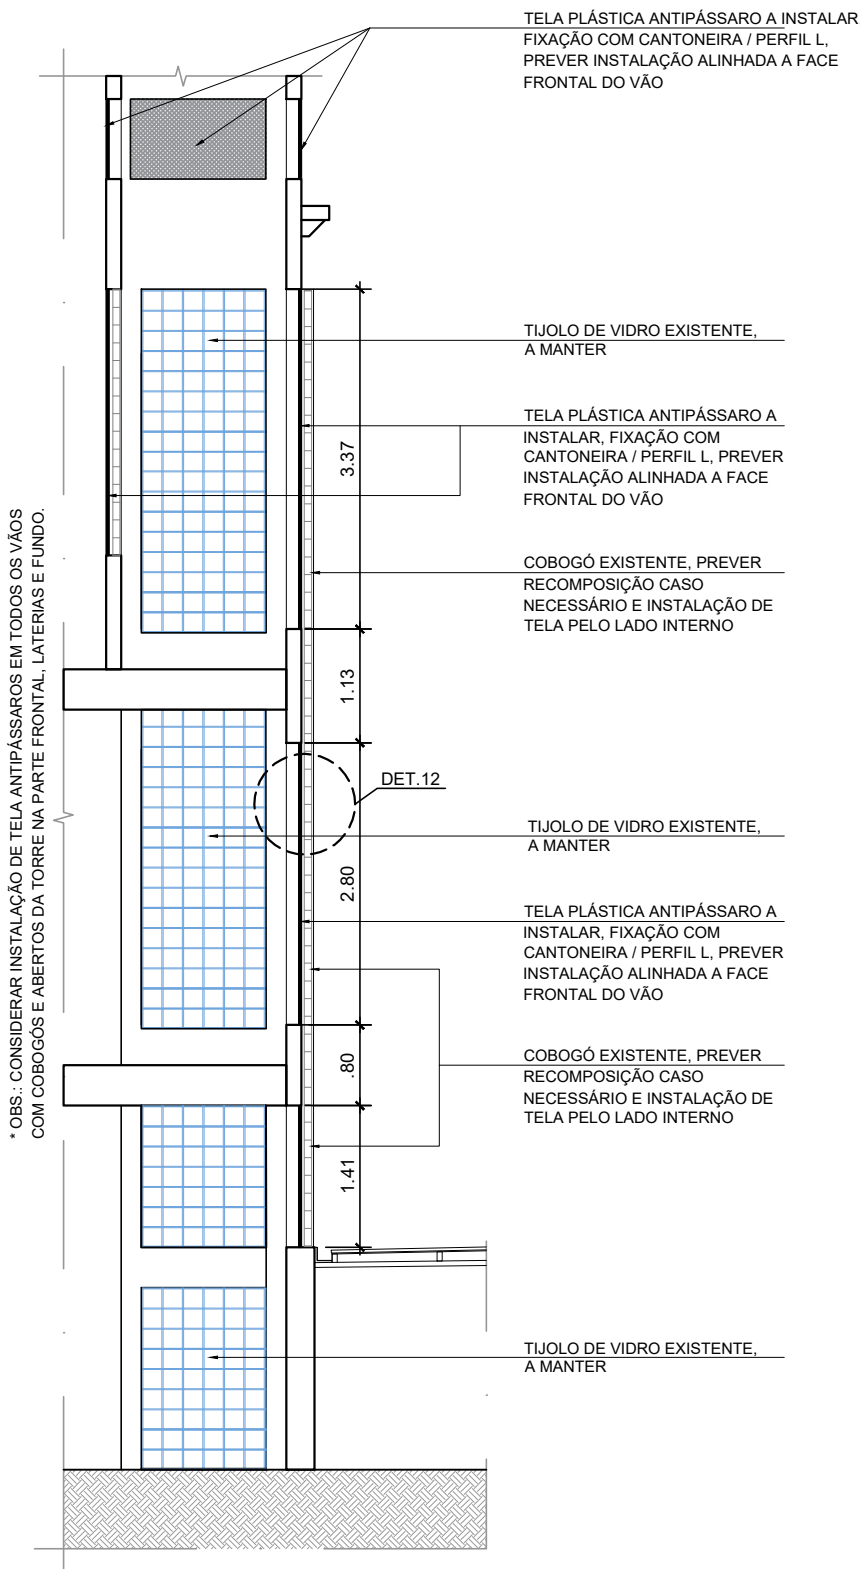



CORTE E-E
ESCALA 1:75

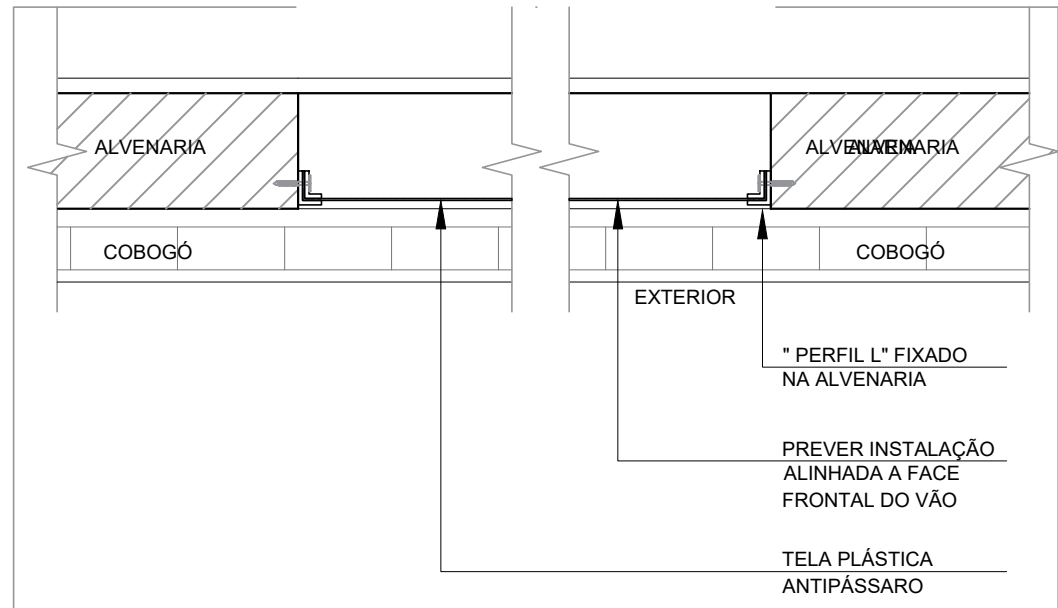


DET. 12
ESCALA 1:25

LEGENDA DE ACABAMENTOS

△	PARQUES EXTERNAS
1	REVESTIMENTO FULGET NA COR CINZA MÉDIO COM JUNTAS DE DILATAÇÃO HORIZONTAIS DE 1" (2,54CM)
2	REVESTIMENTO FULGET NA COR CINZA CLARO COM JUNTAS DE DILATAÇÃO HORIZONTAIS DE 1" (2,54CM)
3	REVESTIMENTO FULGET NA COR VERMELHO
4	ESTRUTURA METÁLICA FIXADA NA FACHADA REVESTIDA COM PAINEL DE ACM NA COR VERMELHO PADRÃO SÃO CAMILO (VIDE PROJETO ESPECÍFICO)
5	ESTRUTURA METÁLICA FIXADA NA FACHADA REVESTIDA COM PAINEL DE ACM NA CINZA MÉDIO (VIDE PROJETO ESPECÍFICO)
6	TIJOLO DE VIDRO 190X190X80MM ONDULADO INCOLOR, E BARRAS DE AÇO DE 5MM DE DIÂMETRO PARA TRAVAMENTO VERTICAL E HORIZONTAL A INSTALAR
7	TIJOLO DE VIDRO 200X200X60MM COM VENTILAÇÃO, INCOLOR E BARRAS DE AÇO DE 5MM DE DIÂMETRO PARA TRAVAMENTO VERTICAL E HORIZONTAL A INSTALAR
8	CERÂMICA 100X100 EXISTENTE A MANTER
9	MARQUISE EXISTENTE REVESTIDA EM CHAPA METÁLICA, PREVER NOVA PINTURA NA COR VERMELHO PADRÃO SÃO CAMILO
10	RECOMPOSIÇÃO EM MASSA COM PINTURA NA COR CINZA MÉDIO

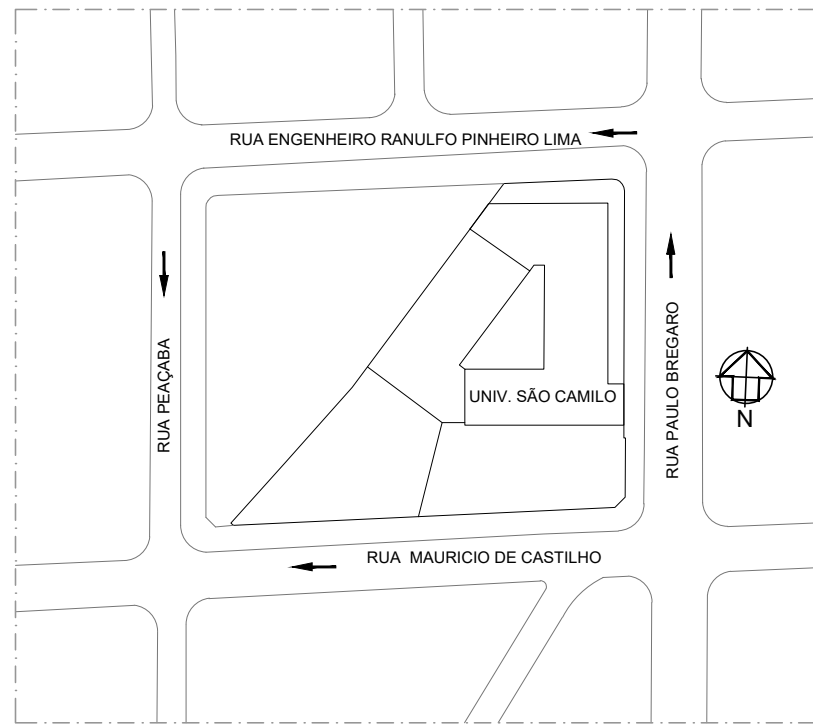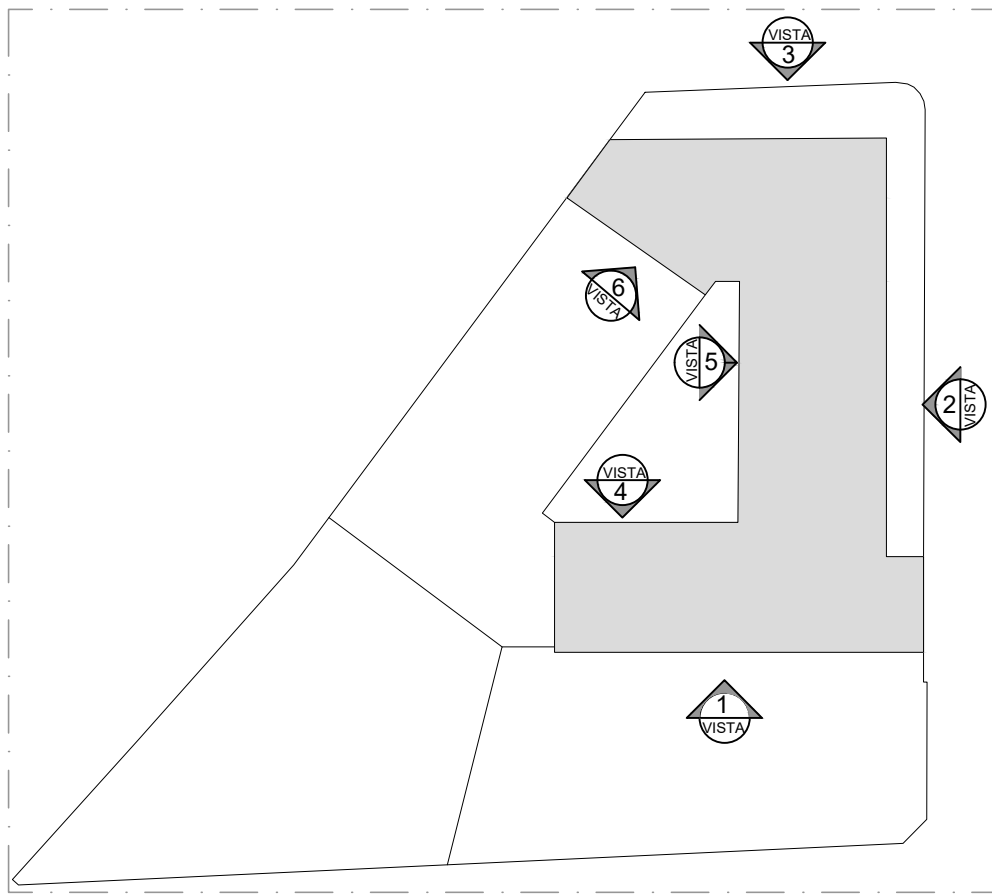


02	27.07.26	MUDANÇA NOS FORMATOS CONF. SOLICITAÇÃO DA ENGº DO SÃO CAMILO
01	07.11.24	REVISÃO GERAL CONFORME APONTAMENTOS
REVISÃO:	DATA:	DESCRIÇÃO:
PROJETISTA: MP ARQUITETURA ARQUITETURA & CONSULTORIA		
CLIENTE: CENTRO UNIVERSITÁRIO SÃO CAMILO		
PROJETO: UNIVERSIDADE SÃO CAMILO - UNIDADE IPIRANGA PROMOVE		
ASSUNTO: REFORMA DE FACHADA / EXECUTIVO		
PISO/ FACHADA 02- CORTES E DETALHES		
RESPONSÁVEL TÉCNICO: MAURO PEREIRA FILHO		
CAU DO RESPONSÁVEL TÉCNICO: A - 7458-6		
RRT		
REVISÃO: 02		
FOLHA: 05 / 12		

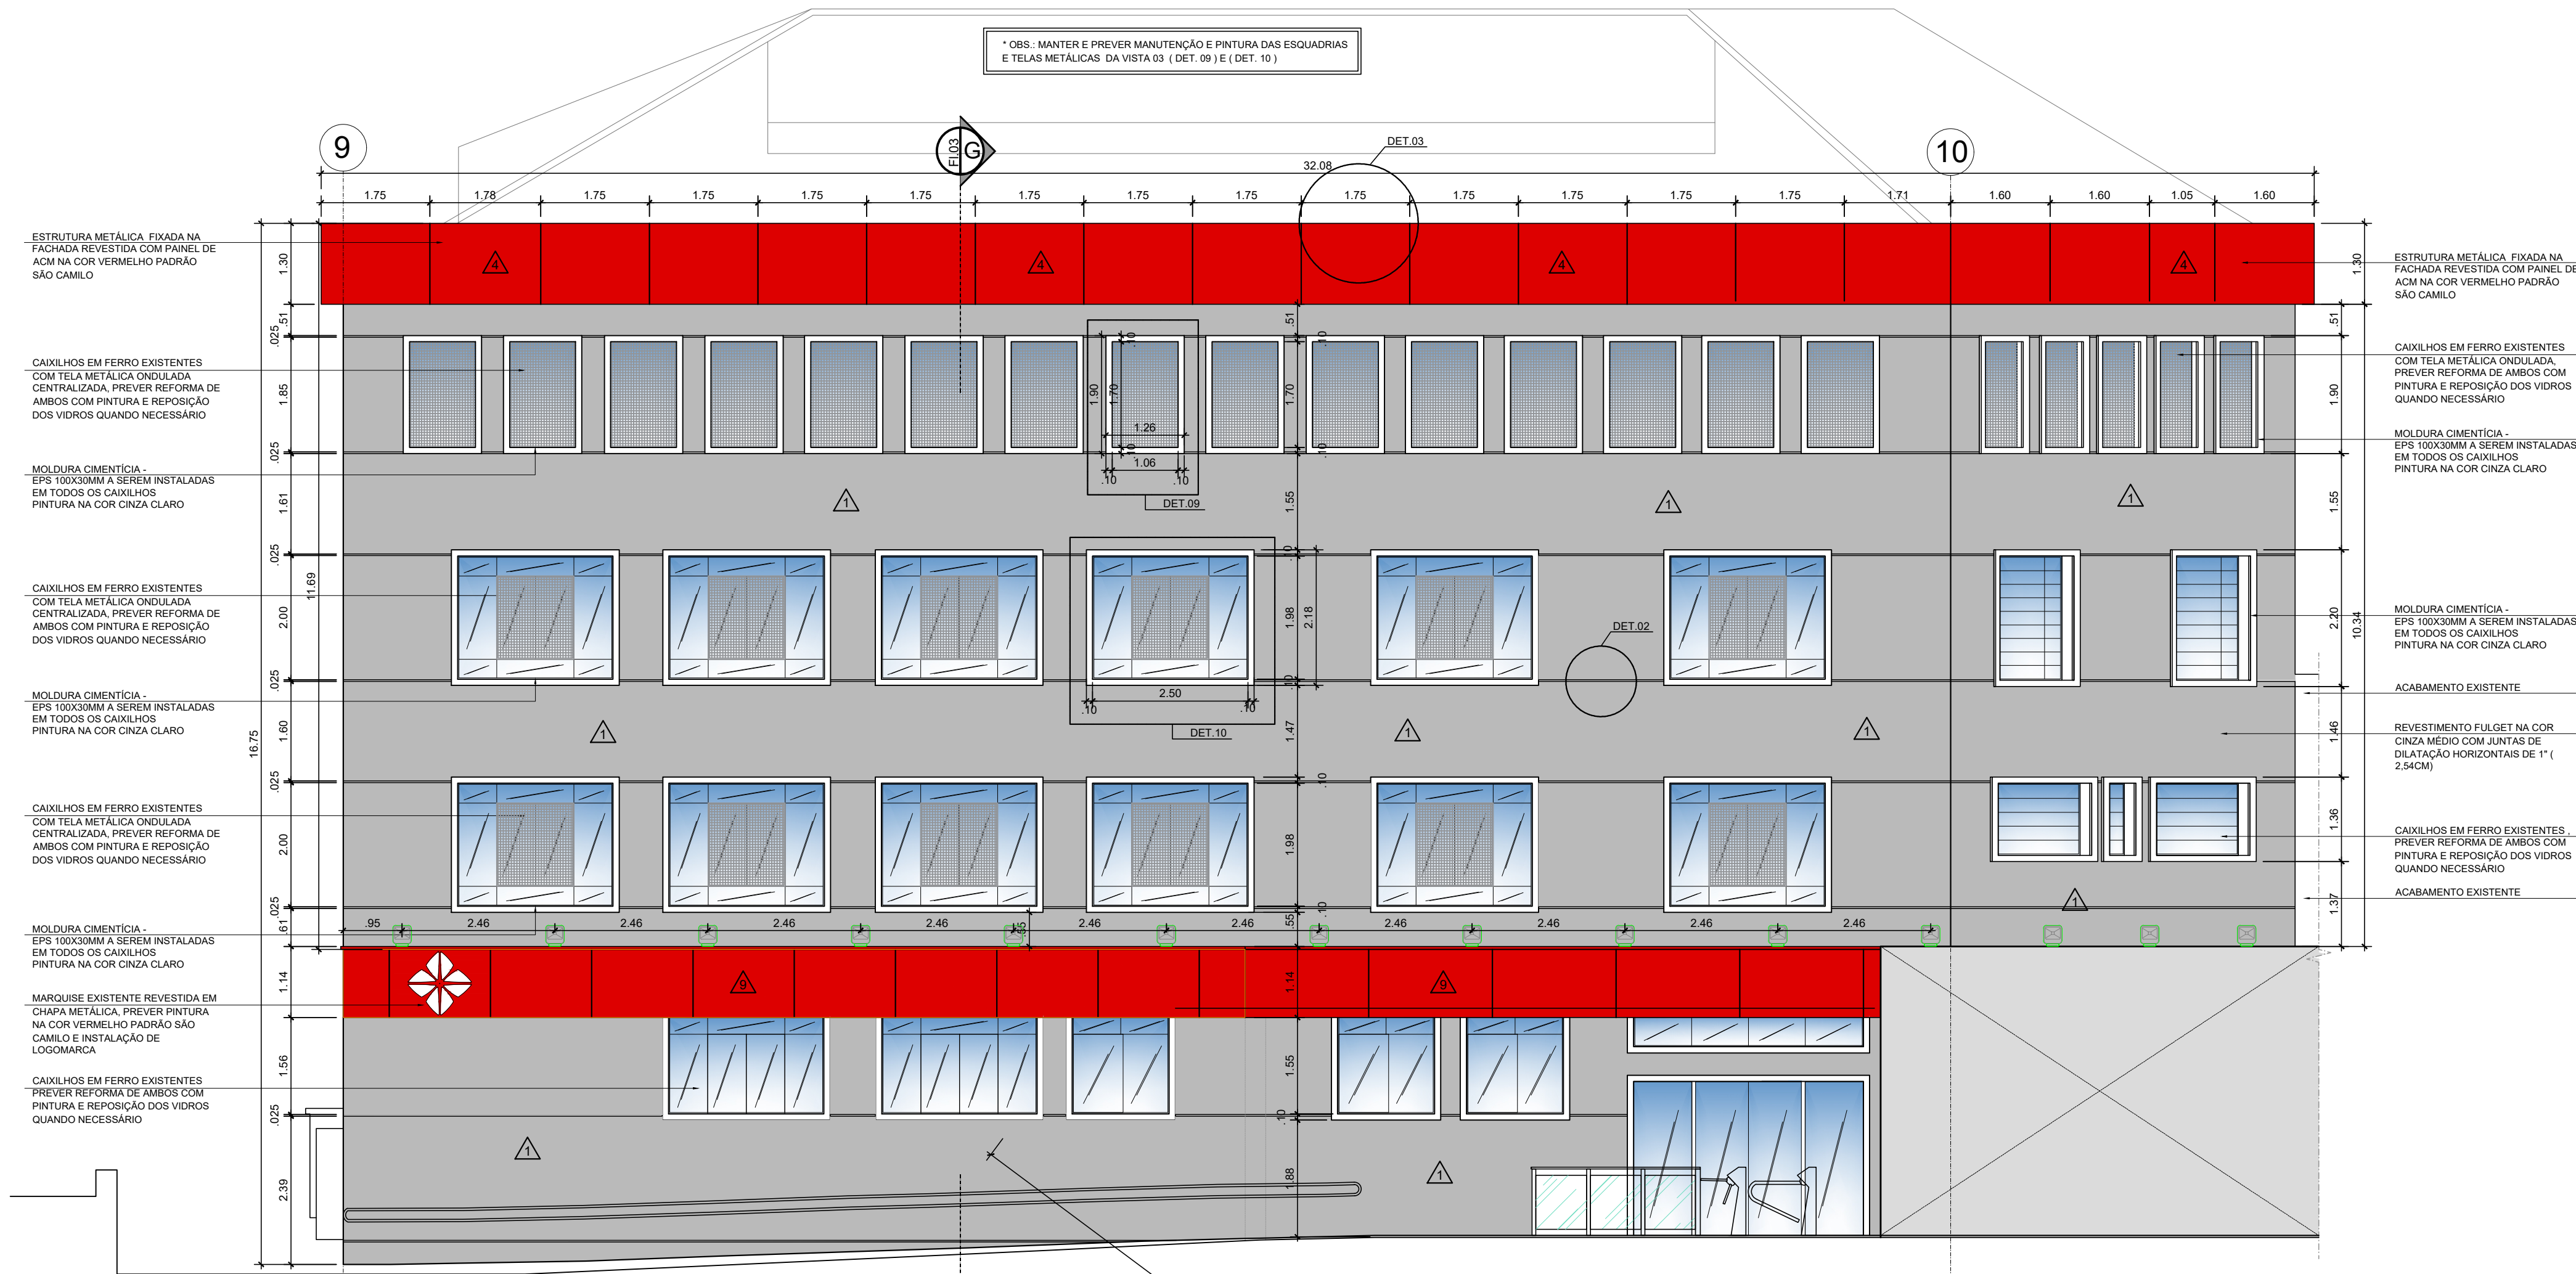


IMPORTANTE:
** NOTA TÉCNICA - PROJETO DE FACHADA, INSTALAÇÃO DE ACM **
A. INSTALAÇÃO DE ACM NA FACHADA DO EDIFÍCIO REQUER A ELABORAÇÃO DE UM PROJETO ESPECÍFICO, QUE CONTEMPLE TODOS OS DETALHES TÉCNICOS E ESTRUTURAIS NECESSÁRIOS PARA GARANTIR A EXECUÇÃO SEGURA, EFICIENTE E ESTETICAMENTE SATISFATORIA DO MATERIAL. O PROJETO DEVERÁ ESPECIFICAR AS CONDIÇÕES DE FIXAÇÃO, INCLUINDO SUPORTES, ANCORAGENS E DETALHES DE ACABAMENTO, RESPEITANDO AS NORMAS DE SEGURANÇA E DESEMPENHO.

LEGENDA DE ACABAMENTOS

PAREDES EXTERNAS	
1	REVESTIMENTO FULGET NA COR CINZA MIO COM JUNTAS DE DILATAÇÃO HORIZONTAIS DE 1" (2,54CM)
2	REVESTIMENTO FULGET NA COR CINZA CLARO COM JUNTAS DE DILATAÇÃO HORIZONTAIS DE 1" (2,54CM)
3	REVESTIMENTO FULGET NA COR VERMELHO
4	ESTRUTURA METÁLICA FIXADA NA FACHADA REVESTIDA COM PAINEL DE ACM NA COR VERMELHO PADRÃO SÃO CAMILO (VIDE PROJETO ESPECÍFICO)
5	ESTRUTURA METÁLICA FIXADA NA FACHADA REVESTIDA COM PAINEL DE ACM NA COR CINZA MIO (VIDE PROJETO ESPECÍFICO)
6	TUOLO DE VIDRO 190X190X6MM ONDULADO INCOLOR, E BARRAS DE AÇO DE 6MM DE DIÂMETRO PARA TRAVAMENTO VERTICAL E HORIZONTAL A INSTALAR
7	TUOLO DE VIDRO 200X200X6MM COM VENTILAÇÃO, INCOLOR E BARRAS DE AÇO DE 6MM DE DIÂMETRO PARA TRAVAMENTO VERTICAL E HORIZONTAL A INSTALAR
8	CERÂMICA 100X100 EXISTENTE A MANTER
9	MARQUISE EXISTENTE REVESTIDA EM CHAPA METÁLICA, PREVER NOVA PINTURA NA COR VERMELHO PADRÃO SÃO CAMILO
10	RECOMPOSIÇÃO EM MASSA COM PINTURA NA COR CINZA MIO

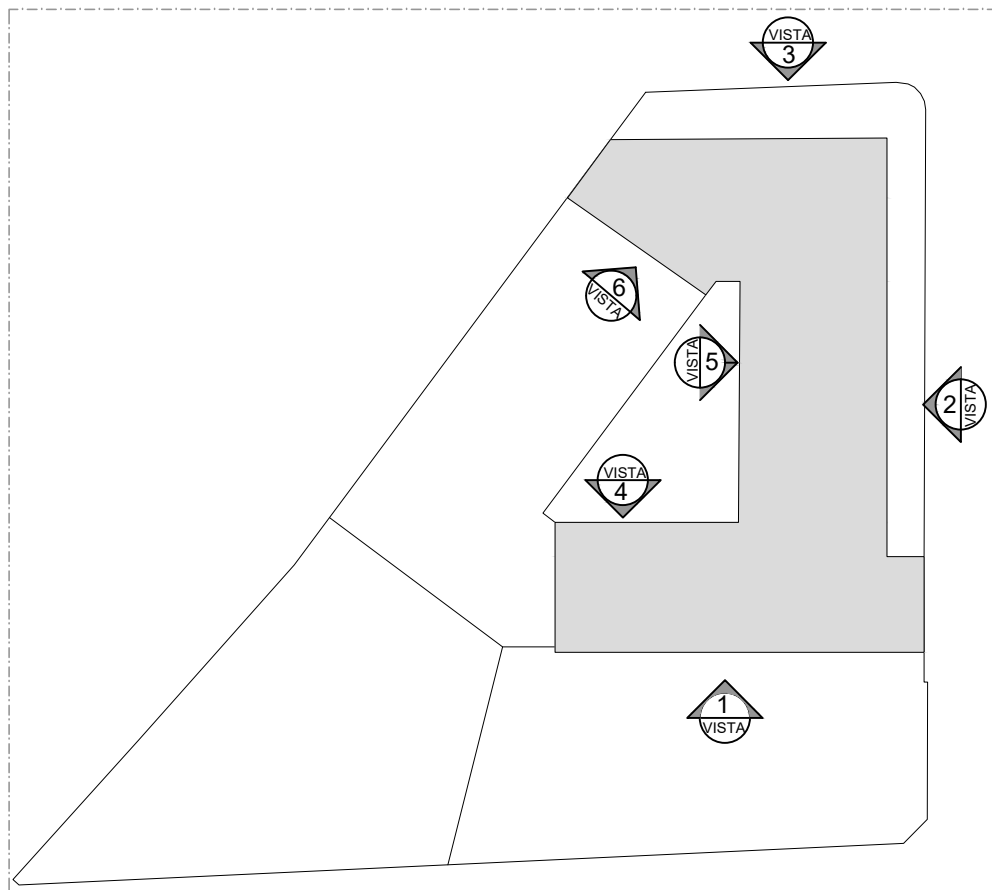

ESCALA: 1:75
VISTA 03
RUA ENG. RANULFO PINHEIRO LIMA
ESCALA: 1:75

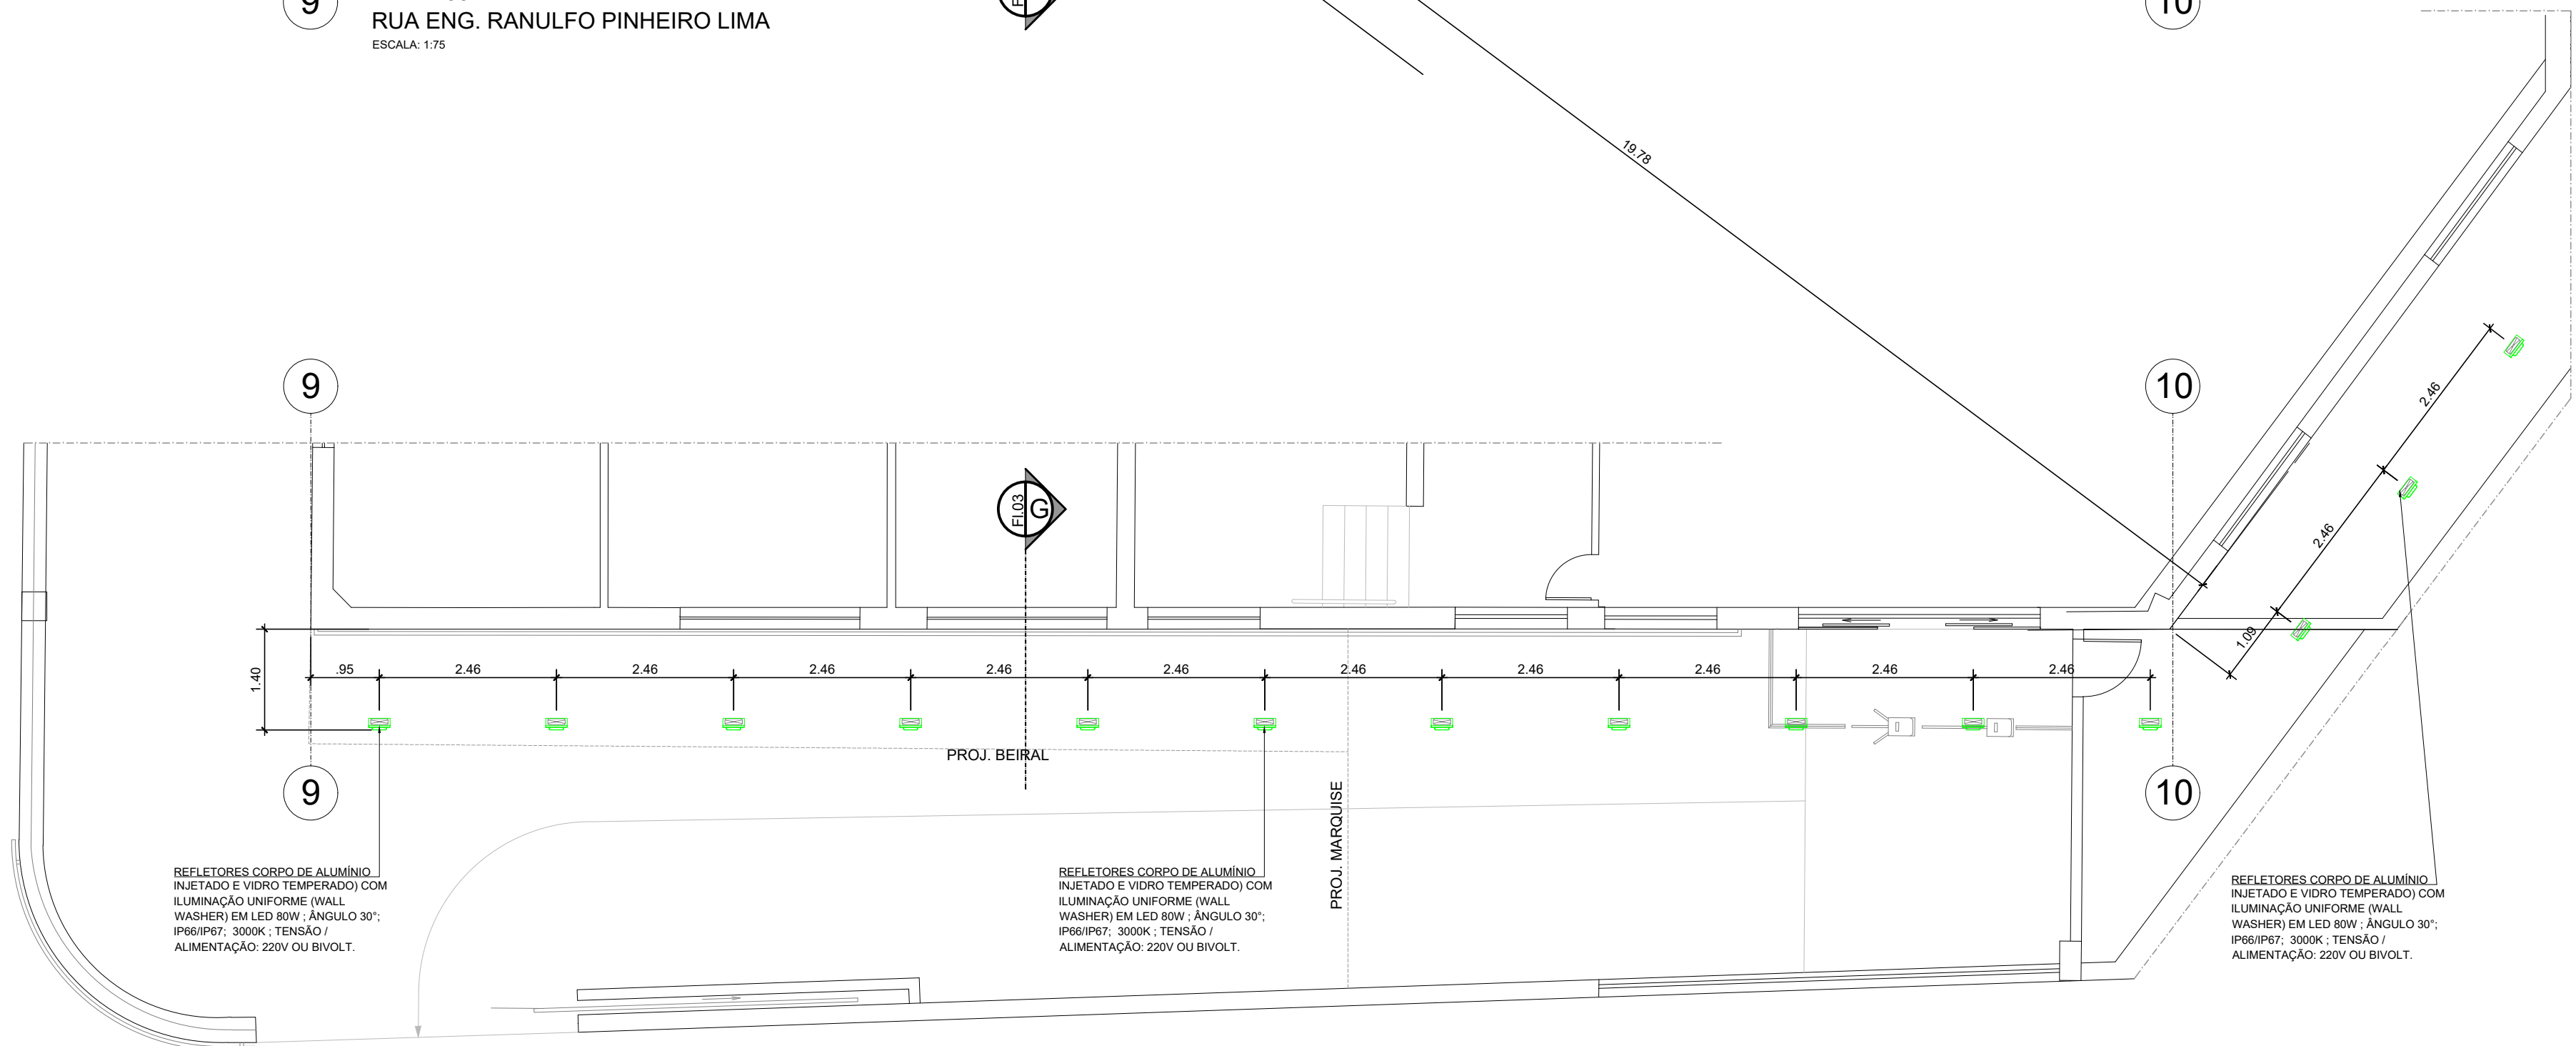

PLANTA PARCIAL
VISTA 03
ESCALA: 1:75

RUA ENGENHEIRO RANULFO PINHEIRO LIMA

02	27.07.26	MUDANÇA NOS FORMATOS CONF. SOLICITAÇÃO DA ENGª DO SÃO CAMILO
01	07.11.24	REVISÃO GERAL CONFORME APOSTAMENTOS
REVISÃO:	DATA:	DESCRIÇÃO:

PROJETISTA:
MP ARQUITETURA
ARQUITETURA & CONSULTORIA

CLIENTE:
**CENTRO UNIVERSITÁRIO
SÃO CAMILO**

PROJETO:
UNIVERSIDADE SÃO CAMILO - UNIDADE IPIRANGA PROMOVE

ASSUNTO:
REFORMA DE FACHADA / EXECUTIVO

PISO/
FACHADA 03- PLANTAS PARCIAIS
RESPONSÁVEL TÉCNICO:
MAURO PEREIRA FILHO
CAU DO RESPONSÁVEL TÉCNICO
A - 7458-6

ESC.:
INDICADA
DATA:
04.05.23


RRT

REVISÃO:


02

FOLHA:

06
12

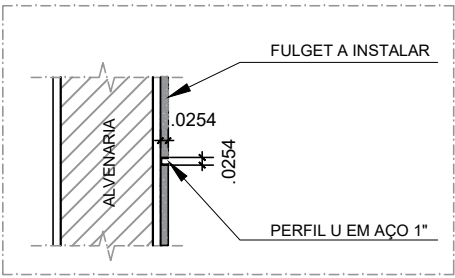

DET. 02
ESCALA 1:25

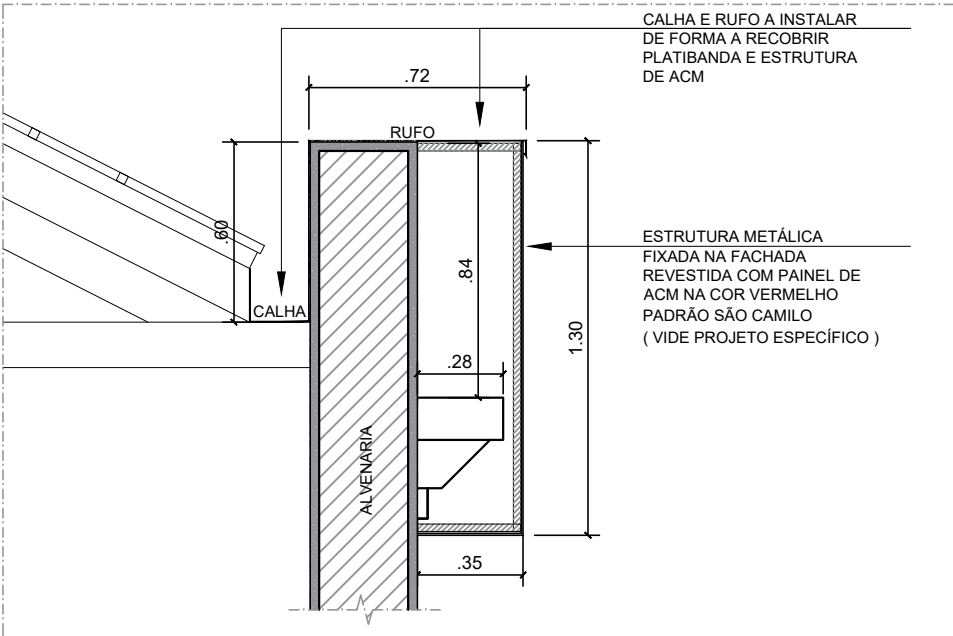



DET. 03-ORIENTATIVO
ESCALA 1:25

LEGENDA DE ACABAMENTOS

△	PAREDES EXTERNAS
1	REVESTIMENTO FULGET NA COR CINZA MÉDIO COM JUNTAS DE DILATAÇÃO HORIZONTAIS DE 1" (2,54CM)
2	REVESTIMENTO FULGET NA COR CINZA CLARO COM JUNTAS DE DILATAÇÃO HORIZONTAIS DE 1" (2,54CM)
3	REVESTIMENTO FULGET NA COR VERMELHO
4	ESTRUTURA METÁLICA FIXADA NA FACHADA REVESTIDA COM PAINEL DE ACM NA COR VERMELHO PADRÃO SÃO CAMILO (VIDE PROJETO ESPECÍFICO)
5	ESTRUTURA METÁLICA FIXADA NA FACHADA REVESTIDA COM PAINEL DE ACM NA CINZA MÉDIO (VIDE PROJETO ESPECÍFICO)
6	TUJOLO DE VIDRO 190X190X80MM ONDULADO INCOLOR, E BARRAS DE AÇO DE 5MM DE DIÂMETRO PARA TRAVAMENTO VERTICAL E HORIZONTAL A INSTALAR
7	TUJOLO DE VIDRO 200X200X60MM COM VENTILAÇÃO, INCOLOR E BARRAS DE AÇO DE 5MM DE DIÂMETRO PARA TRAVAMENTO VERTICAL E HORIZONTAL A INSTALAR
8	CERÂMICA 100X100 EXISTENTE, A MANTER
9	MARQUISE EXISTENTE REVESTIDA EM CHAPA METÁLICA, PREVER NOVA PINTURA NA COR VERMELHO PADRÃO SÃO CAMILO
10	RECOMPOSIÇÃO EM MASSA COM PINTURA NA COR CINZA MÉDIO

IMPORTANTE:

** NOTA TÉCNICA - PROJETO DE FACHADA, INSTALAÇÃO DE ACM **
A INSTALAÇÃO DE ACM NA FACHADA DO EDIFÍCIO REQUER A ELABORAÇÃO DE UM PROJETO ESPECÍFICO, QUE CONTEMPLE TODOS OS DETALHES TÉCNICOS E ESTRUTURAIS NECESSÁRIOS PARA GARANTIR A EXECUÇÃO SEGURA, EFICIENTE E ESTETICAMENTE SATISFATÓRIA DO MATERIAL. O PROJETO DEVERÁ ESPECIFICAR AS CONDIÇÕES DE FIXAÇÃO, INCLUINDO SUPORTES, ANCORAGENS E DETALHES DE ACABAMENTO, RESPEITANDO AS NORMAS DE SEGURANÇA E DESEMPENHO.

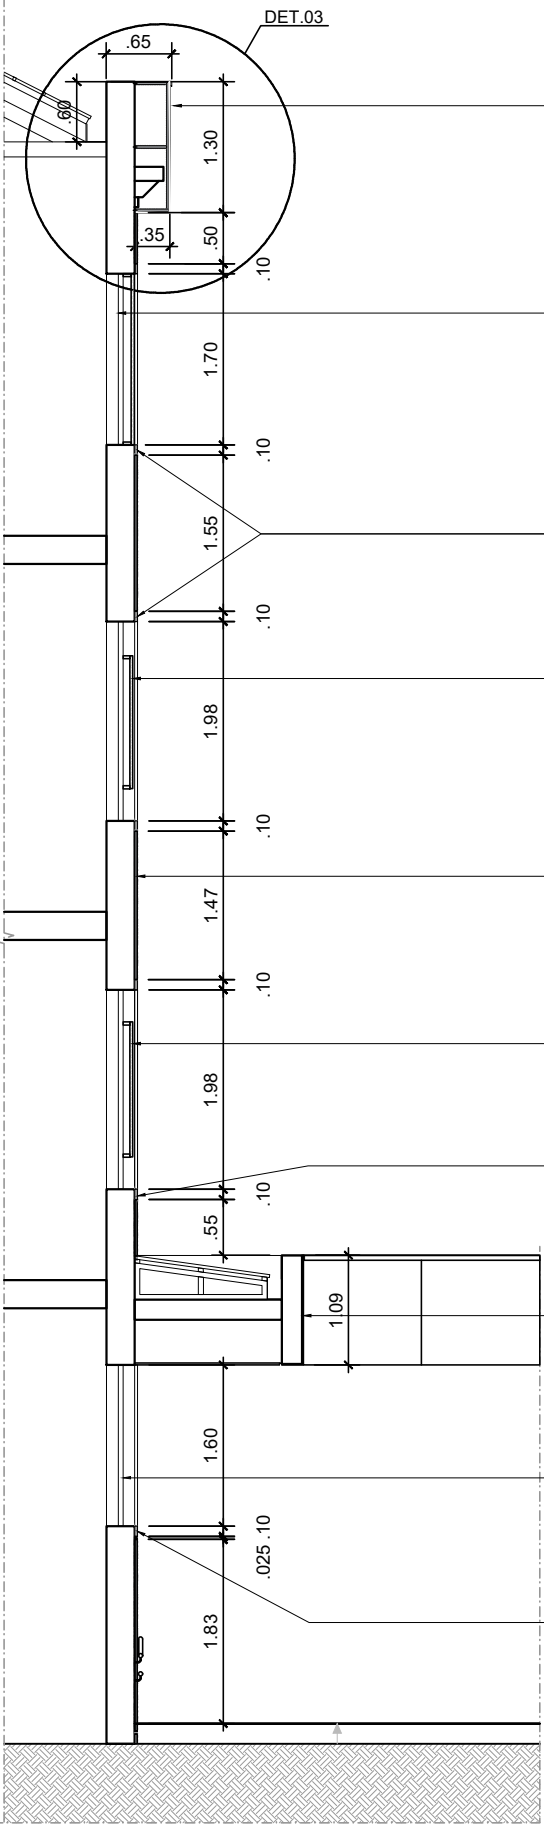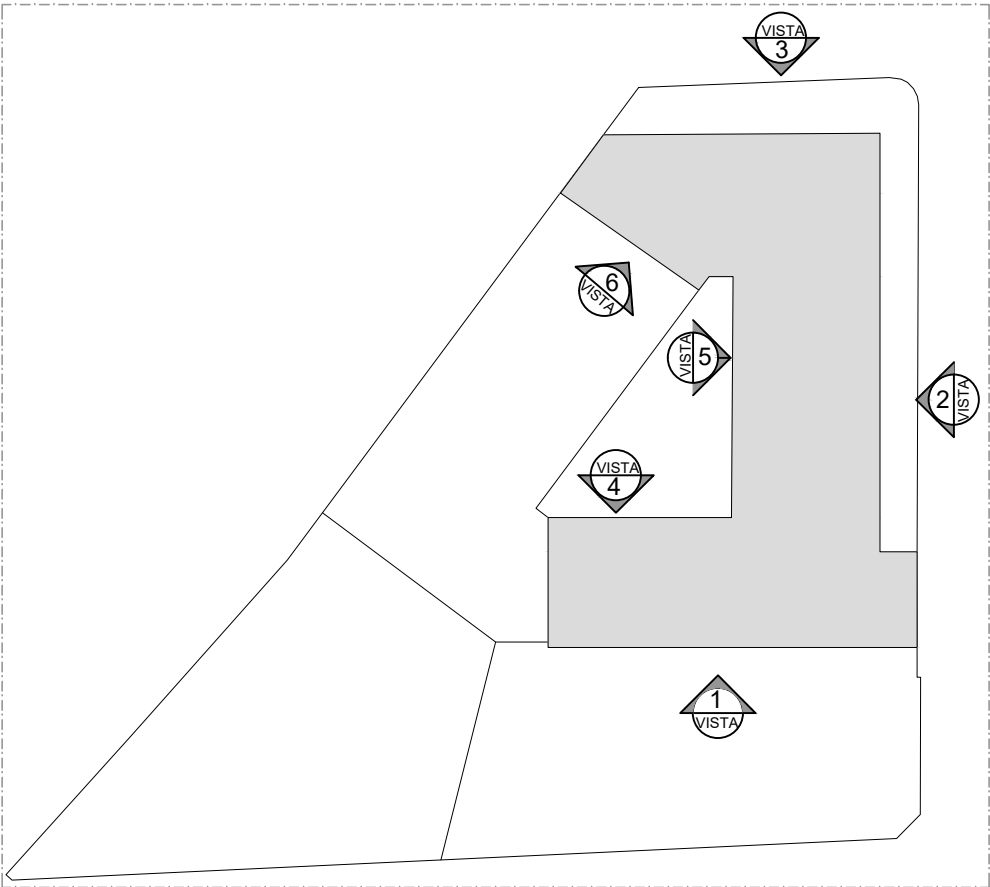

CORTE G - G
ESCALA 1:75

ESTRUTURA METÁLICA
FIXADA NA FACHADA
REVESTIDA COM PAINEL DE
ACM NA COR VERMELHO
PADRÃO
SÃO CAMILO

CAIXILHOS EM FERRO
EXISTENTES COM TELA
METÁLICA ONDULADA
CENTRALIZADA, PREVER
REFORMA DE AMBOS COM
PINTURA E REPOSIÇÃO DOS
VIDROS QUANDO
NECESSÁRIO

MOLDURA CIMENTÍCIA -
EPS 100X30MM A SEREM
INSTALADAS EM TODOS OS
CAIXILHOS
PINTURA NA COR CINZA
CLARO

CAIXILHOS EM FERRO
EXISTENTES COM TELA
METÁLICA ONDULADA
CENTRALIZADA, PREVER
REFORMA DE AMBOS COM
PINTURA E REPOSIÇÃO DOS
VIDROS QUANDO
NECESSÁRIO

REVESTIMENTO FULGET NA COR
CINZA MÉDIO COM JUNTAS DE
DILATAÇÃO HORIZONTAIS DE 1" (2,54CM)


CAIXILHOS EM FERRO
EXISTENTES COM TELA
METÁLICA ONDULADA
CENTRALIZADA, PREVER
REFORMA DE AMBOS COM
PINTURA E REPOSIÇÃO DOS
VIDROS QUANDO
NECESSÁRIO

MOLDURA CIMENTÍCIA -
EPS 100X30MM A SEREM
INSTALADAS EM TODOS OS
CAIXILHOS
PINTURA NA COR CINZA
CLARO


MARQUISE EXISTENTE
REVESTIDA EM CHAPA
METÁLICA, PREVER PINTURA
NA COR VERMELHO PADRÃO
SÃO
CAMILO E INSTALAÇÃO DE
LOGOMARCA

CAIXILHOS EM FERRO
EXISTENTES PREVER
REFORMA DE AMBOS COM
PINTURA E REPOSIÇÃO DOS
VIDROS QUANDO
NECESSÁRIO


MOLDURA CIMENTÍCIA -
EPS 100X30MM A SEREM
INSTALADAS EM TODOS OS
CAIXILHOS
PINTURA NA COR CINZA
CLARO

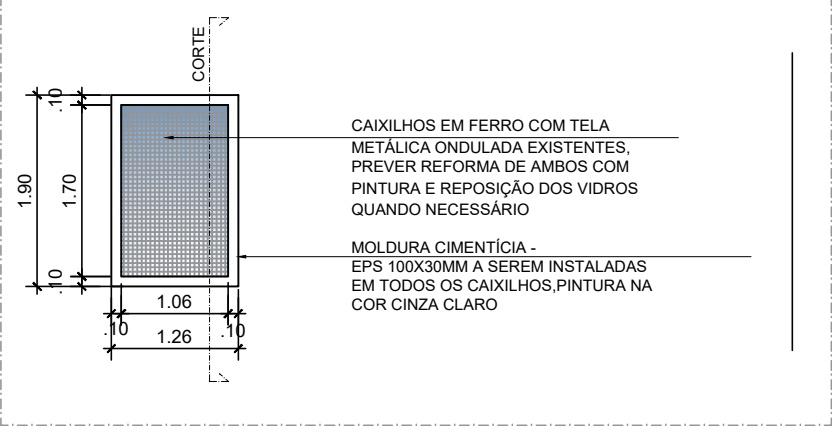


DET. 09
VISTA 3
(COM TELA METÁLICA)
ESCALA 1:75

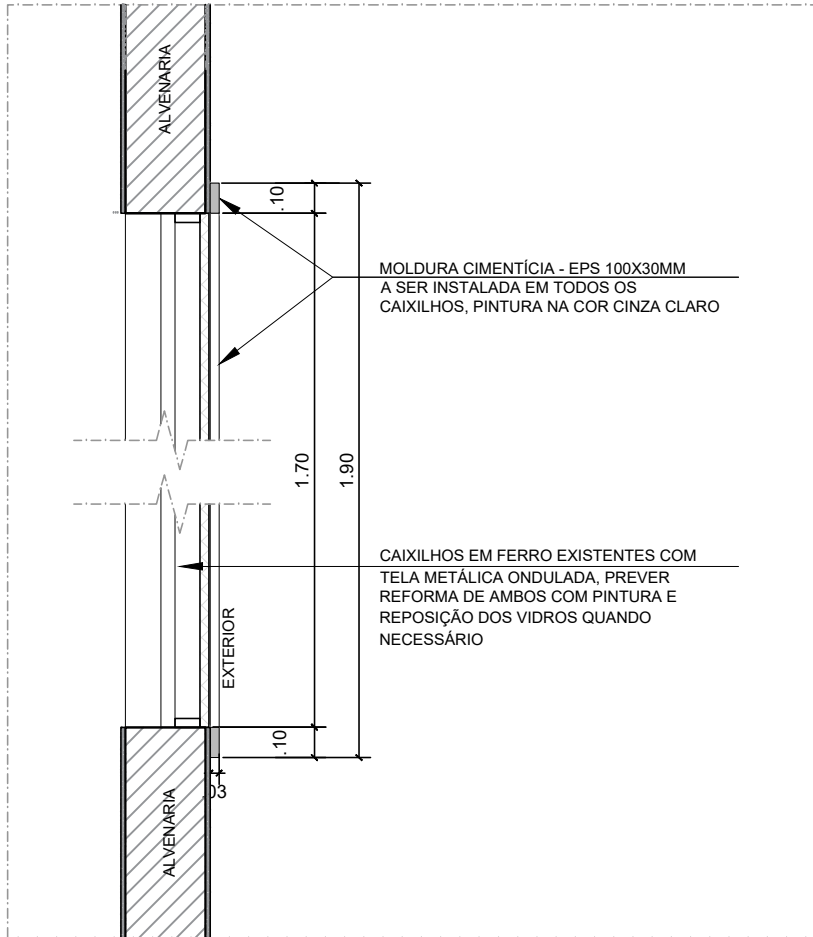


DET. 09
CORTE
(COM TELA METÁLICA)
ESCALA 1:25

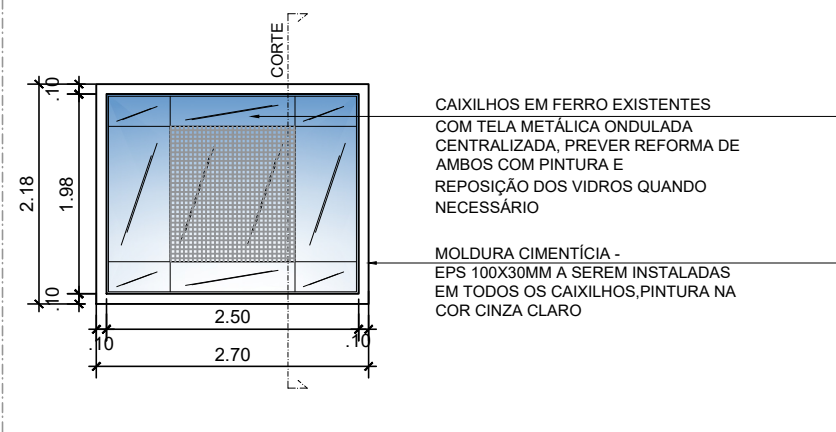

DET. 10
VISTA 3
(COM TELA METÁLICA)
ESCALA 1:75

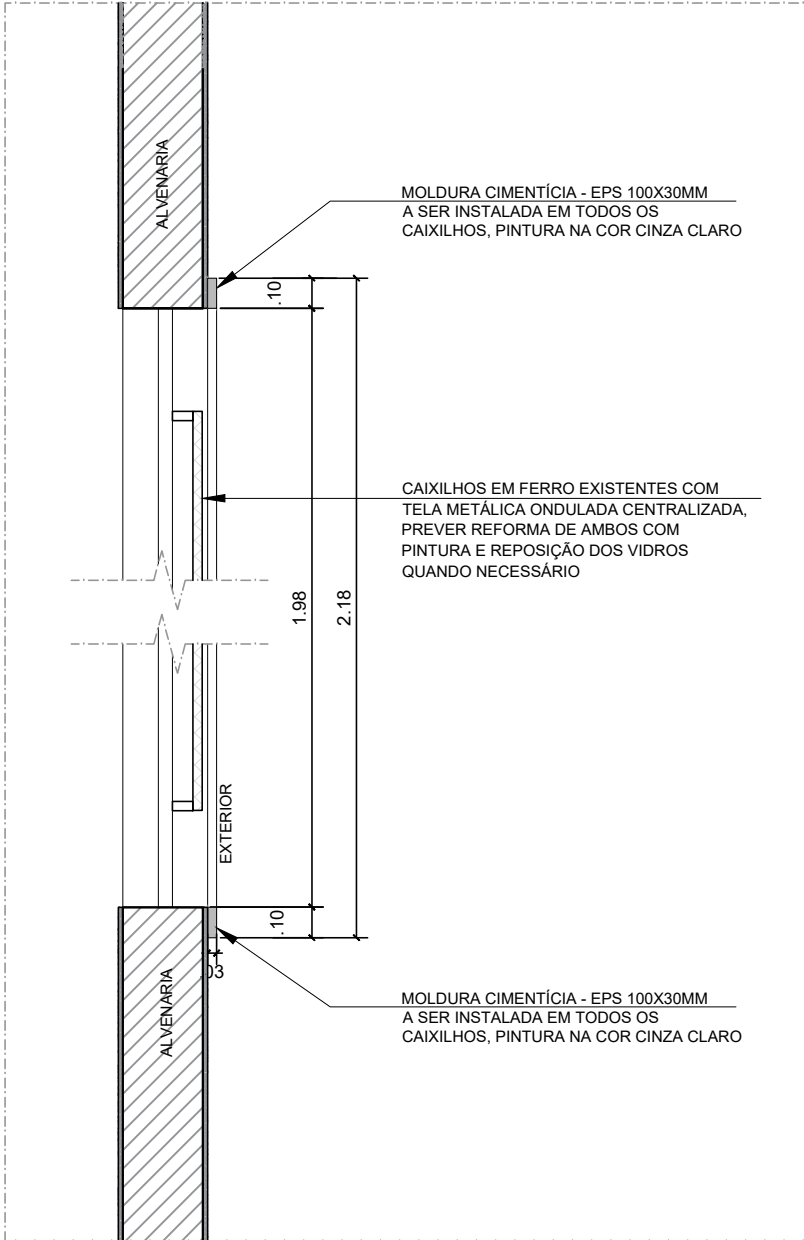

DET. 10
CORTE
(COM TELA METÁLICA)
ESCALA 1:25

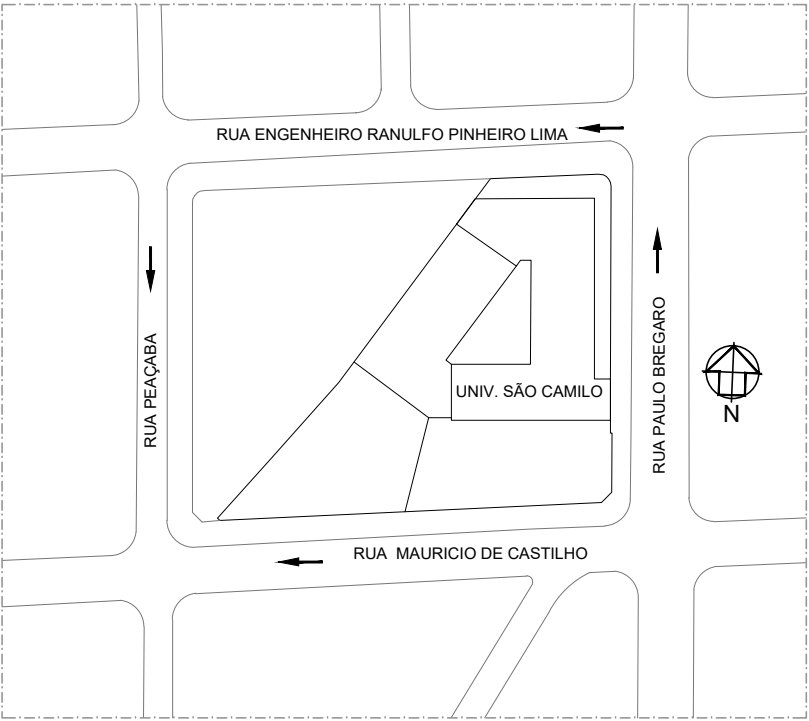

02	27.07.26	MUDANÇA NOS FORMATOS CONF. SOLICITAÇÃO DA ENGª DO SÃO CAMILO
01	07.11.24	REVISÃO GERAL CONFORME APONTAMENTOS
REVISÃO:	DATA:	DESCRIÇÃO:
PROJETISTA:		CLIENTE:
 MP ARQUITETURA ARQUITETURA & CONSULTORIA		 CENTRO UNIVERSITÁRIO SÃO CAMILO
PROJETO:		REVISÃO:
UNIVERSIDADE SÃO CAMILO - UNIDADE IPIRANGA PROMOVE		02
ASSUNTO:		FOLHA:
REFORMA DE FACHADA / EXECUTIVO		
PISO/ FACHADA 03- CORTES E DETALHES	ESC.: INDICADA	
RESPONSÁVEL TÉCNICO: MAURO PEREIRA FILHO	DATA: 04.05.23	
CAU DO RESPONSÁVEL TÉCNICO A - 7458-6	RRT	07 / 12

07
12

△	PARADES EXTERNAS
1	REVESTIMENTO FULGET NA COR CINZA MÉDIO COM JUNTAS DE DILATAÇÃO HORIZONTAIS DE 1" (2,54CM)
2	REVESTIMENTO FULGET NA COR CINZA CLARO COM JUNTAS DE DILATAÇÃO HORIZONTAIS DE 1" (2,54CM)
3	REVESTIMENTO FULGET NA COR VERMELHO
4	ESTRUTURA METÁLICA FIXADA NA FACHADA REVESTIDA COM PAINEL DE ACM NA COR VERMELHO PADRÃO SÃO CAMILO (VIDE PROJETO ESPECÍFICO)
5	ESTRUTURA METÁLICA FIXADA NA FACHADA REVESTIDA COM PAINEL DE ACM NA CINZA MÉDIO (VIDE PROJETO ESPECÍFICO)
6	TUJLO DE VIDRO 190X190X80MM ONDULADO INCOLOR, E BARRAS DE AÇO DE 5MM DE DIÂMETRO PARA TRAVAMENTO VERTICAL E HORIZONTAL.A INSTALAR
7	TUJLO DE VIDRO 200X200X60MM COM VENTILAÇÃO, INCOLOR E BARRAS DE AÇO DE 5MM DE DIÂMETRO PARA TRAVAMENTO VERTICAL E HORIZONTAL.A INSTALAR
8	CERÂMICA 100X100 EXISTENTE,A MANTER
9	MARQUISE EXISTENTE REVESTIDA EM CHAPA METÁLICA, PREVER NOVA PINTURA NA COR VERMELHO PADRÃO SÃO CAMILO
10	RECOMPOSIÇÃO EM MASSA COM PINTURA NA COR CINZA MÉDIO

VISTA 04 INTERNA
ESCALA 1:75

PLANTA PARCIAL VISTA 04
ESCALA 1:75

LEGENDA:

- ESTRUTURA METÁLICA FIXADA NA FACHADA REVESTIDA COM PAINEL DE ACM NA COR VERMELHO PADRÃO SÃO CAMILO
- CAIXILHOS EM FERRO COM VITRAL EXISTENTES, PREVER REFORMA E PINTURA DO CAIXILHO E RESTAURAÇÃO DO VITRAL SE NECESSÁRIO OBS.: DESENHO DO VITRAL NESTE PROJETO É MERAMENTE ILUSTRATIVO
- MOLDURA CIMENTÍCIA - EPS 100X30MM A SEREM INSTALADAS EM TODOS OS CAIXILHOS, PINTURA NA COR CINZA CLARO
- REVESTIMENTO FULGET NA COR CINZA MÉDIO COM JUNTAS DE DILATAÇÃO HORIZONTAIS DE 1" (2,54CM)
- REFLETORES, EXISTENTES PREVER MANUTENÇÃO DOS EQUIPAMENTOS SE NECESSÁRIO
- FECHAMENTO EM VIDRO TEMPERADO EXISTENTE, A SER MANTIDO
- MOLDURA CIMENTÍCIA - EPS 100X30MM A SEREM INSTALADAS EM TODOS OS CAIXILHOS, PINTURA NA COR CINZA CLARO
- REVESTIMENTO CERÂMICO 10X10 EXISTENTE, PREVER RETIRADA E APLICAÇÃO DE FULGET CINZA MÉDIO CONFORME DEMAIS FACHADAS
- ESTRUTURA METÁLICA FIXADA NA FACHADA REVESTIDA COM PAINEL DE ACM NA COR VERMELHO PADRÃO SÃO CAMILO
- CAIXILHOS EM FERRO EXISTENTES COM TELA METÁLICA DE PROTEÇÃO, PREVER REFORMA DE AMBOS COM PINTURA E REPOSIÇÃO DOS VIDROS QUANDO NECESSÁRIO
- ESTRUTURA METÁLICA FIXADA NA FACHADA REVESTIDA COM PAINEL DE ACM NA COR VERMELHO PADRÃO SÃO CAMILO

DETALHES:

- DET.01: DETALHE DO CAIXILHO COM VITRAL E MOLDURA CIMENTÍCIA.
- DET.02: DETALHE DO CAIXILHO COM VITRAL E MOLDURA CIMENTÍCIA.
- DET.03: DETALHE DO CAIXILHO COM VITRAL E MOLDURA CIMENTÍCIA.
- DET.04: DETALHE DO CAIXILHO COM VITRAL E MOLDURA CIMENTÍCIA.
- DET.05: DETALHE DO CAIXILHO COM VITRAL E MOLDURA CIMENTÍCIA.



SEÇÕES:


- SEÇÃO 11: SEÇÃO TRANSVERSAL DA FACHADA.
- SEÇÃO 12: SEÇÃO TRANSVERSAL DA FACHADA.
- SEÇÃO 13: SEÇÃO TRANSVERSAL DA FACHADA.
- SEÇÃO 14: SEÇÃO TRANSVERSAL DA FACHADA.
- SEÇÃO 15: SEÇÃO TRANSVERSAL DA FACHADA.


PLANTA PARCIAL VISTA 04:

- PÁTIO COBERTO
- PÁTIO DESCOBERTO
- FLOREIRA
- PROJ. COB.


**** NOTA TÉCNICA - PROJETO DE FACHADA, INSTALAÇÃO DE ACM ****
A INSTALAÇÃO DE ACM NA FACHADA DO EDIFÍCIO REQUER A ELABORAÇÃO DE UM PROJETO ESPECÍFICO, QUE CONTEMPLE TODOS OS DETALHES TÉCNICOS E ESTRUTURAIS NECESSÁRIOS PARA GARANTIR A EXECUÇÃO SEGURA, EFICIENTE E ESTETICAMENTE SATISFATÓRIA DO MATERIAL. O PROJETO DEVERÁ ESPECIFICAR AS CONDIÇÕES DE FIXAÇÃO, INCLUINDO SUPORTES, ANCORAGENS E DETALHES DE ACABAMENTO, RESPEITANDO AS NORMAS DE SEGURANÇA E DESEMPENHO.

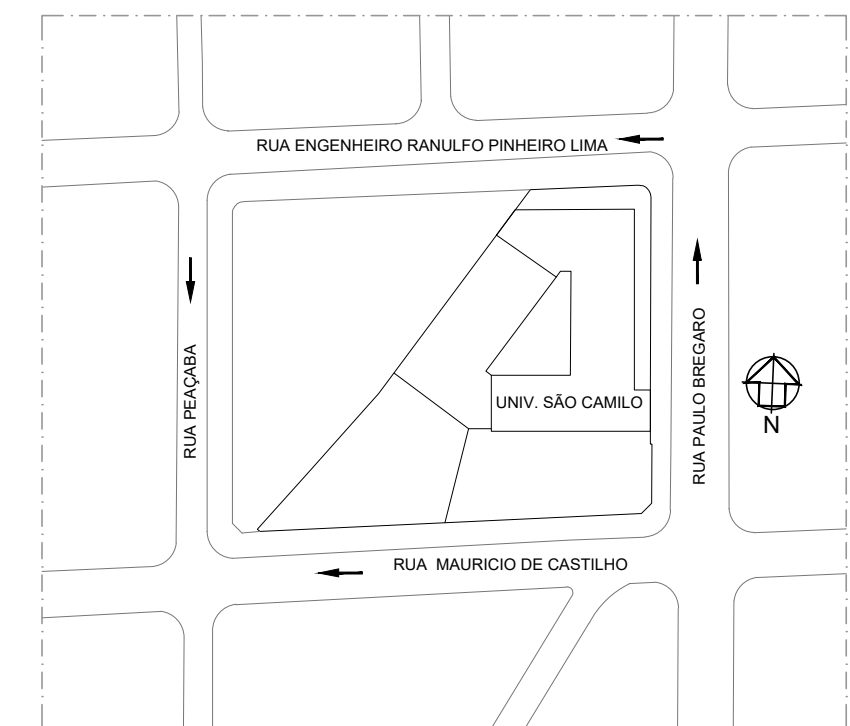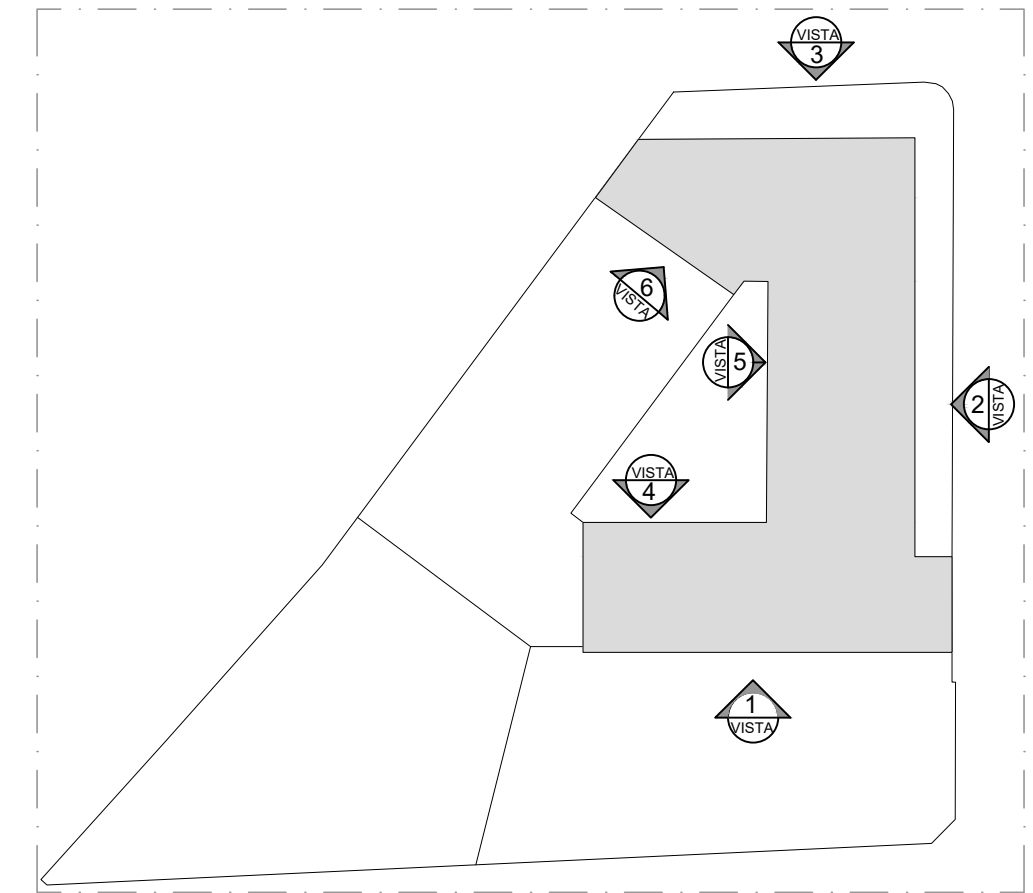

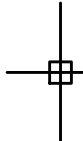
02	27.07.26	MUDANÇA NOS FORMATOS CONF. SOLICITAÇÃO DA ENGª DO SÃO CAMILO
01	07.11.24	REVISÃO GERAL CONFORME APONTAMENTOS
REVISÃO:	DATA:	DESCRIÇÃO:
PROJETISTA:  MP ARQUITETURA ARQUITETURA & CONSULTORIA		CLIENTE:  CENTRO UNIVERSITÁRIO SÃO CAMILO
PROJETO: UNIVERSIDADE SÃO CAMILO - UNIDADE IPIRANGA PROMOVE		REVISÃO: 02
ASSUNTO: REFORMA DE FACHADA / EXECUTIVO		
PISO/ FACHADA 04- PLANTA PARCIAL		FOLHA: 08 / 12
RESPONSÁVEL TÉCNICO: MAURO PEREIRA FILHO		
CAU DO RESPONSÁVEL TÉCNICO A - 7458-6		
		ESC.: INDICADA
		DATA: 04.05.23

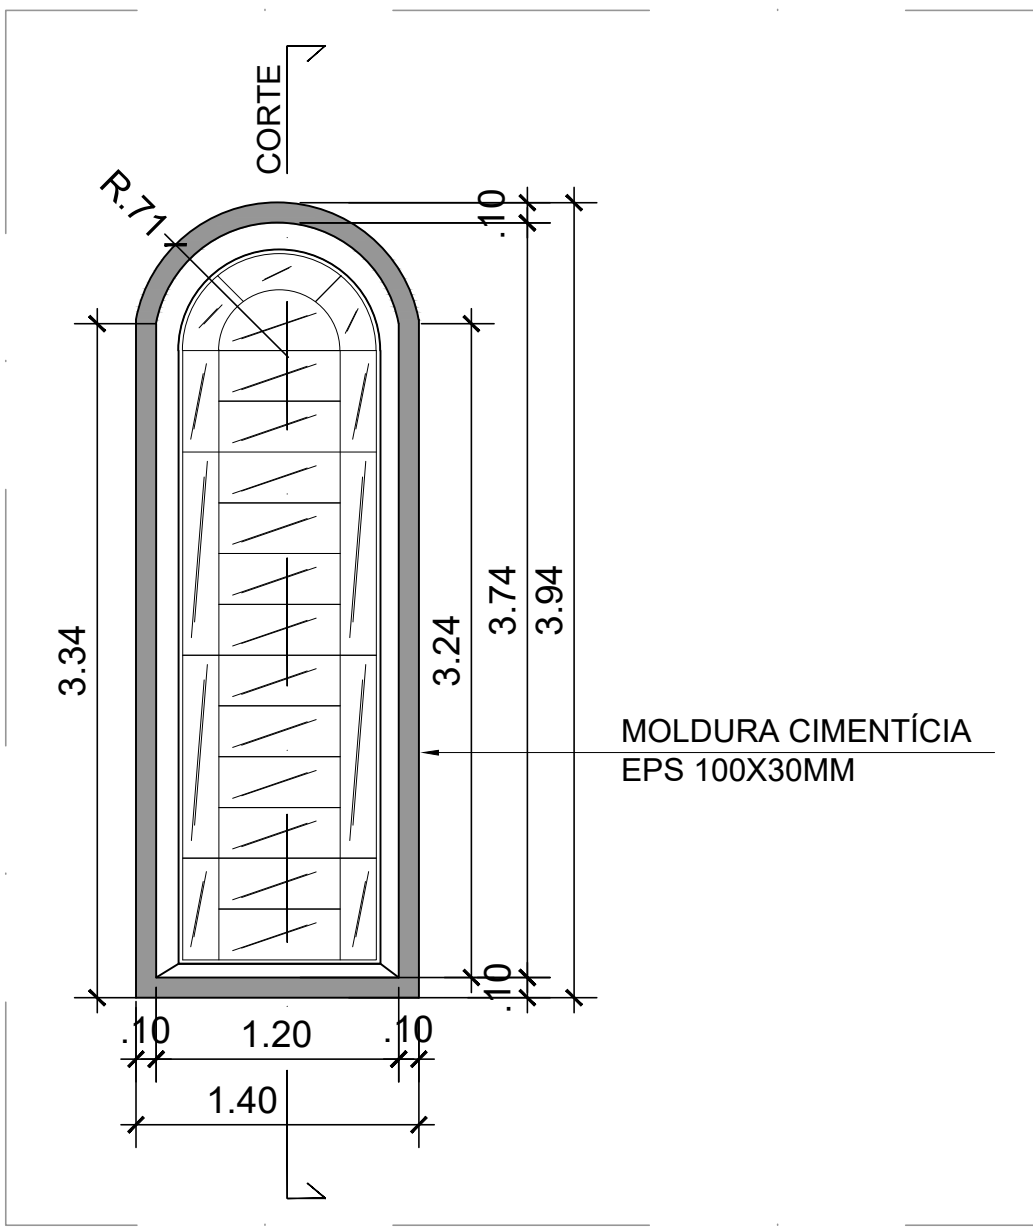

DET. 01
VISTA 4
(SEM TELA METÁLICA)
ESCALA 1:75

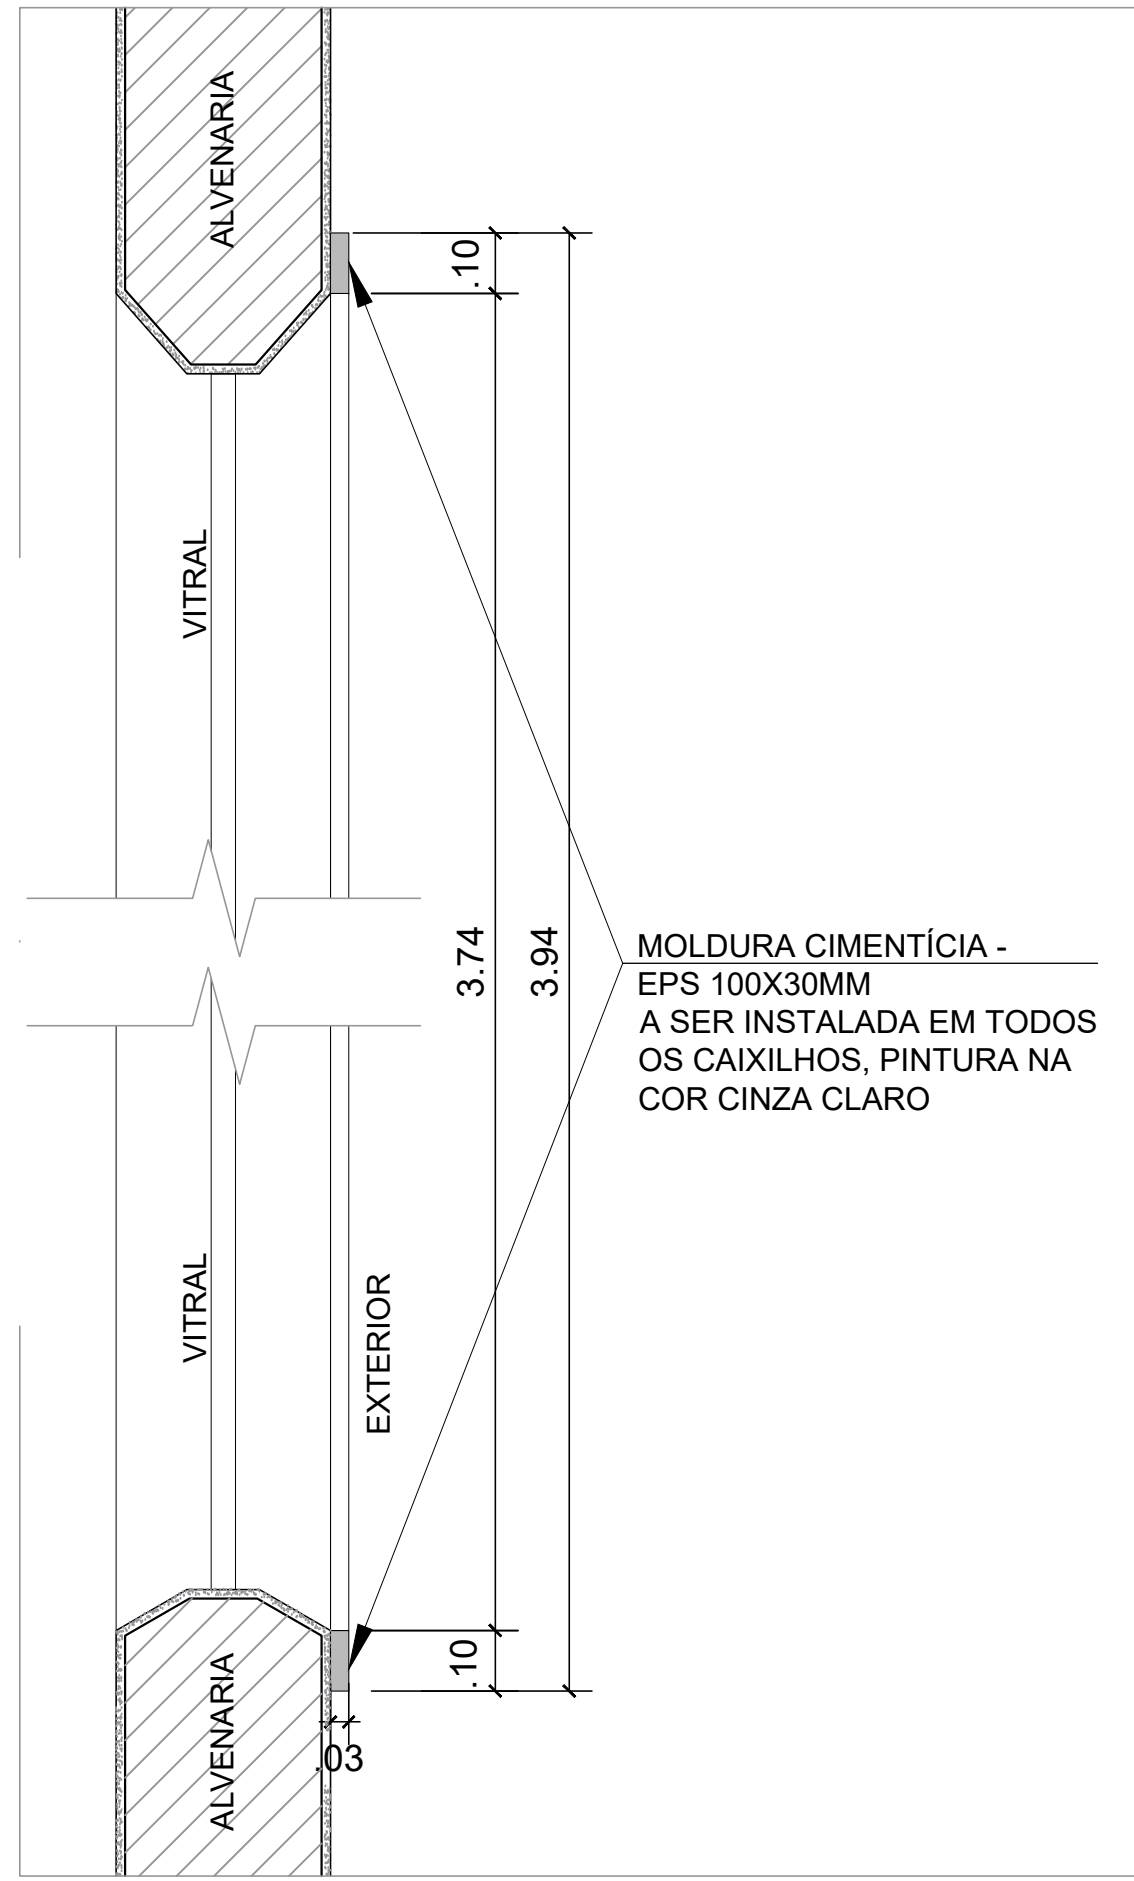

DET. 01
CORTE
(SEM TELA METÁLICA)
ESCALA 1:25

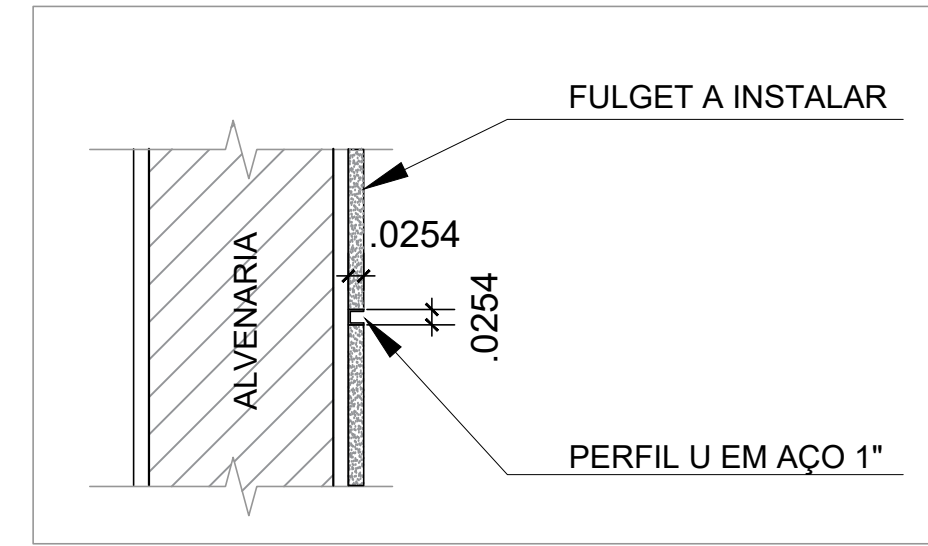

DET. 02
ESCALA 1:25



LEGENDA DE ACABAMENTOS

△	PAREDES EXTERNAS
1	REVESTIMENTO FULGET NA COR CINZA MÉDIO COM JUNTAS DE DILATAÇÃO HORIZONTAIS DE 1" (2,54CM)
2	REVESTIMENTO FULGET NA COR CINZA CLARO COM JUNTAS DE DILATAÇÃO HORIZONTAIS DE 1" (2,54CM)
3	REVESTIMENTO FULGET NA COR VERMELHO
4	ESTRUTURA METÁLICA FIXADA NA FACHADA REVESTIDA COM PAINEL DE ACM NA COR VERMELHO PADRÃO SÃO CAMILO (VIDE PROJETO ESPECÍFICO)
5	ESTRUTURA METÁLICA FIXADA NA FACHADA REVESTIDA COM PAINEL DE ACM NA CINZA MÉDIO (VIDE PROJETO ESPECÍFICO)
6	TUJOLO DE VIDRO 190X190X80MM ONDULADO INCOLOR, E BARRAS DE AÇO DE 5MM DE DIÂMETRO PARA TRAVAMENTO VERTICAL E HORIZONTAL A INSTALAR
7	TUJOLO DE VIDRO 200X200X60MM COM VENTILAÇÃO, INCOLOR E BARRAS DE AÇO DE 5MM DE DIÂMETRO PARA TRAVAMENTO VERTICAL E HORIZONTAL A INSTALAR
8	CERÂMICA 100X100 EXISTENTE, A MANTER
9	MARQUISE EXISTENTE REVESTIDA EM CHAPA METÁLICA, PREVER NOVA PINTURA NA COR VERMELHO PADRÃO SÃO CAMILO
10	RECOMPOSIÇÃO EM MASSA COM PINTURA NA COR CINZA MÉDIO


IMPORTANTE:

** NOTA TÉCNICA - PROJETO DE FACHADA. INSTALAÇÃO DE ACM **


A INSTALAÇÃO DE ACM NA FACHADA DO EDIFÍCIO REQUER A ELABORAÇÃO DE UM PROJETO ESPECÍFICO, QUE CONTEMPLE TODOS OS DETALHES TÉCNICOS E ESTRUTURAIS NECESSÁRIOS PARA GARANTIR A EXECUÇÃO SEGURA, EFICIENTE E ESTETICAMENTE SATISFATÓRIA DO MATERIAL. O PROJETO DEVERÁ ESPECIFICAR AS CONDIÇÕES DE FIXAÇÃO, INCLUINDO SUPORTES, ANCORAGENS E DETALHES DE ACABAMENTO, RESPEITANDO AS NORMAS DE SEGURANÇA E DESEMPENHO.

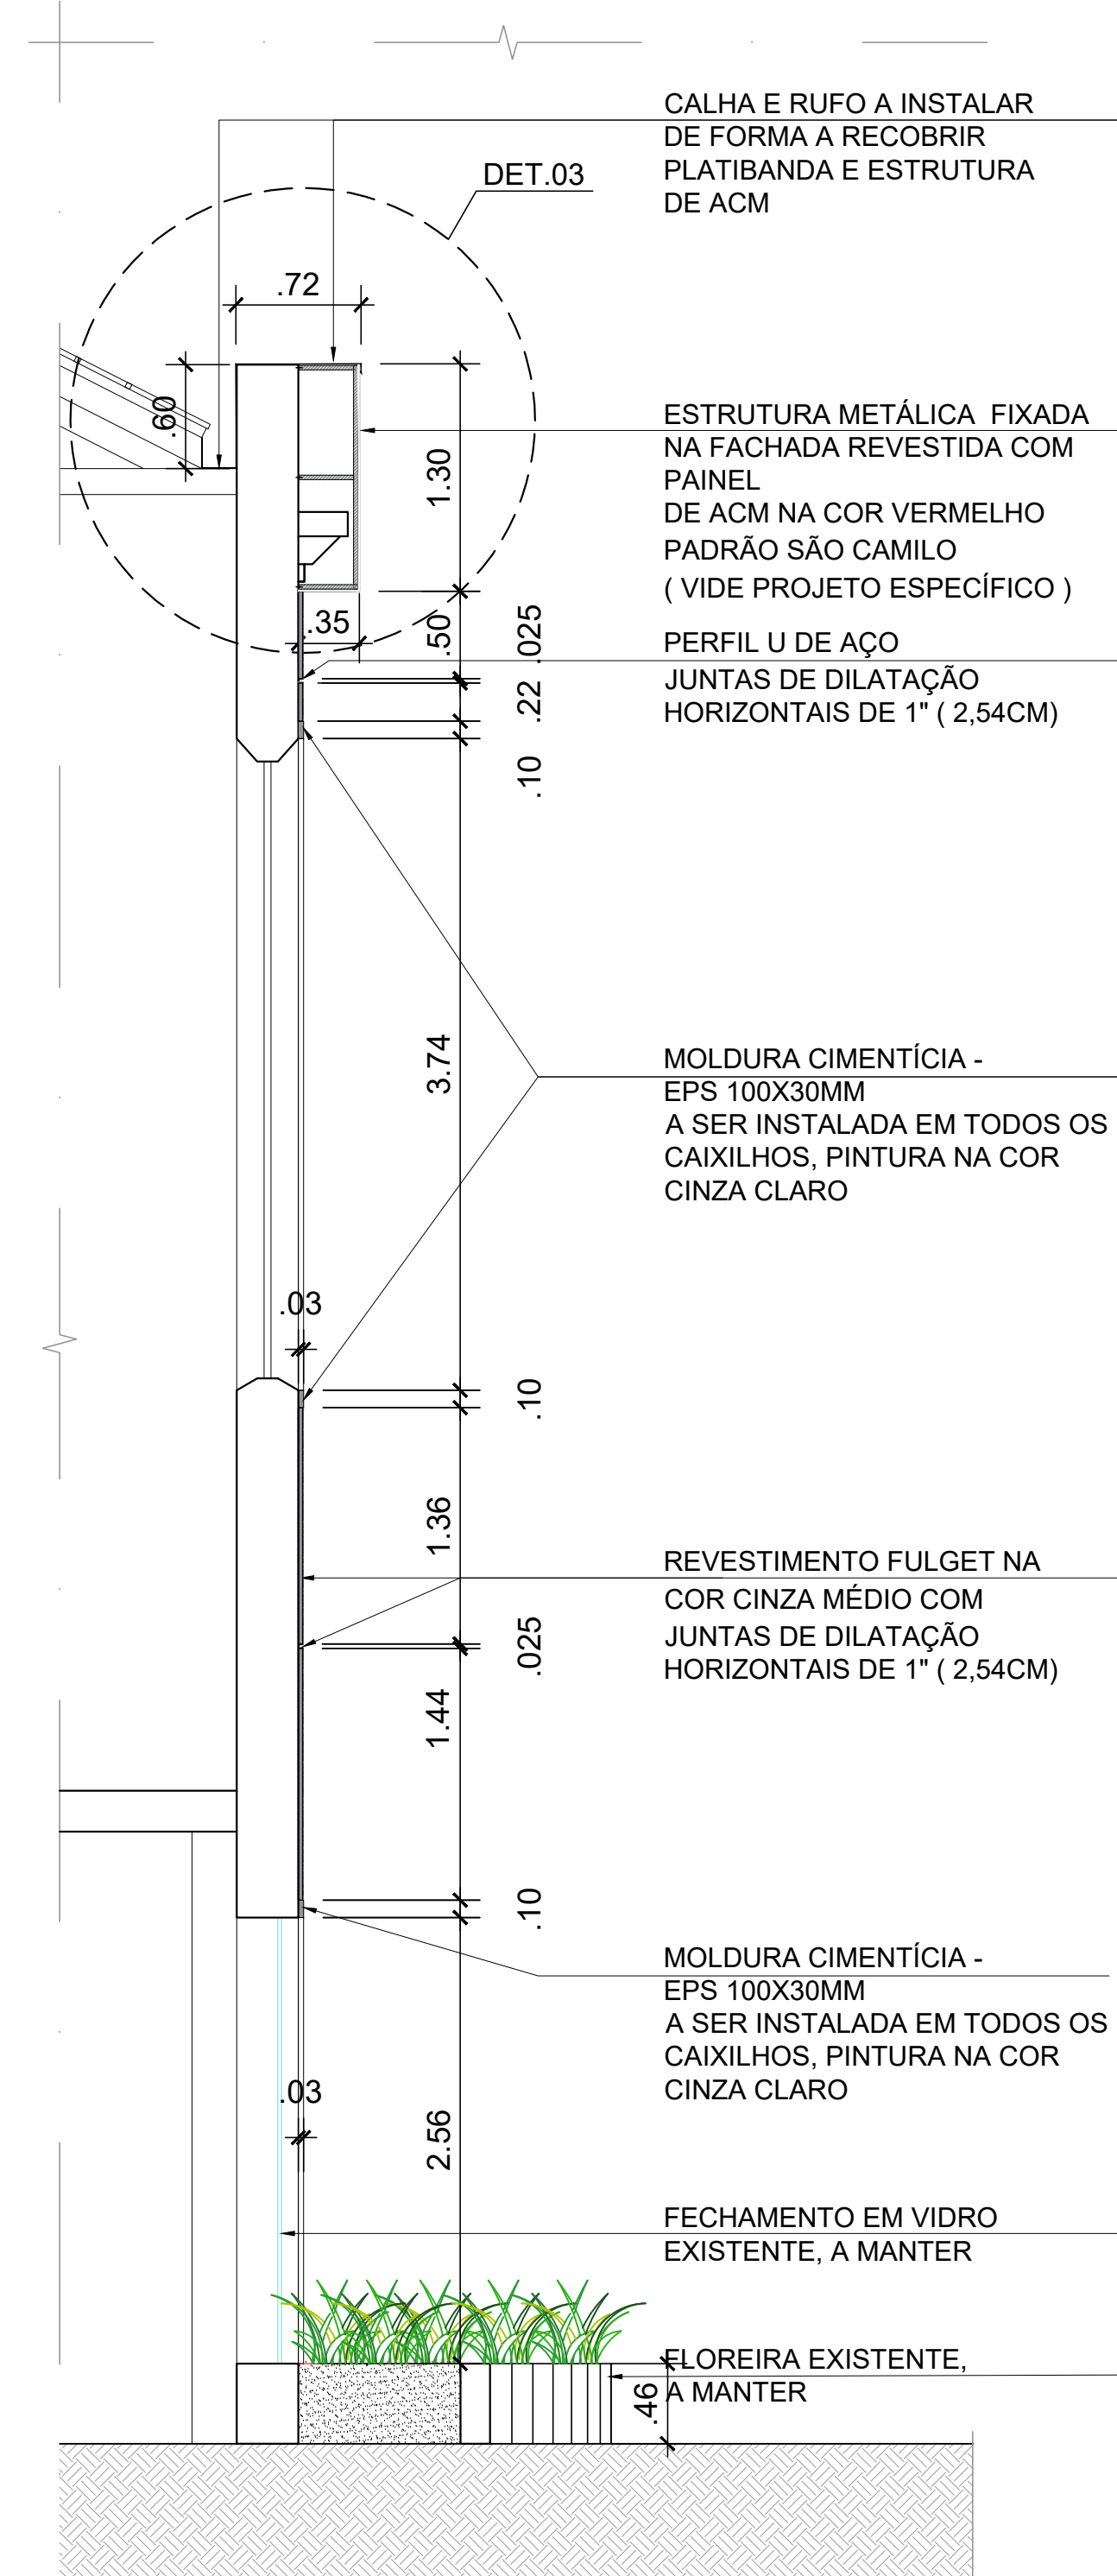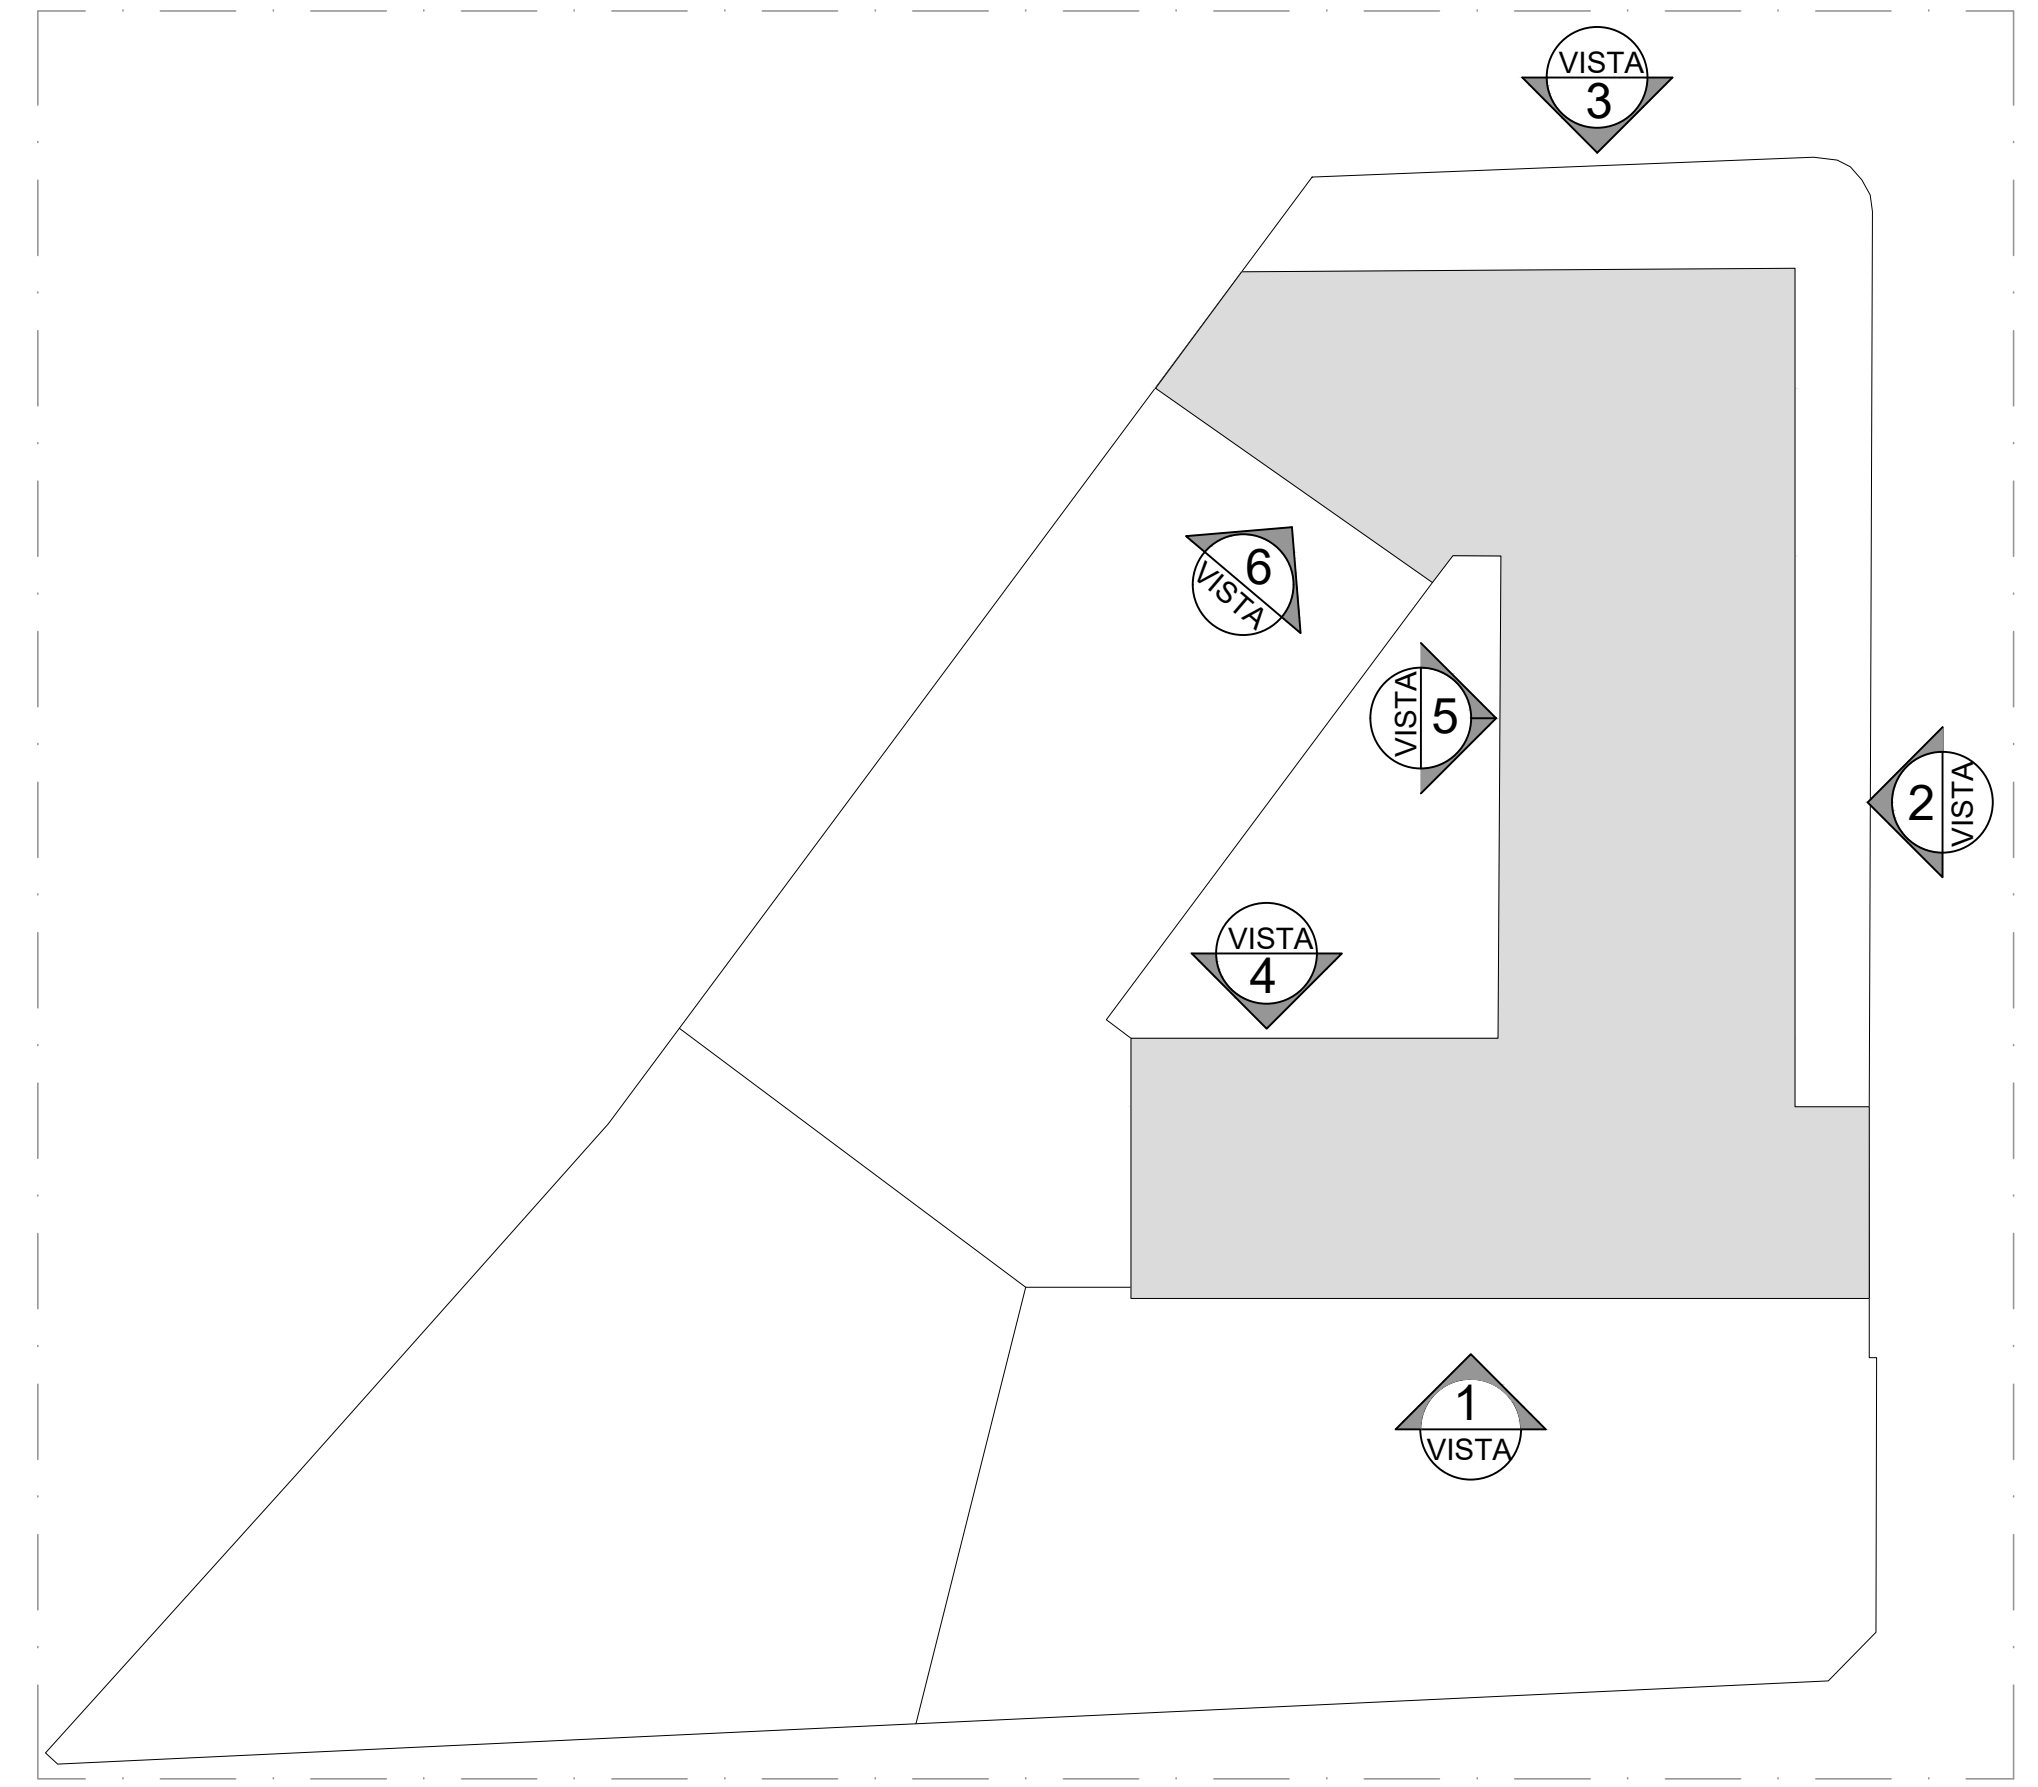


CORTE H-H
ESCALA 1:75

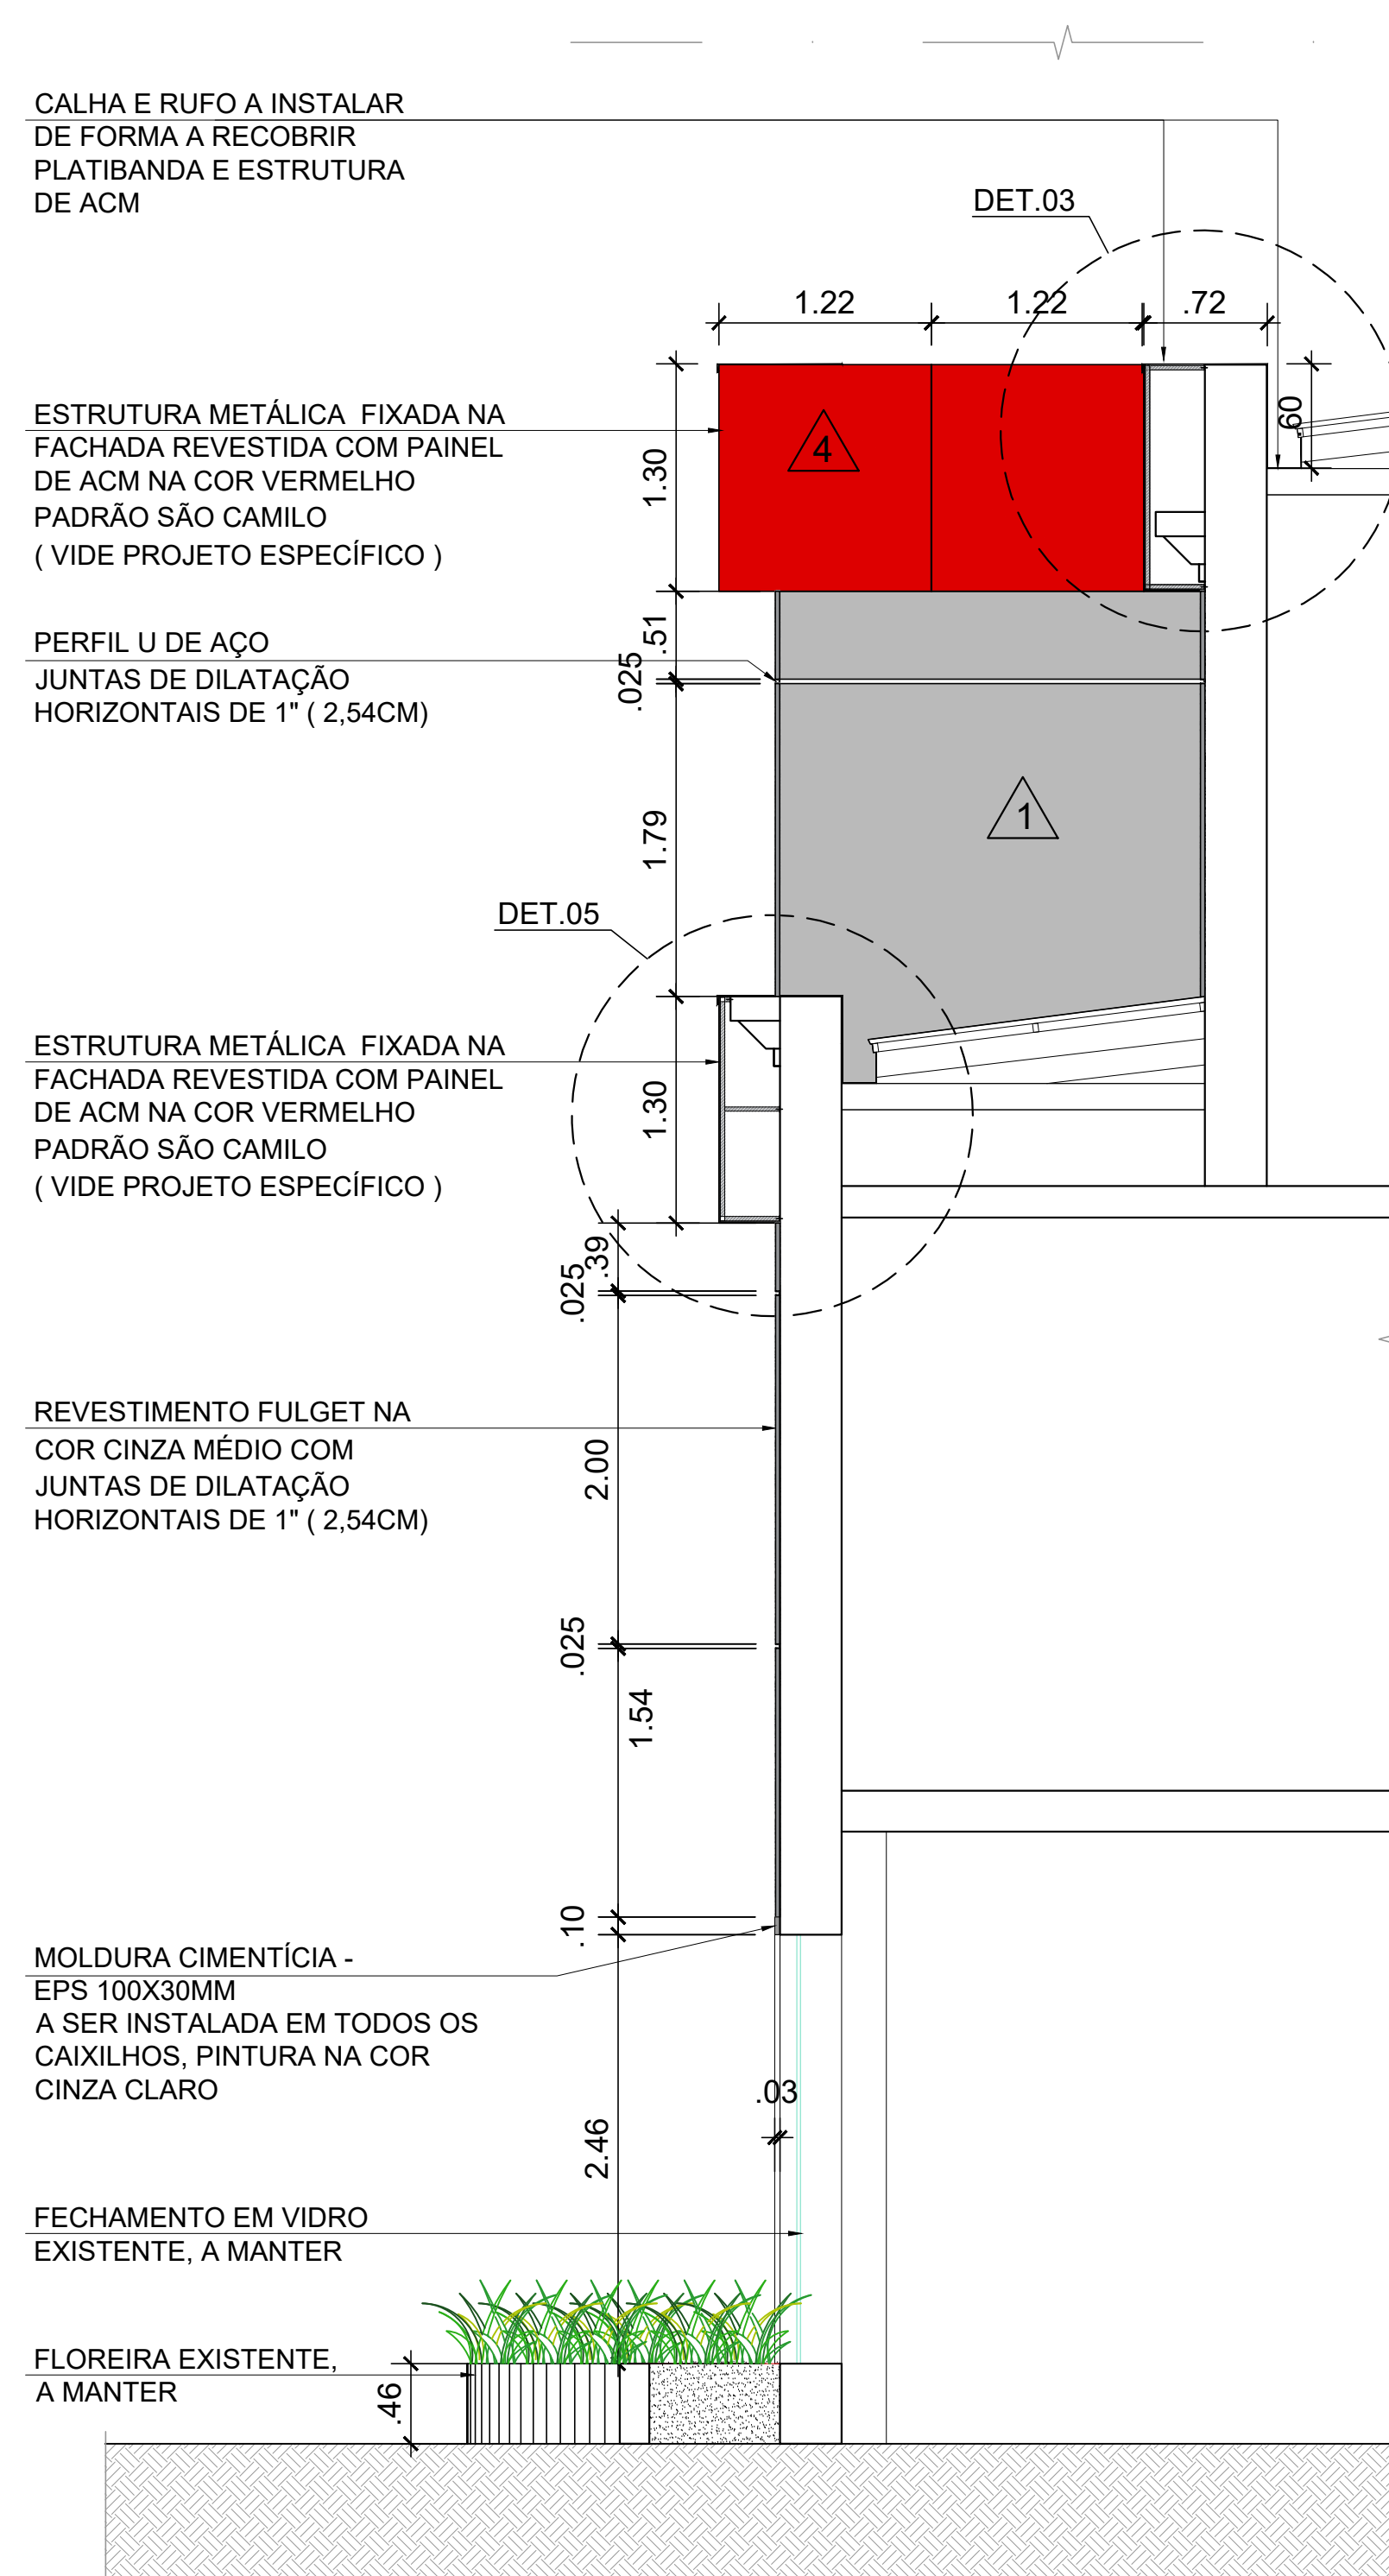


CORTE I-I
ESCALA 1:75


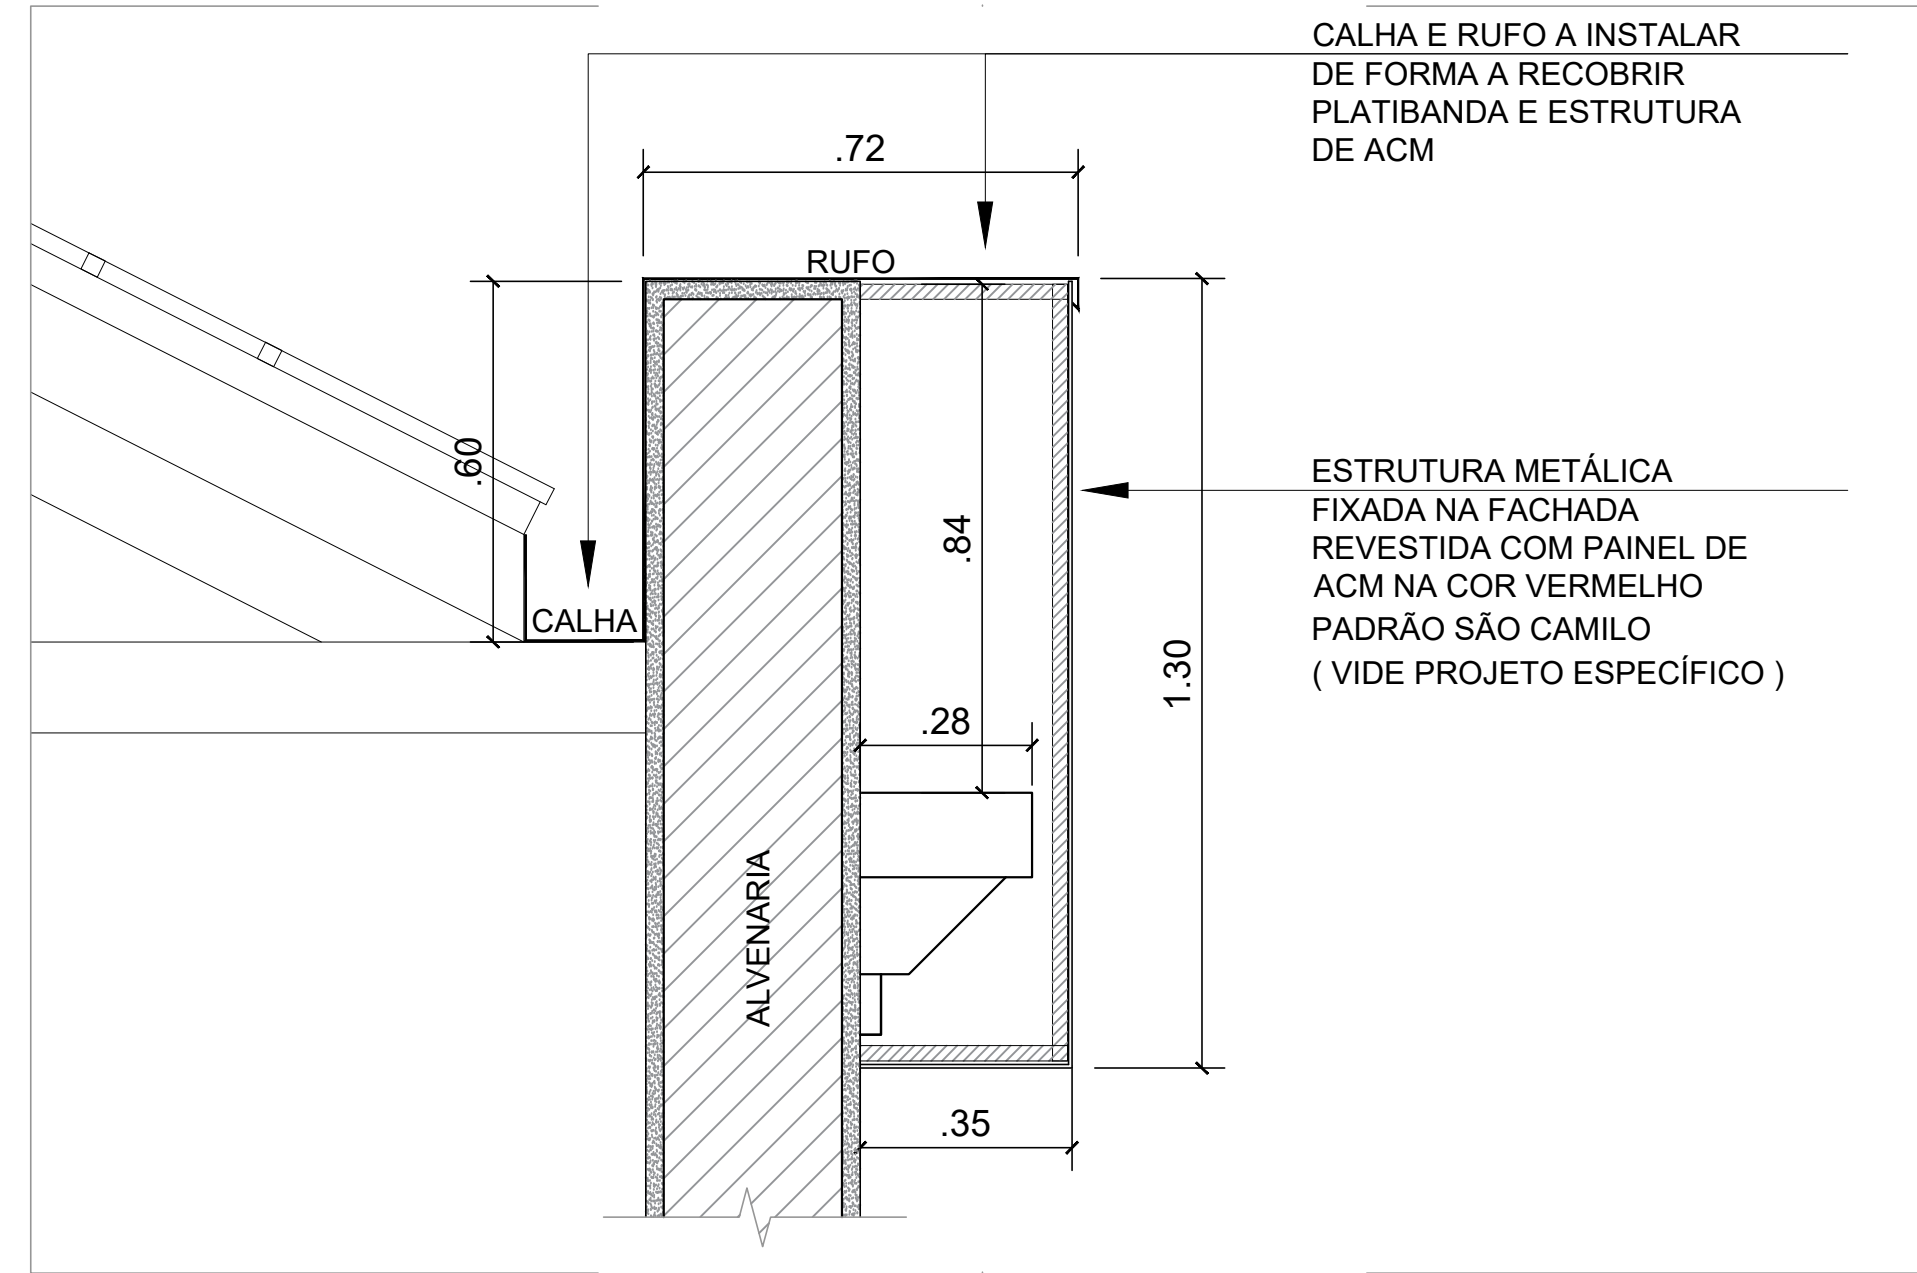



DET. 03- ORIENTATIVO
ESCALA 1:25

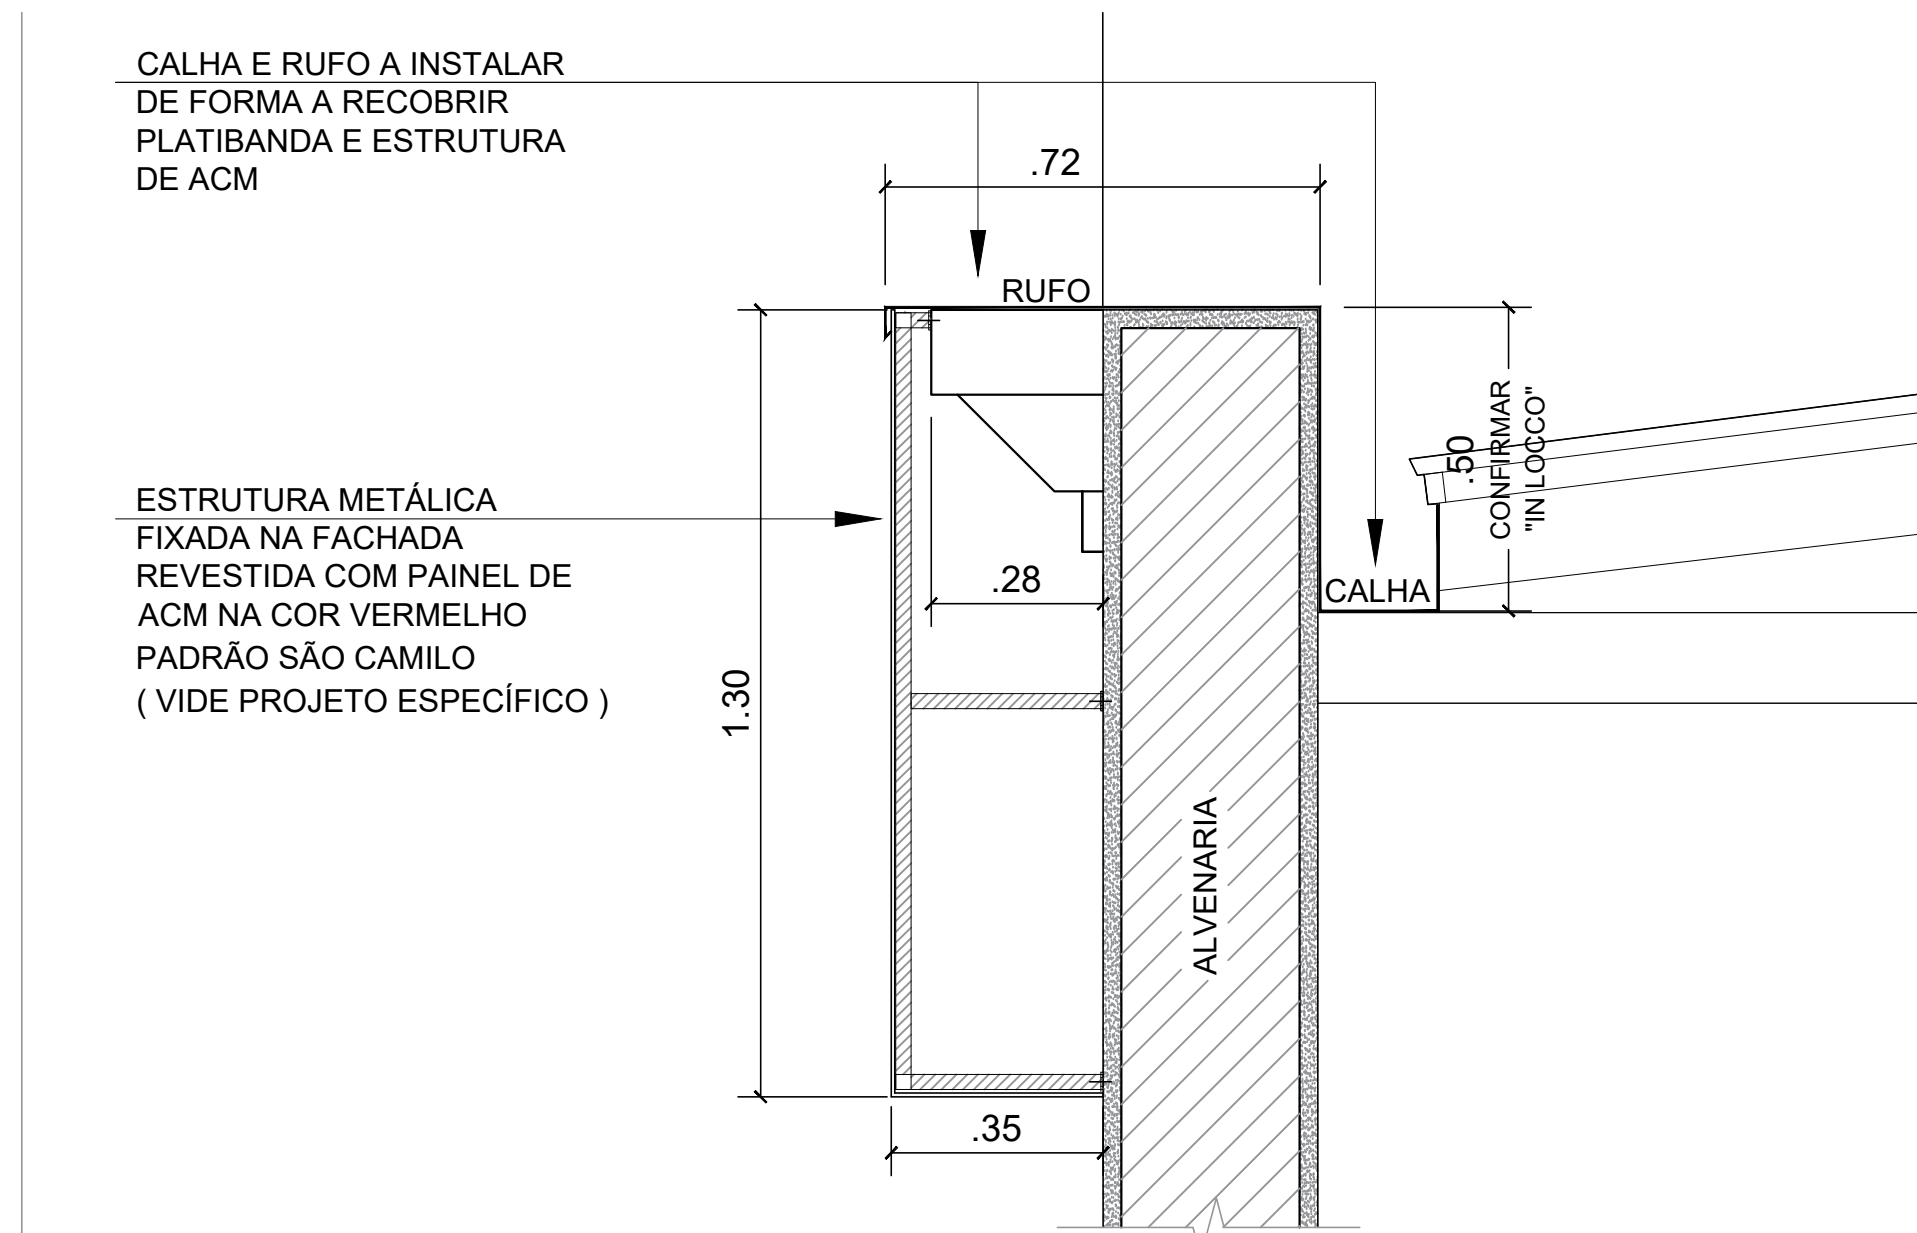


DET. 05
ORIENTATIVO
ESCALA 1:25

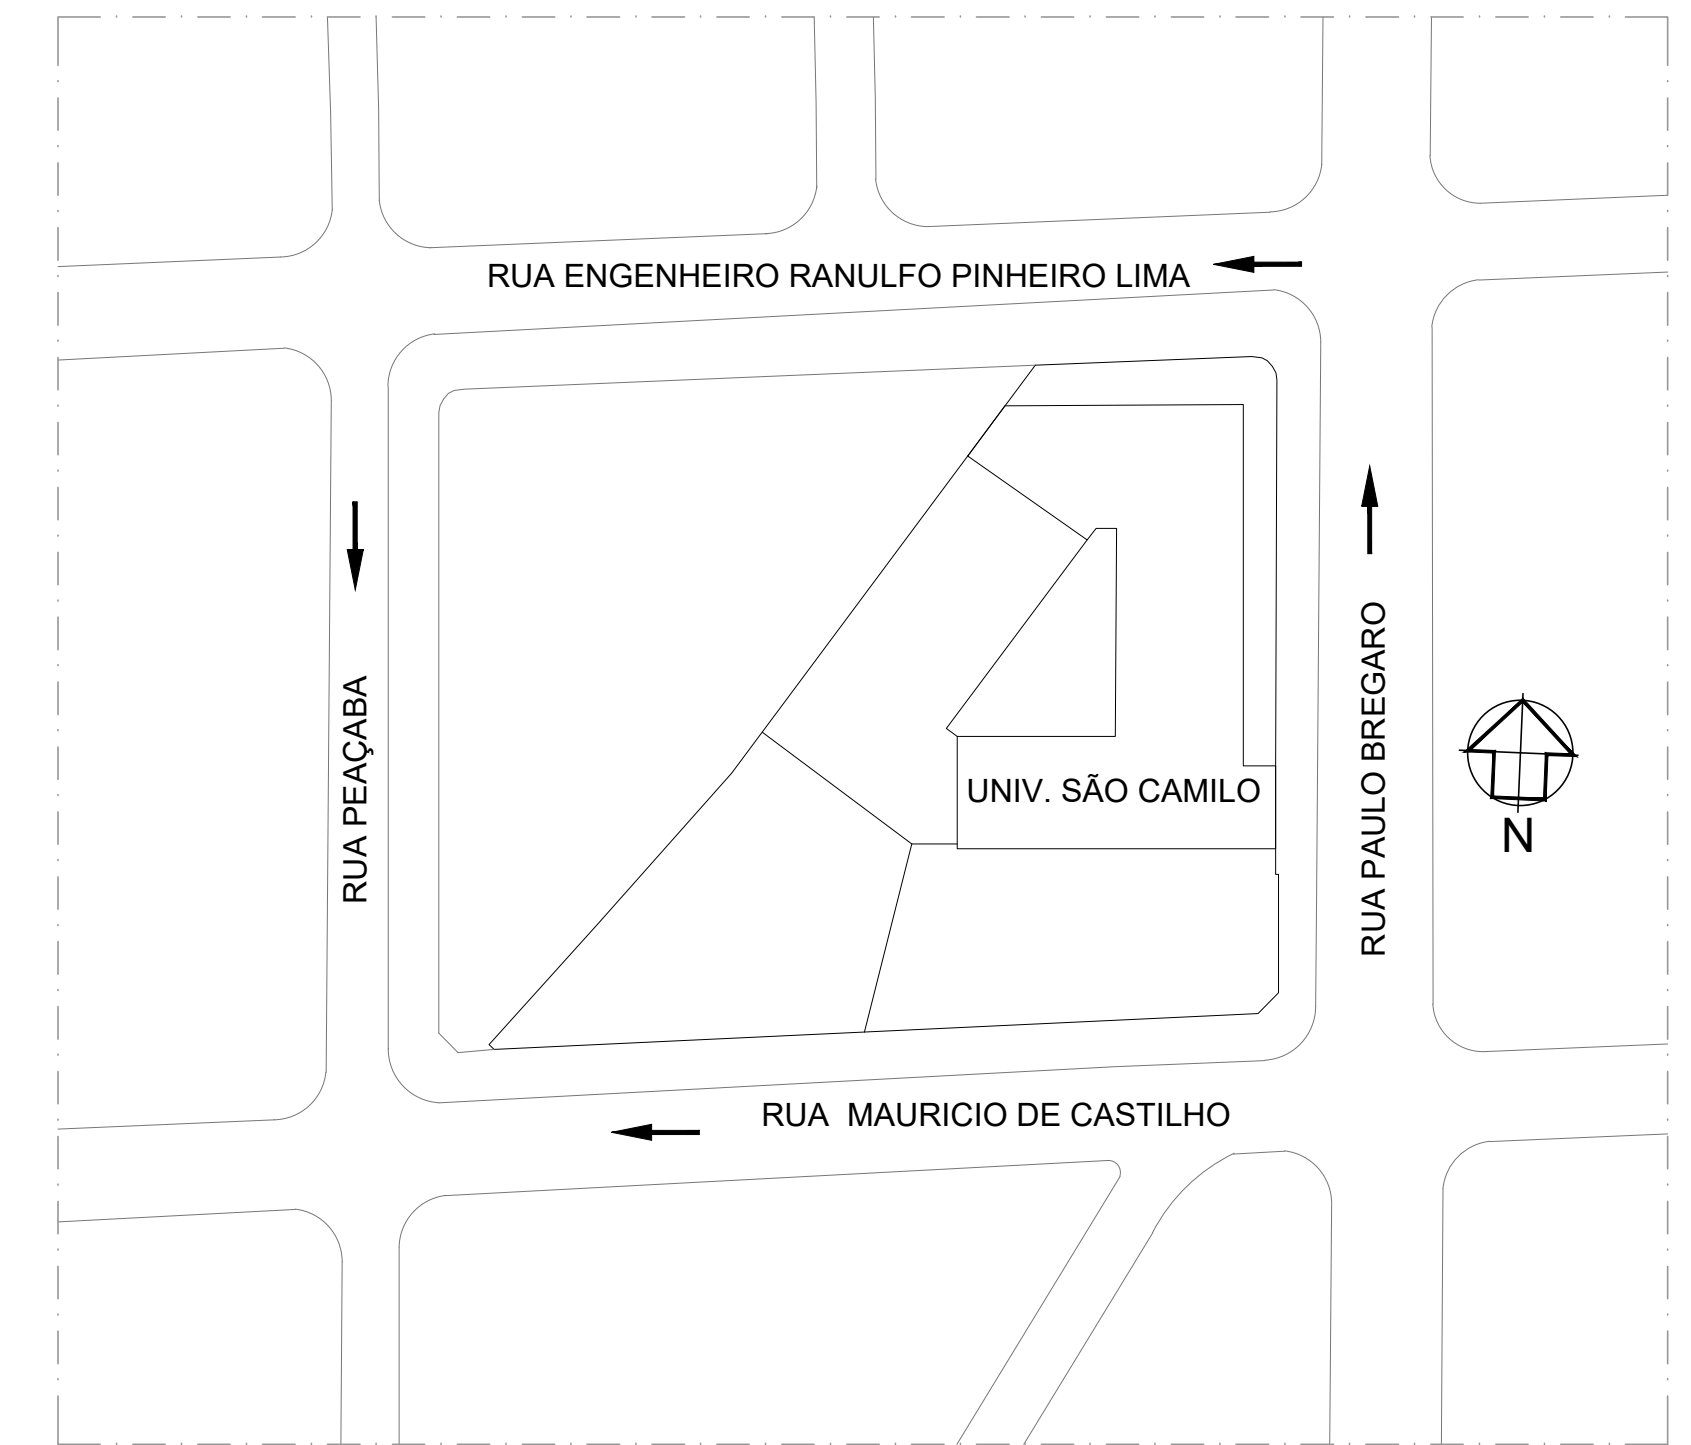

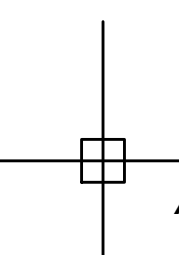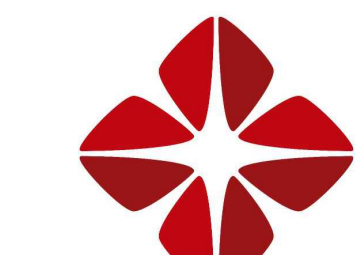
02	27.07.26	MUDANÇA NOS FORMATOS CONF. SOLICITAÇÃO DA ENGª DO SÃO CAMILO
01	07.11.24	REVISÃO GERAL CONFORME APONTAMENTOS
REVISÃO:	DATA:	DESCRIÇÃO:
PROJETISTA:  MP ARQUITETURA ARQUITETURA & CONSULTORIA		CLIENTE:  CENTRO UNIVERSITÁRIO SÃO CAMILO
PROJETO: UNIVERSIDADE SÃO CAMILO - UNIDADE IPIRANGA PROMOVE		REVISÃO: 02
ASSUNTO: REFORMA DE FACHADA / EXECUTIVO		FOLHA: 09 / 12
PISO/ FACHADA 04- CORTES E DETALHES	ESC.: INDICADA	
RESPONSÁVEL TÉCNICO: MAURO PEREIRA FILHO	DATA: 04.05.23	
CAU DO RESPONSÁVEL TÉCNICO A - 7458-6	RRT	

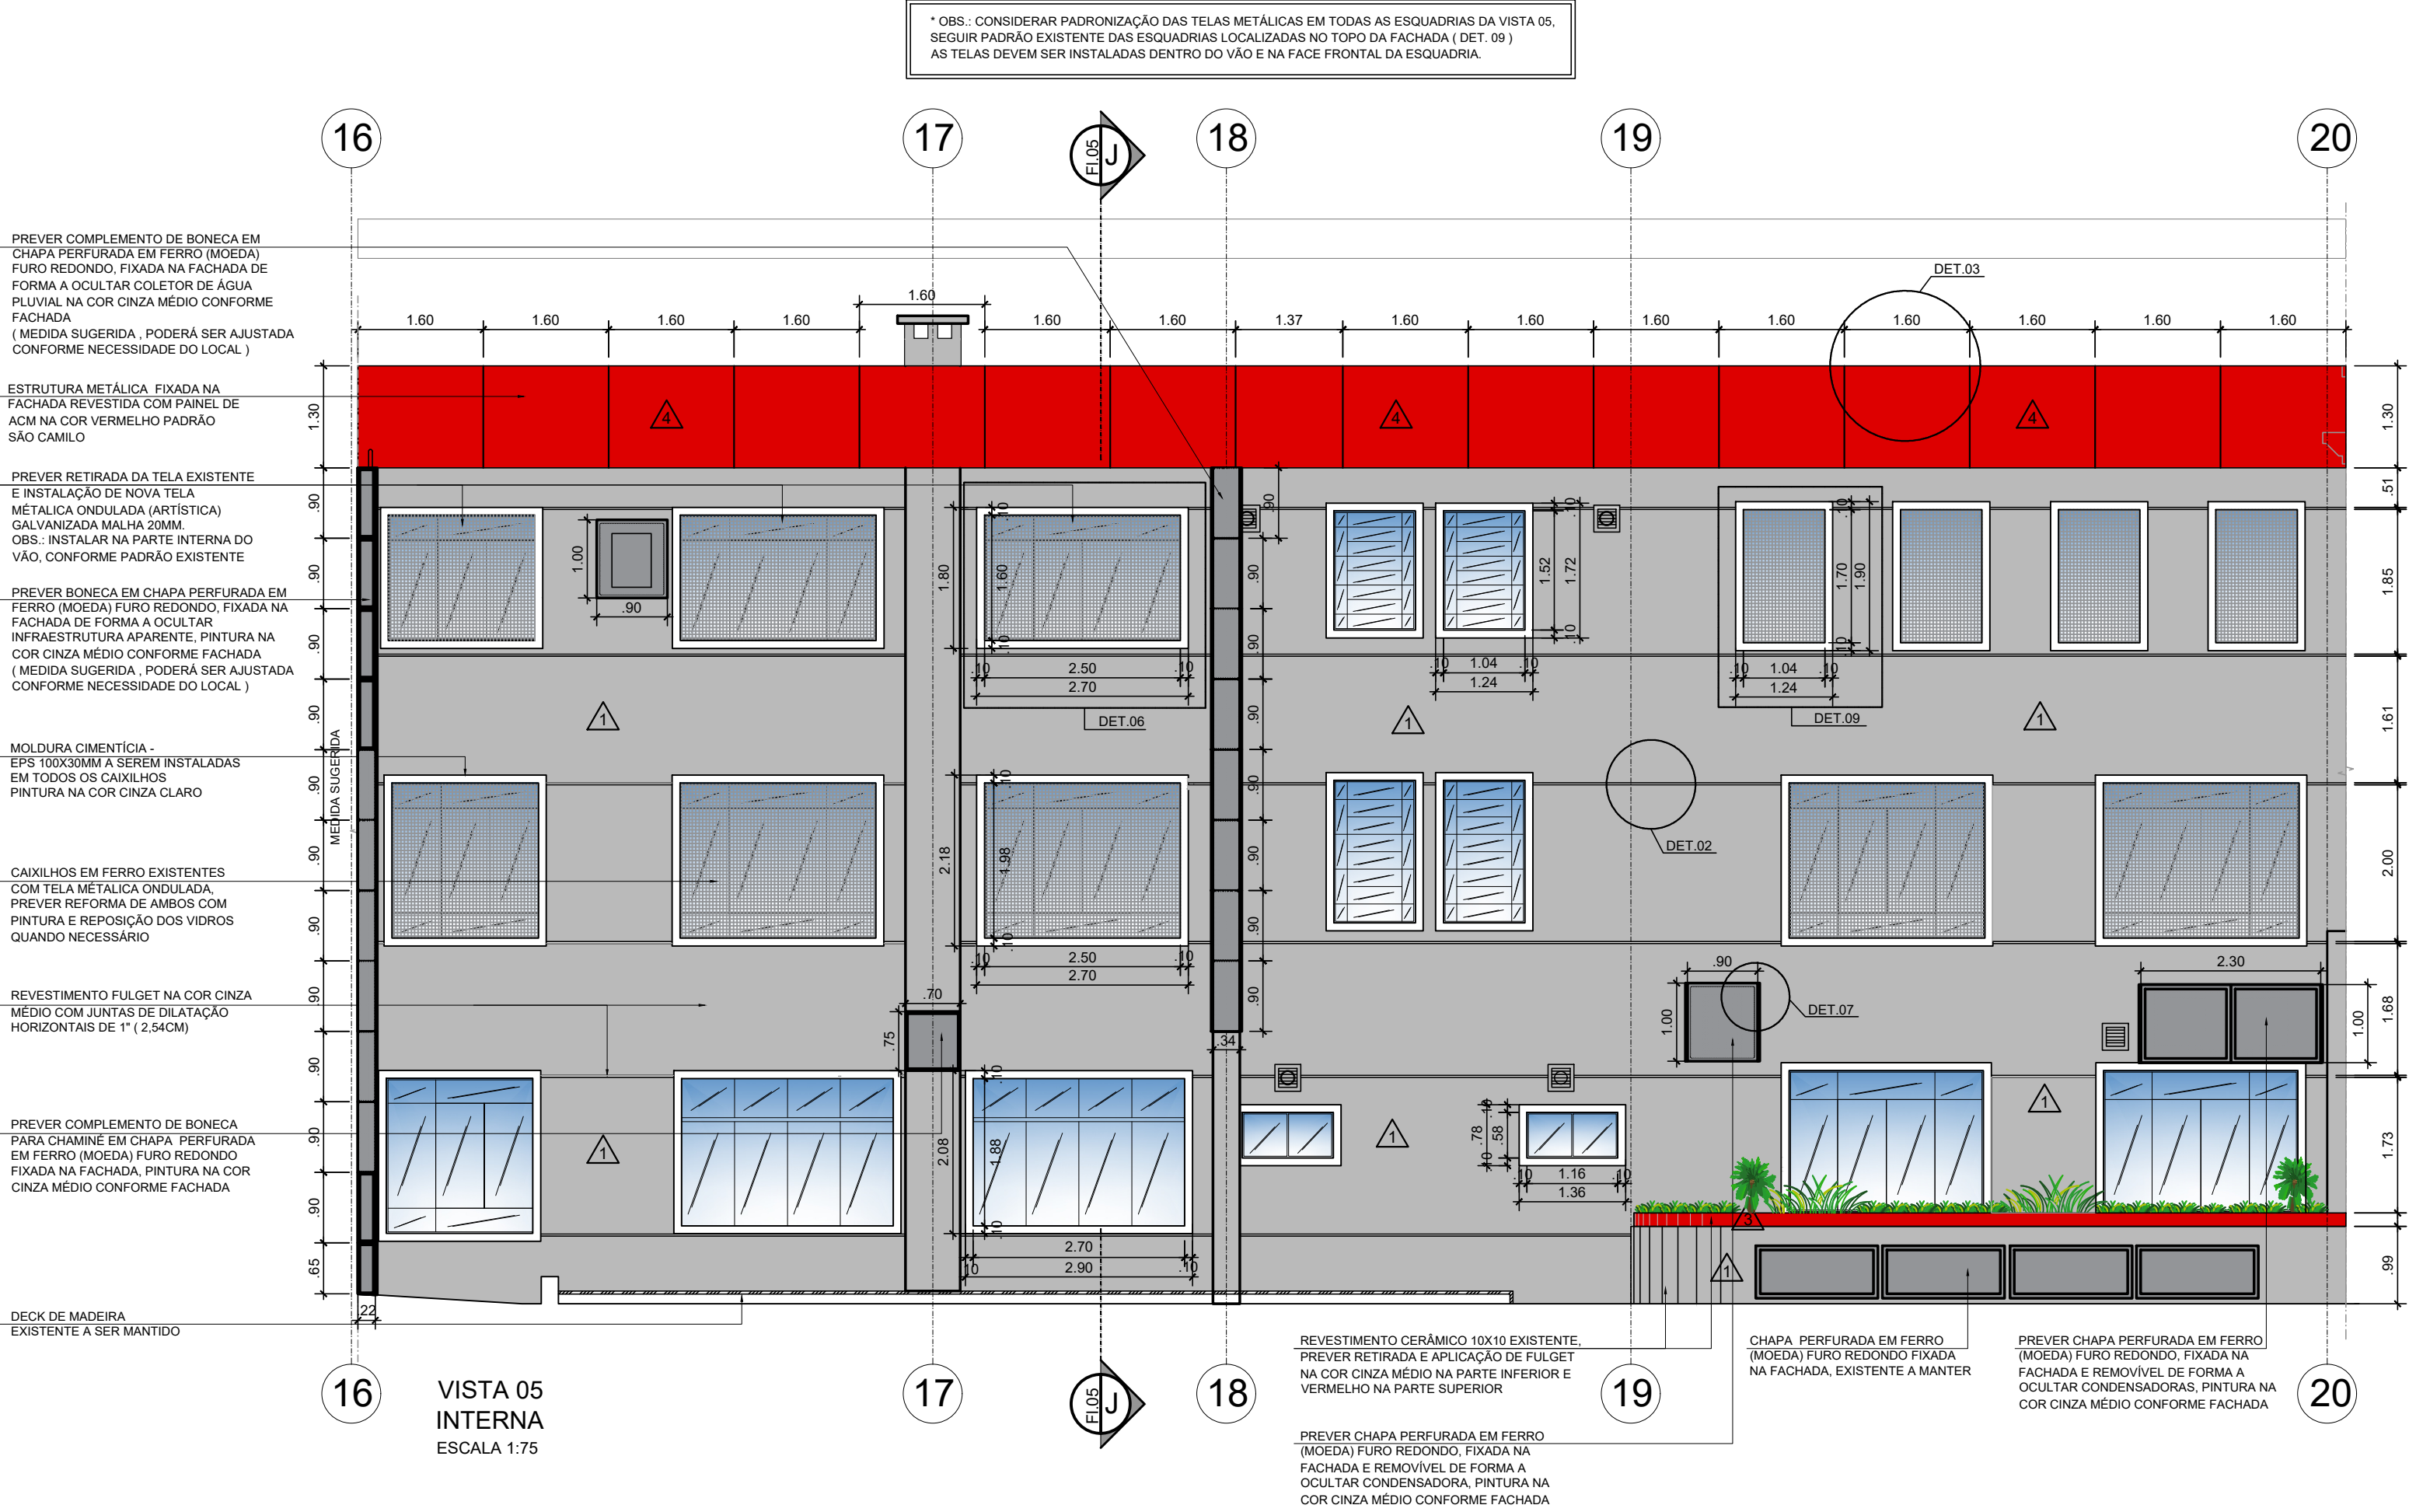


VISTA 05 INTERNA
ESCALA 1:75

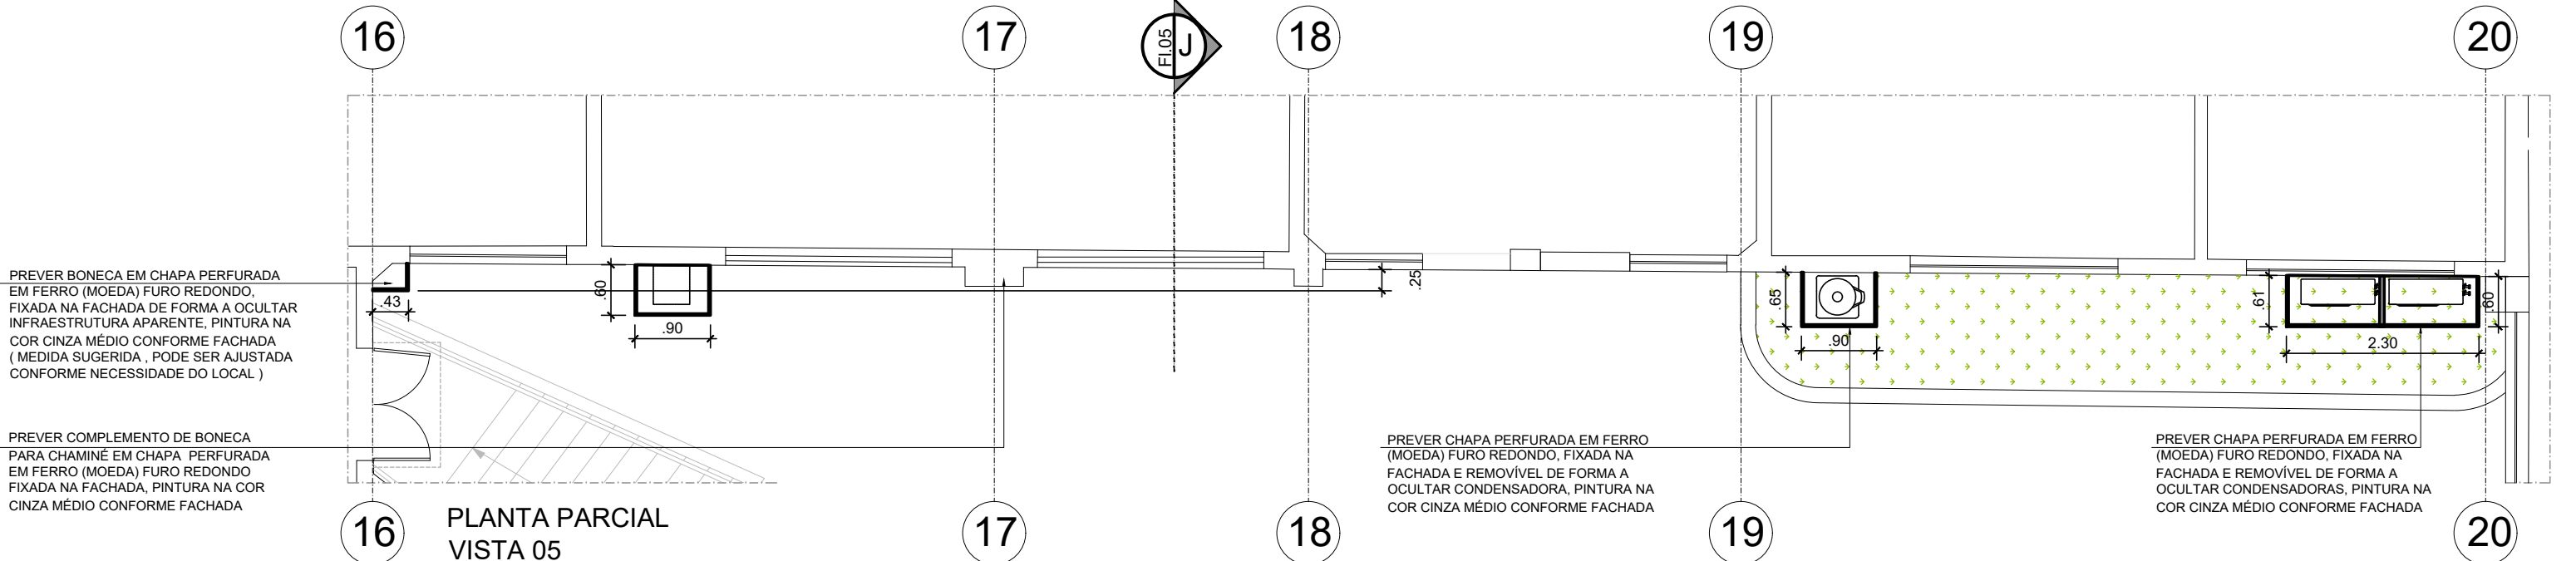


PLANTA PARCIAL
VISTA 05
ESCALA 1:75

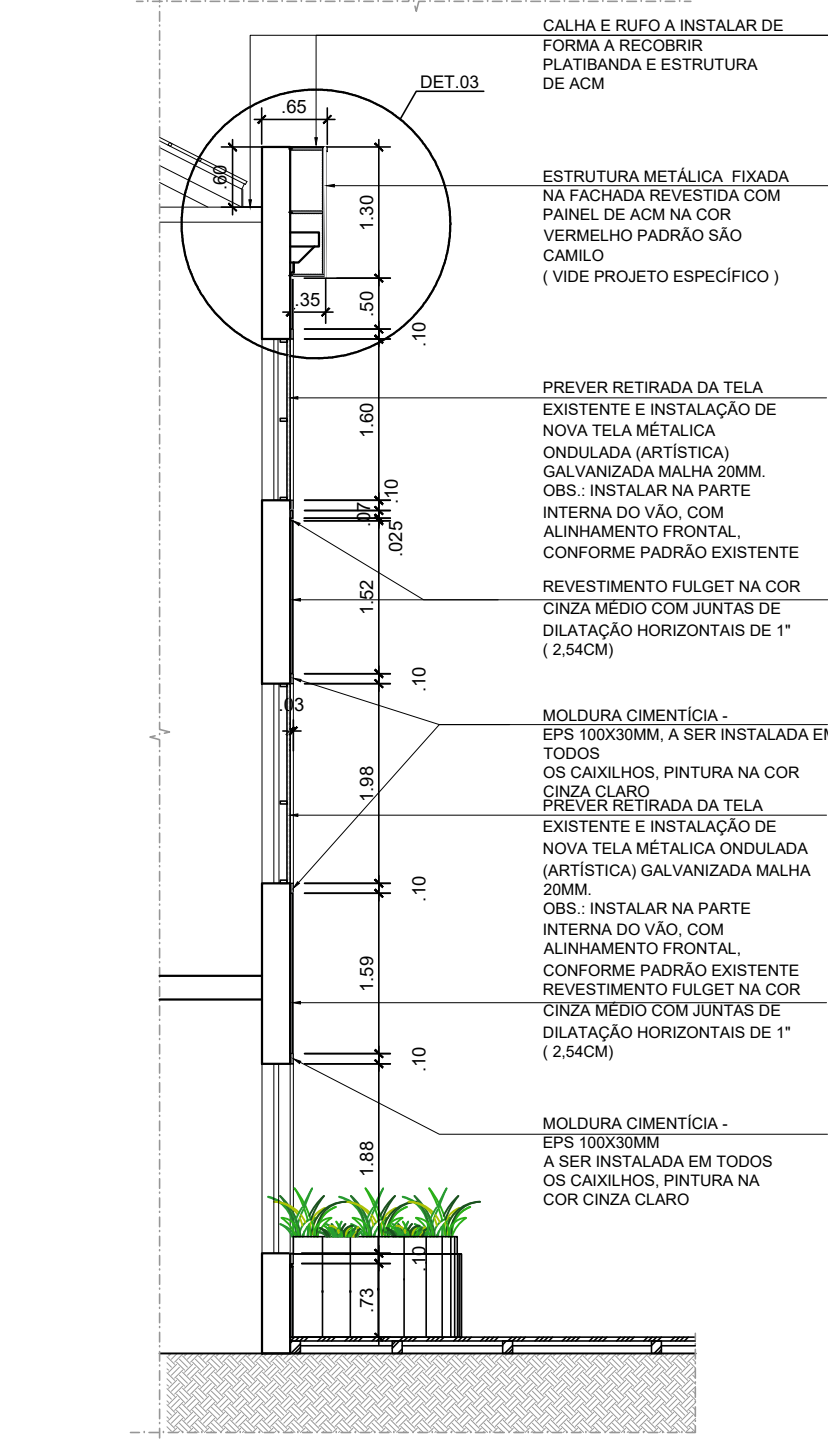


CORTE J-J
ESCALA 1:75

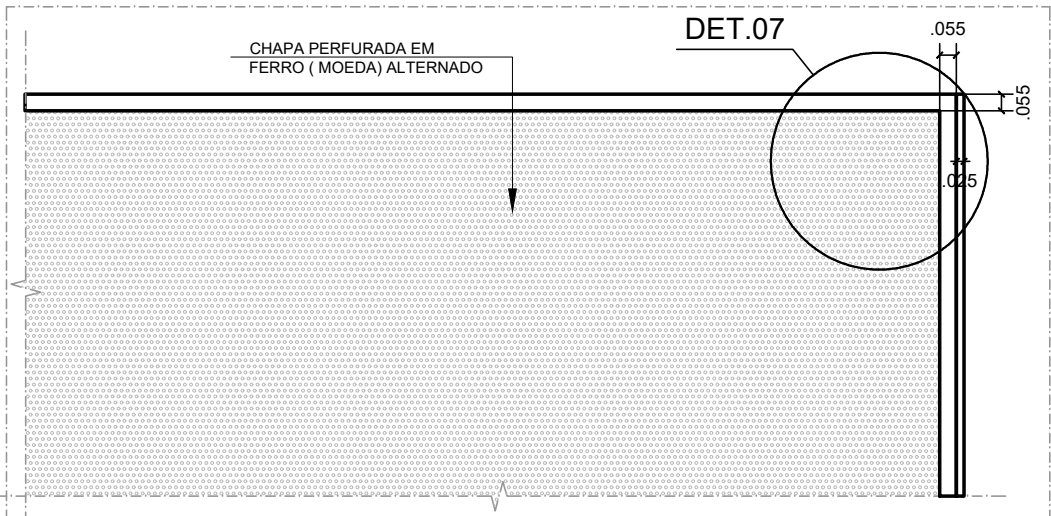


DET.07- VISTA DA CHAPA PERFORADA
ESCALA 1:25

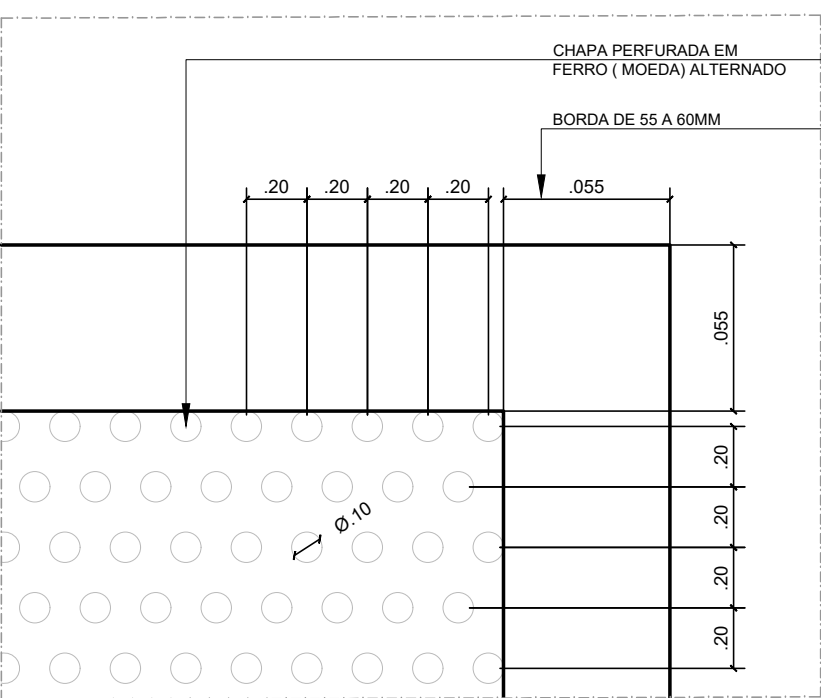


DET. 07
ESCALA 1:25

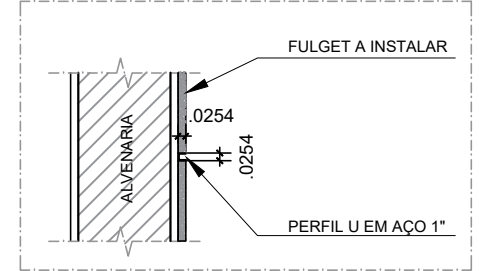


DET. 02
ESCALA 1:25

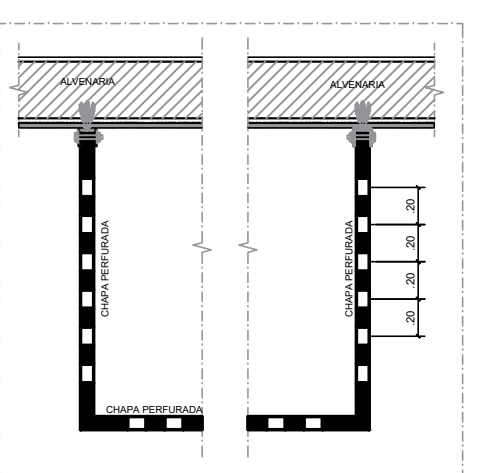


DET. 07
GENÉRICO
FIXAÇÃO DA CHAPA PERFORADA
ESCALA 1:25

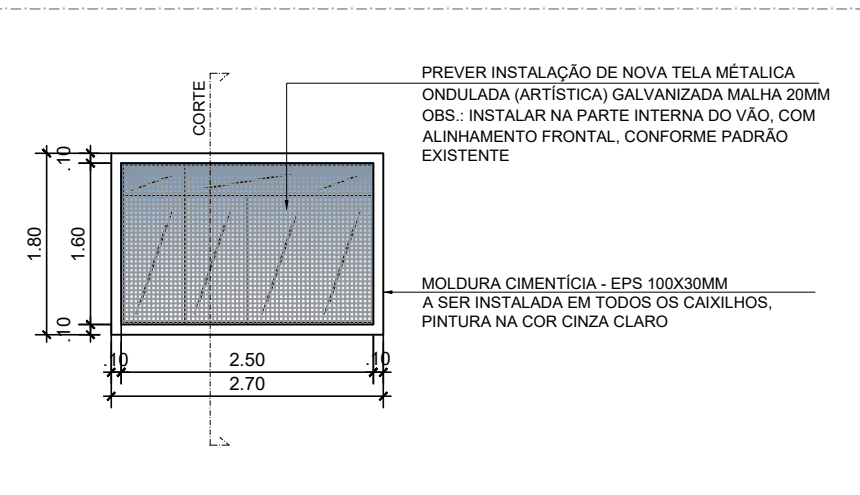


DET. 06- VISTA 5
(COM TELA METÁLICA)
ESCALA 1:75

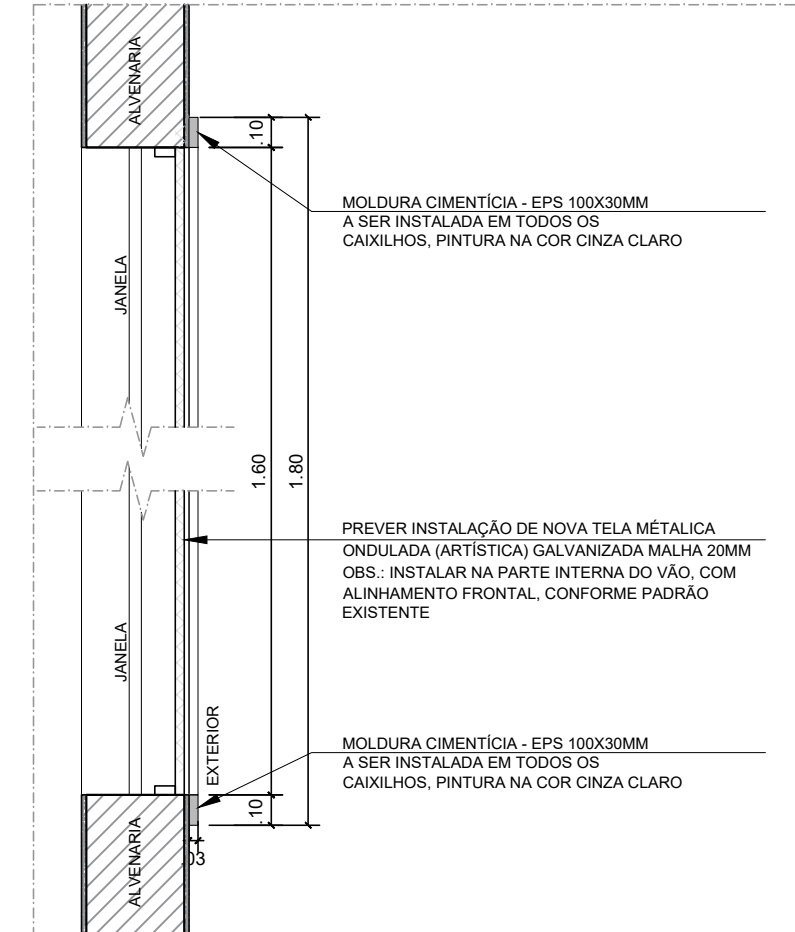


DET. 06- CORTE
(COM TELA METÁLICA)
ESCALA 1:25

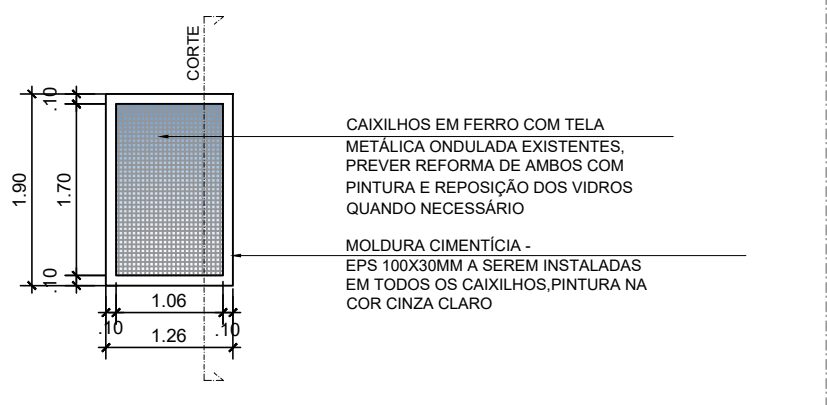

DET. 09- VISTA 5
(COM TELA METÁLICA)
ESCALA 1:75

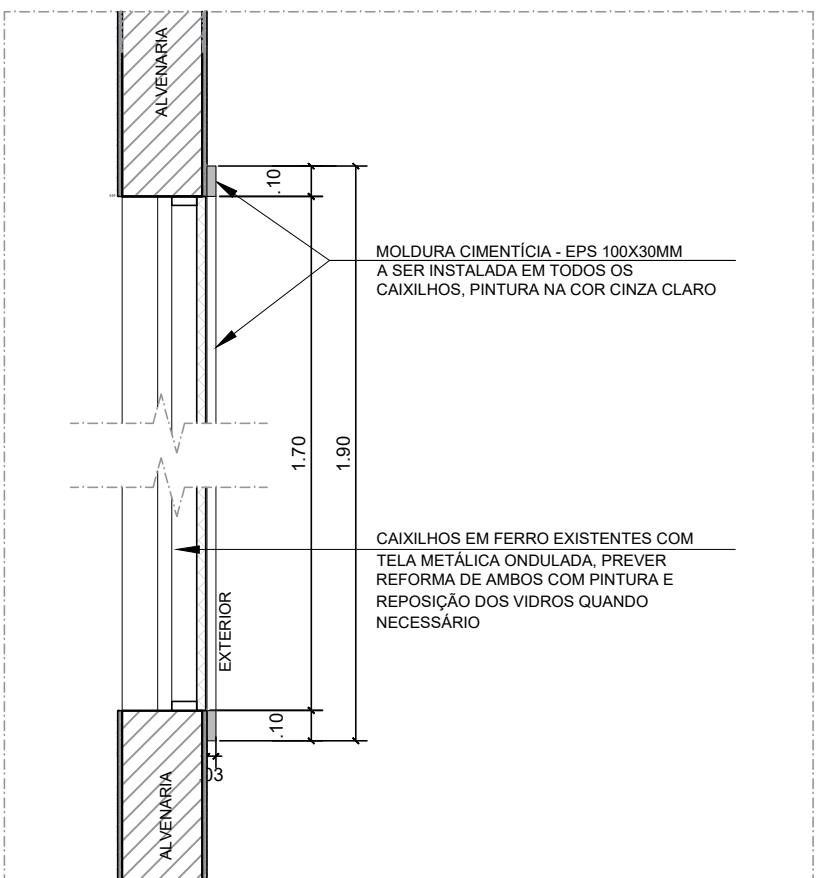

DET. 09- CORTE
(COM TELA METÁLICA)
ESCALA 1:25


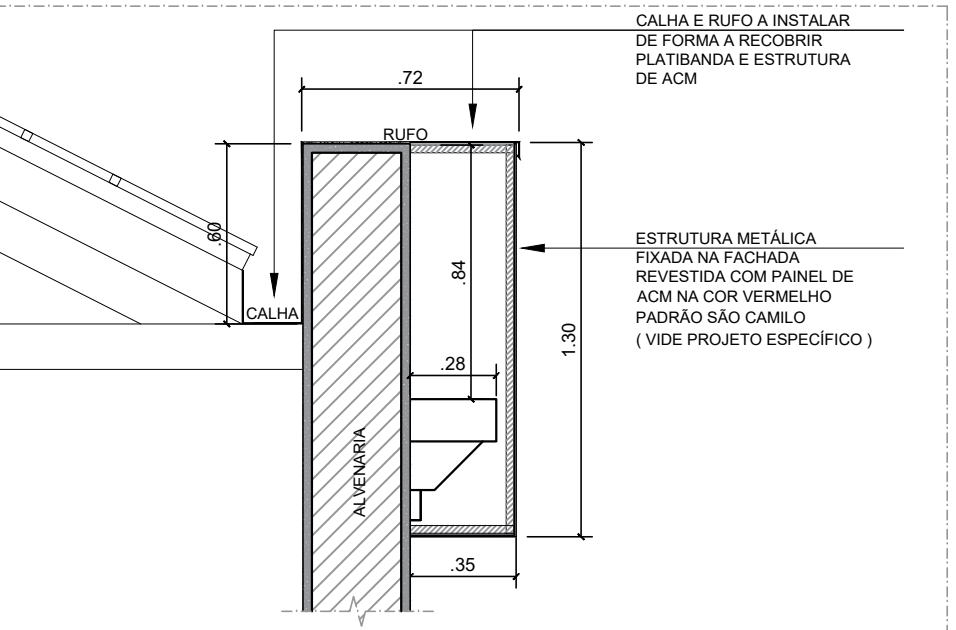


DET. 03- ORIENTATIVO
ESCALA 1:25



IMPORTANTE:
** NOTA TÉCNICA - PROJETO DE FACHADA, INSTALAÇÃO DE ACM **
A INSTALAÇÃO DE ACM NA FACHADA DO EDIFÍCIO REQUER A ELABORAÇÃO DE UM PROJETO ESPECÍFICO, QUE CONTEMPLE TODOS OS DETALHES TÉCNICOS E ESTRUTURAIS NECESSÁRIOS PARA GARANTIR A EXECUÇÃO SEGURA, EFICIENTE E ESTETICAMENTE SATISFATÓRIA DO MATERIAL. O PROJETO DEVERÁ ESPECIFICAR AS CONDIÇÕES DE FIXAÇÃO, INCLUINDO SUPORTES, ANCORAGENS E DETALHES DE ACABAMENTO, RESPEITANDO AS NORMAS DE SEGURANÇA E DESEMPENHO.

LEGENDA DE ACABAMENTOS

△ PAREDES EXTERNAS
1 REVESTIMENTO FULGET NA COR CINZA MÉDIO COM JUNTAS DE DILATAÇÃO HORIZONTAIS DE 1" (2,54CM)
2 REVESTIMENTO FULGET NA COR CINZA CLARO COM JUNTAS DE DILATAÇÃO HORIZONTAIS DE 1" (2,54CM)
3 REVESTIMENTO FULGET NA COR VERMELHO
4 ESTRUTURA METÁLICA, FIXADA NA FACHADA REVESTIDA COM PAINEL DE ACM NA COR VERMELHO PADRÃO SÃO CAMILO (VIDE PROJETO ESPECÍFICO)
5 ESTRUTURA METÁLICA, FIXADA NA FACHADA REVESTIDA COM PAINEL DE ACM NA CINZA MÉDIO (VIDE PROJETO ESPECÍFICO)
6 TUILO DE VIDRO 190X190X6MM ONDULADO INCOLOR, E BARRAS DE AÇO DE 6MM DE DIÂMETRO PARA TRAVAMENTO VERTICAL E HORIZONTAL A INSTALAR
7 TUILO DE VIDRO 200X200X6MM COM VENTILAÇÃO, INCOLOR E BARRAS DE AÇO DE 6MM DE DIÂMETRO PARA TRAVAMENTO VERTICAL E HORIZONTAL A INSTALAR
8 CERÂMICA 100X100 EXISTENTE A MANTER
9 MARQUISE EXISTENTE REVESTIDA EM CHAPA METÁLICA, PREVER NOVA PINTURA NA COR VERMELHO PADRÃO SÃO CAMILO
10 RECOMPOSIÇÃO EM MASSA COM PINTURA NA COR CINZA MÉDIO

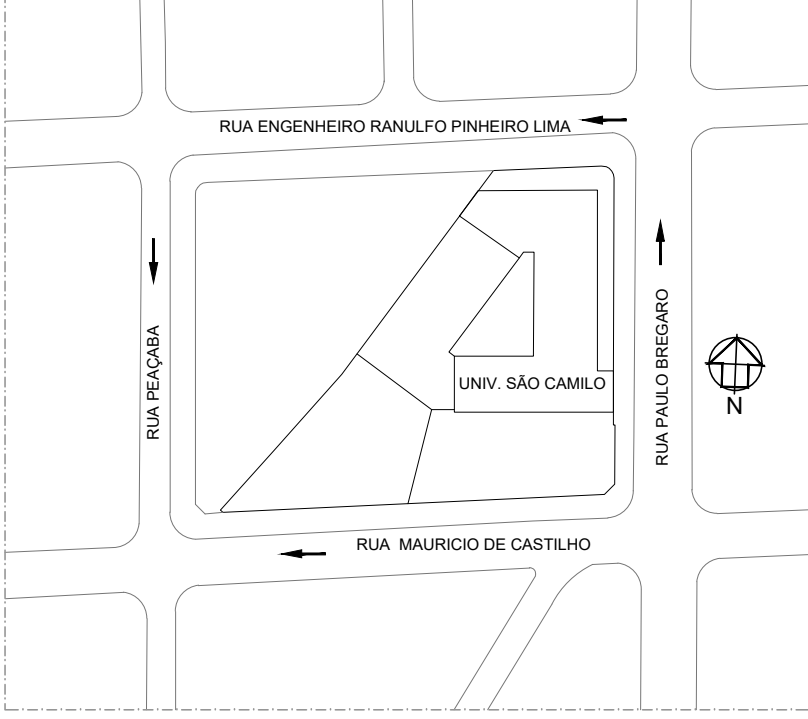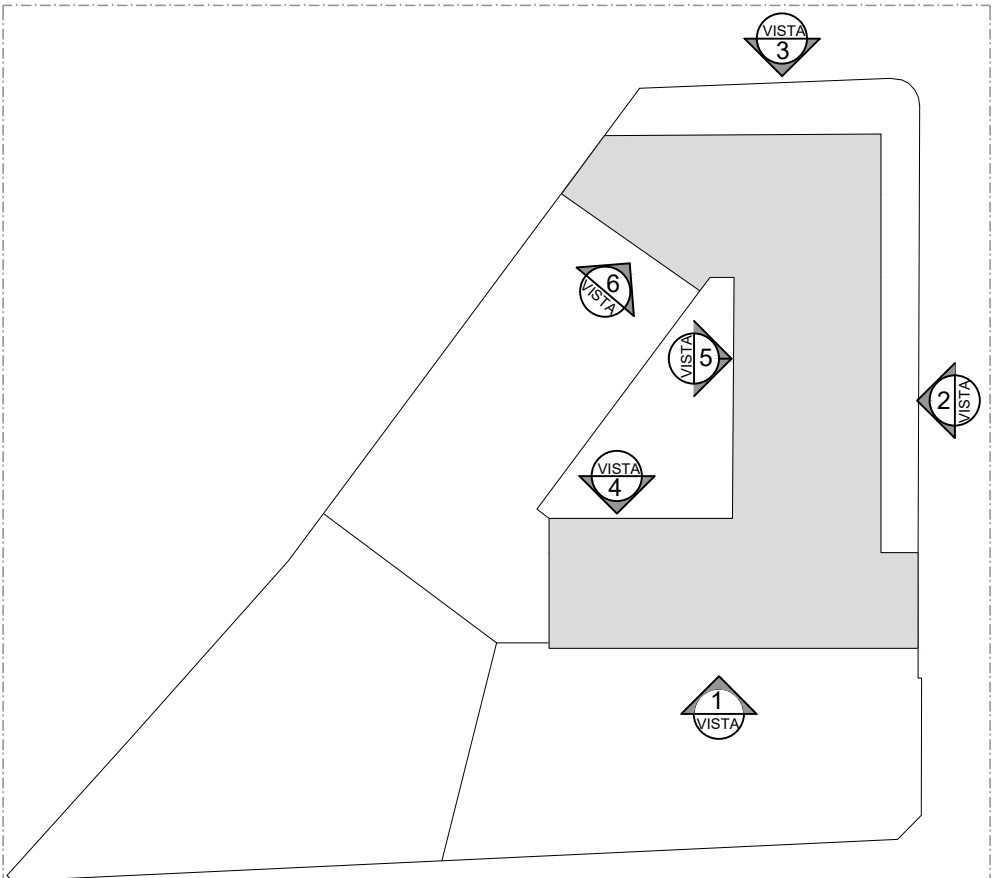

02	27.07.26	MUDANÇA NOS FORMATOS CONF. SOLICITAÇÃO DA ENGª DO SÃO CAMILO
01	07.11.24	REVISÃO GERAL CONFORME APONTAMENTOS
REVISÃO:	DATA:	DESCRIÇÃO:
PROJETISTA:	CLIENTE:	
MP ARQUITETURA ARQUITETURA & CONSULTORIA	CENTRO UNIVERSITÁRIO SÃO CAMILO	
PROJETO:	UNIVERSIDADE SÃO CAMILO - UNIDADE IPIRANGA PROMOVE	
ASSUNTO:	REFORMA DE FACHADA / EXECUTIVO	
PISO:	ESC.:	REVISÃO:
FACHADA 05- PLANTAS PARCIAIS CORTES E DETALHES	10/12	
RESPONSÁVEL TÉCNICO:	DATA:	FOLHA:
MAURO PEREIRA FILHO	04.05.23	10/12
CAU DO RESPONSÁVEL TÉCNICO	RRT	
A - 7458-6		

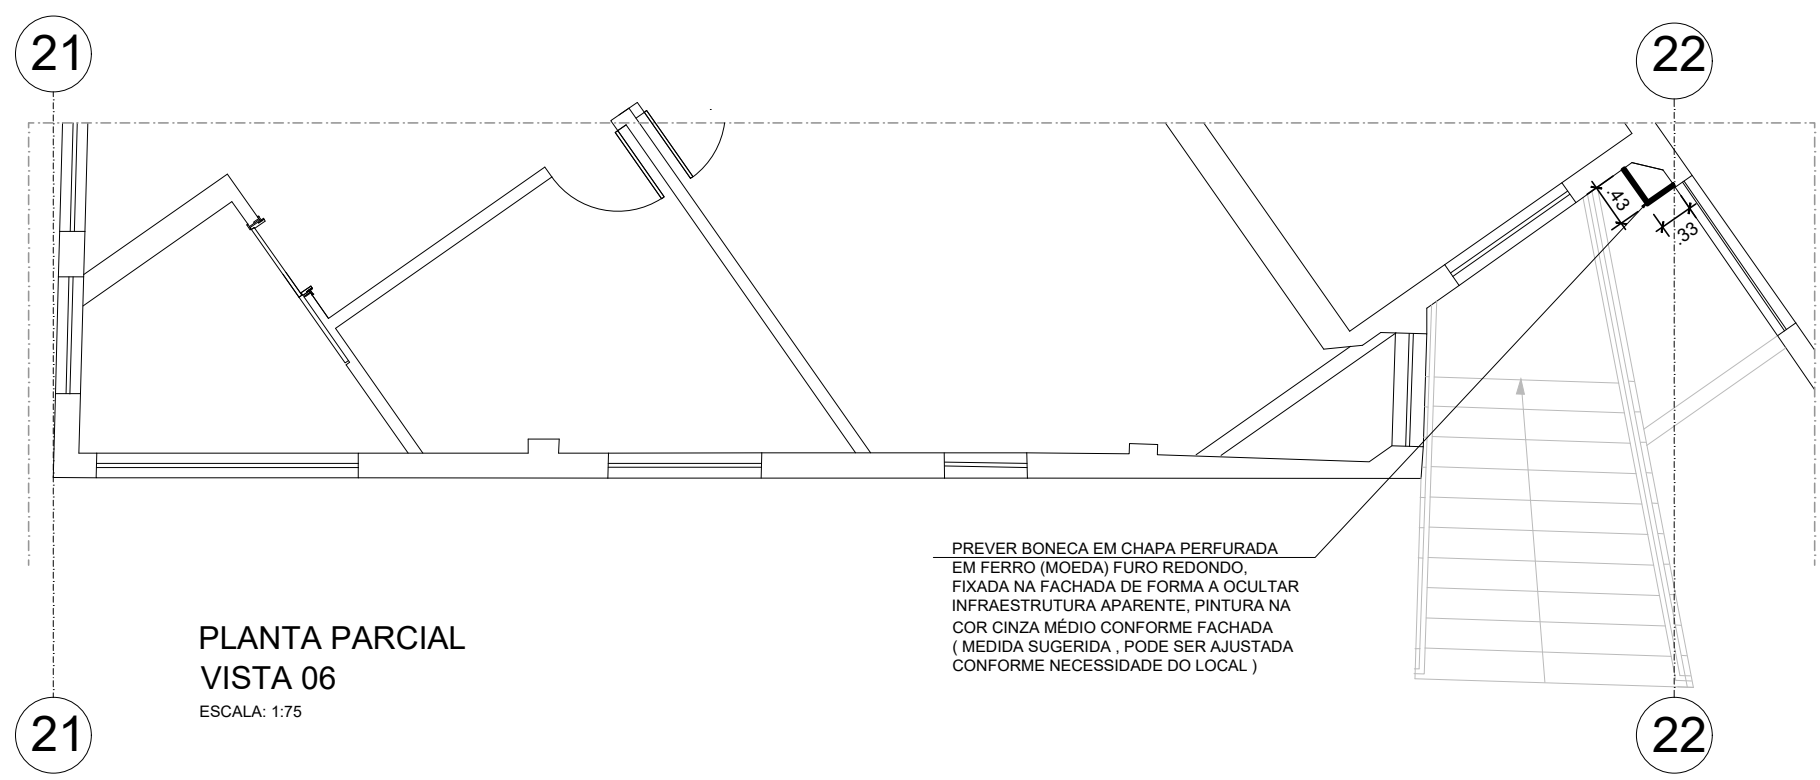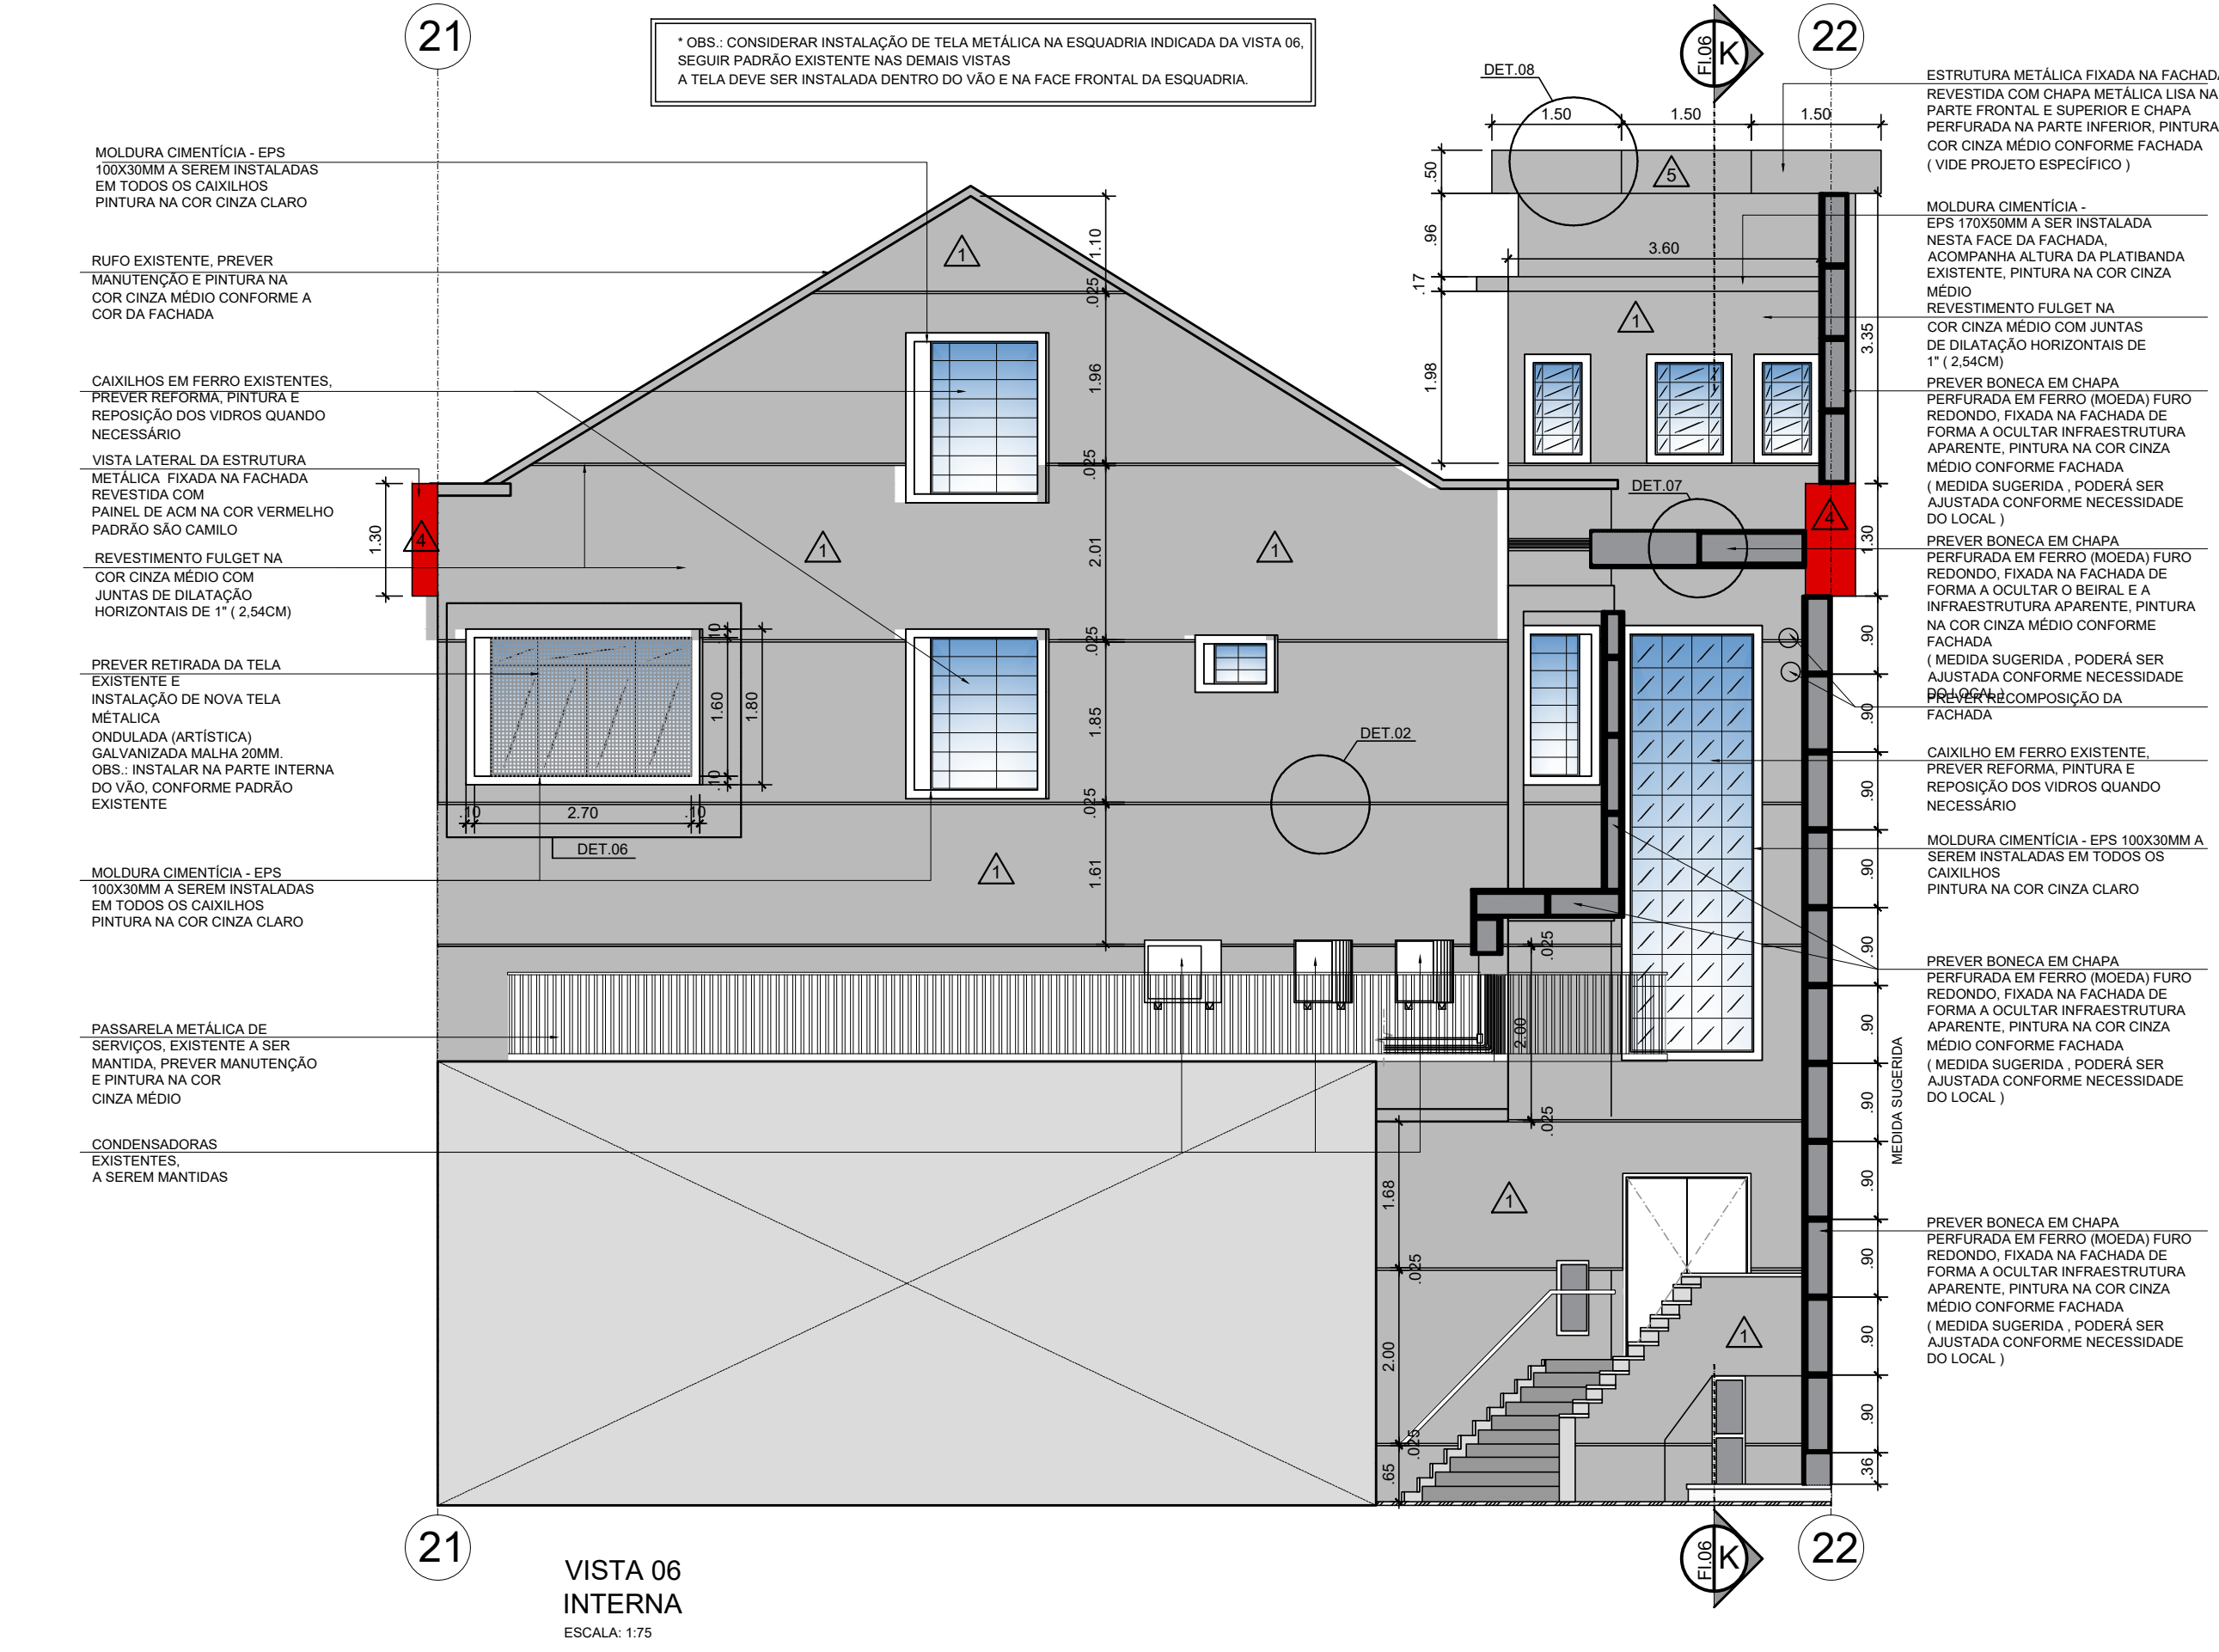

LEGENDA DE ACABAMENTOS	
△	PAREDES EXTERNAS
1	REVESTIMENTO FULGET NA COR CINZA MÉDIO COM JUNTAS DE DILATAÇÃO HORIZONTAIS DE 1" (2,54CM)
2	REVESTIMENTO FULGET NA COR CINZA CLARO COM JUNTAS DE DILATAÇÃO HORIZONTAIS DE 1" (2,54CM)
3	REVESTIMENTO FULGET NA COR VERMELHO
4	ESTRUTURA METÁLICA: FIXADA NA FACHADA REVESTIDA COM PAINEL DE ACM NA COR VERMELHO PADRÃO SÃO CAMILO (VIDE PROJETO ESPECÍFICO)
5	ESTRUTURA METÁLICA: FIXADA NA FACHADA REVESTIDA COM PAINEL DE ACM NA CINZA MÉDIO (VIDE PROJETO ESPECÍFICO)
6	TIJOLO DE VIDRO 190X190X80MM ONDULADO INCOLOR, E BARRAS DE AÇO DE 5MM DE DIÂMETRO PARA TRAVAMENTO VERTICAL E HORIZONTAL, A INSTALAR
7	TIJOLO DE VIDRO 200X200X60MM COM VENTILAÇÃO, INCOLOR E BARRAS DE AÇO DE 5MM DE DIÂMETRO PARA TRAVAMENTO VERTICAL E HORIZONTAL, A INSTALAR
8	CERÂMICA 100X100 EXISTENTE, A MANTER
9	MARQUISE EXISTENTE REVESTIDA EM CHAPA METÁLICA, PREVER NOVA PINTURA NA COR VERMELHO PADRÃO SÃO CAMILO
10	RECOMPOSIÇÃO EM MASSA COM PINTURA NA COR CINZA MÉDIO

IMPORTANTE:

**** NOTA TÉCNICA - PROJETO DE FACHADA, INSTALAÇÃO DE ACM ****

A INSTALAÇÃO DE ACM NA FACHADA DO EDIFÍCIO REQUER A ELABORAÇÃO DE UM PROJETO ESPECÍFICO, QUE CONTEMPLE TODOS OS DETALHES TÉCNICOS E ESTRUTURAIS NECESSÁRIOS PARA GARANTIR A EXECUÇÃO SEGURA, EFICIENTE E ESTETICAMENTE SATISFATÓRIA DO MATERIAL. O PROJETO DEVERÁ ESPECIFICAR AS CONDIÇÕES DE FIXAÇÃO, INCLUINDO SUPORTES, ANCORAGENS E DETALHES DE ACABAMENTO, RESPEITANDO AS NORMAS DE SEGURANÇA E DESEMPENHO.

02	27.07.26	MUDANÇA NOS FORMATOS CONF. SOLICITAÇÃO DA ENGº DO SÃO CAMILO
01	07.11.24	REVISÃO GERAL CONFORME APONTAMENTOS
REVISÃO:	DATA:	DESCRIÇÃO:

PROJETISTA:

MP ARQUITETURA
ARQUITETURA & CONSULTORIA

CLIENTE:

**CENTRO UNIVERSITÁRIO
SÃO CAMILO**

PROJETO:

UNIVERSIDADE SÃO CAMILO - UNIDADE IPIRANGA PROMOVE

ASSUNTO:

REFORMA DE FACHADA / EXECUTIVO

PISO/

FACHADA 06- PLANTA PARCIAL

RESPONSÁVEL TÉCNICO:

MAURO PEREIRA FILHO

CAU DO RESPONSÁVEL TÉCNICO

A - 7458-6

REVISÃO:

02

FOLHA:

11 / 12









ESC.: INDICADA

DATA:

04.05.23



RRT

USC_I_200_EXE_R02_FACHADA_A2_22.07.26.dwg

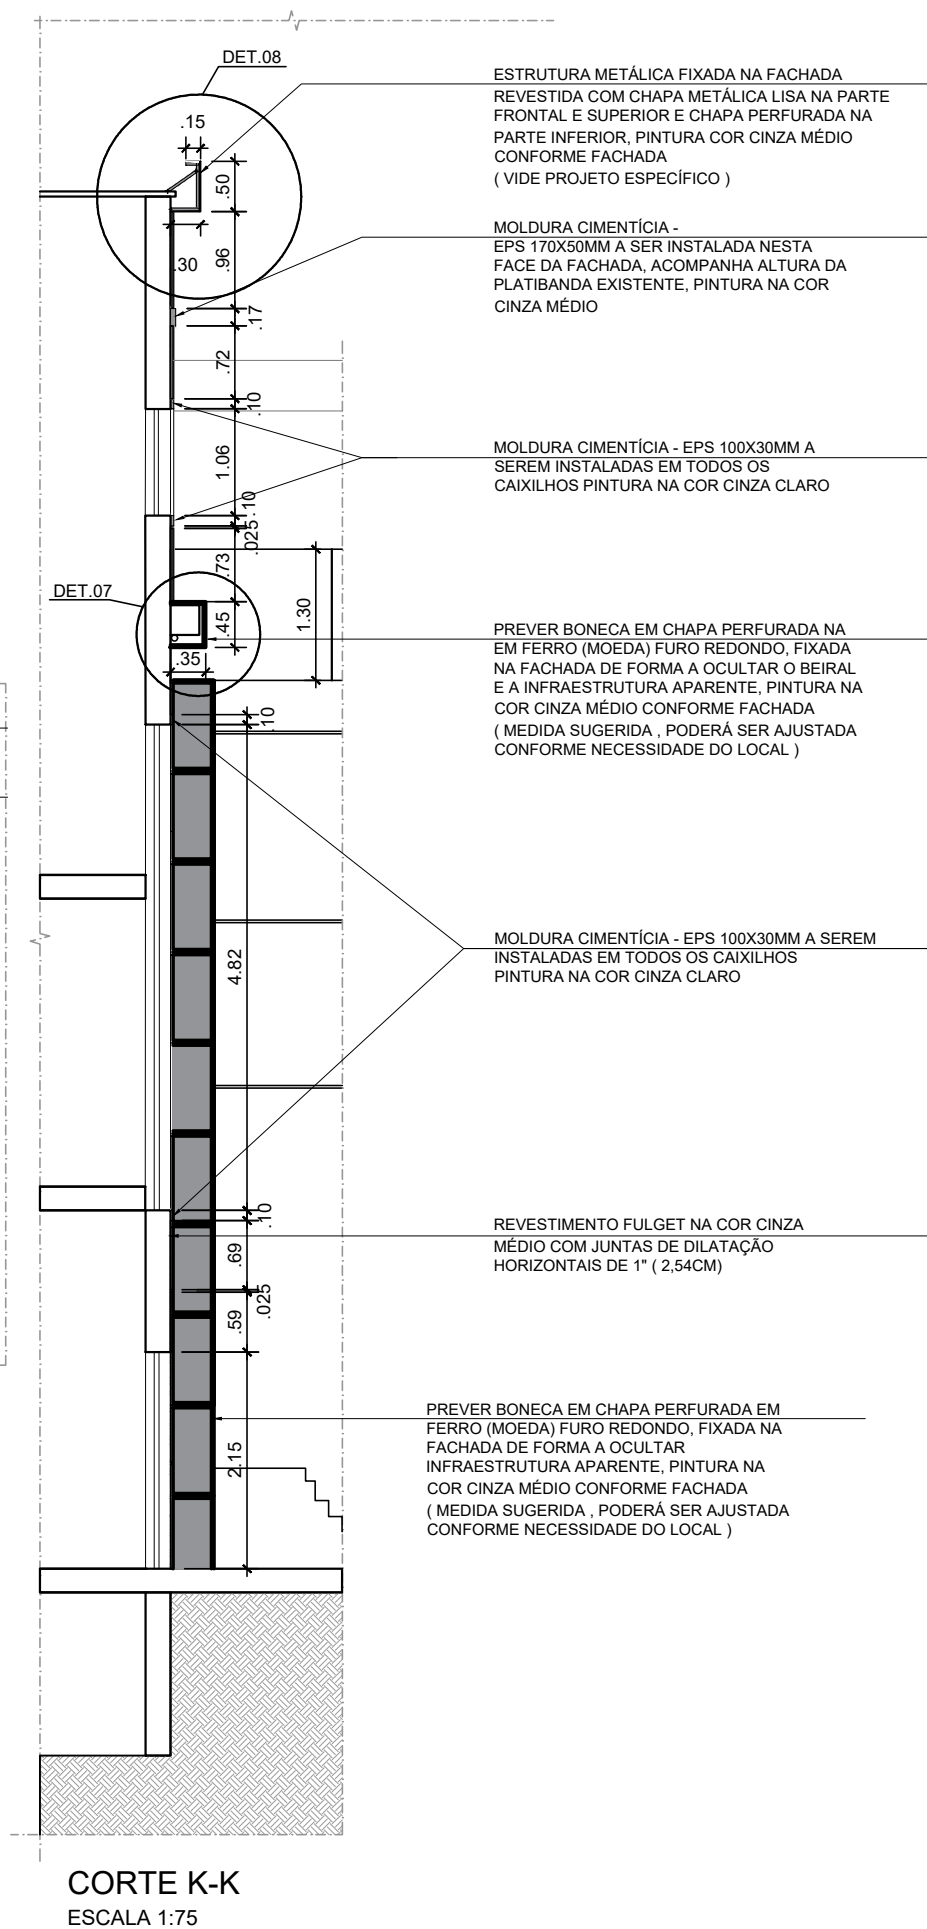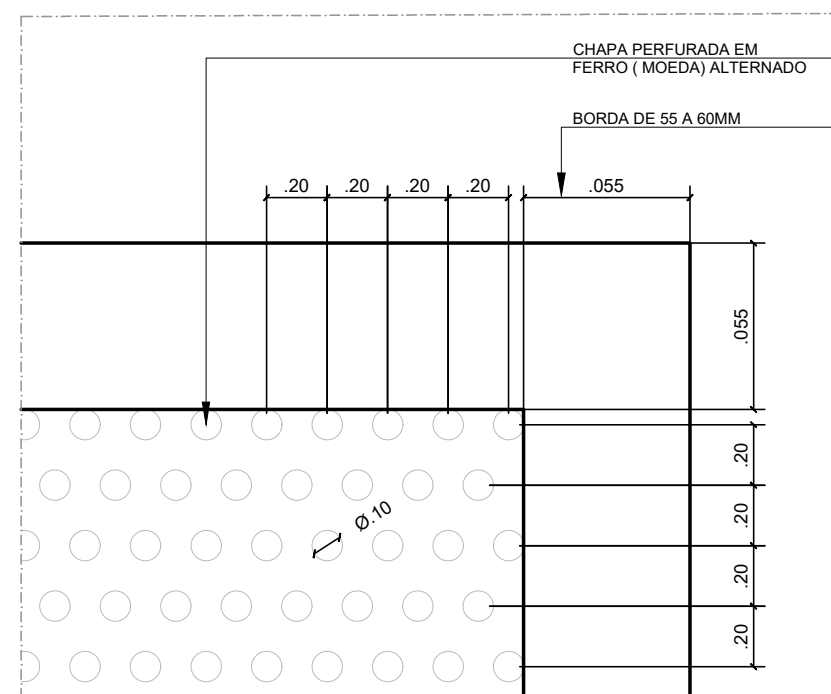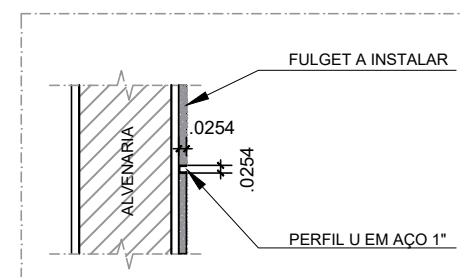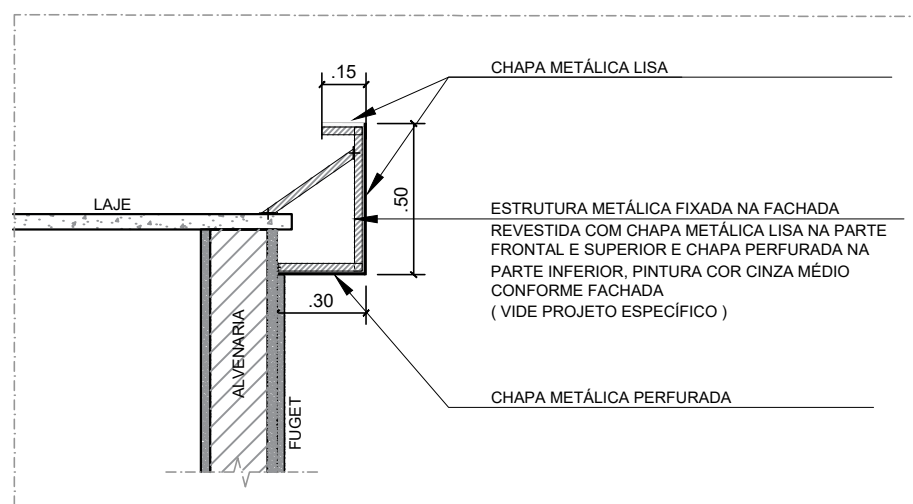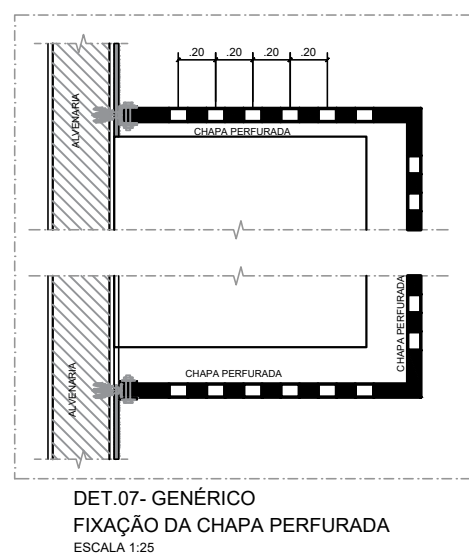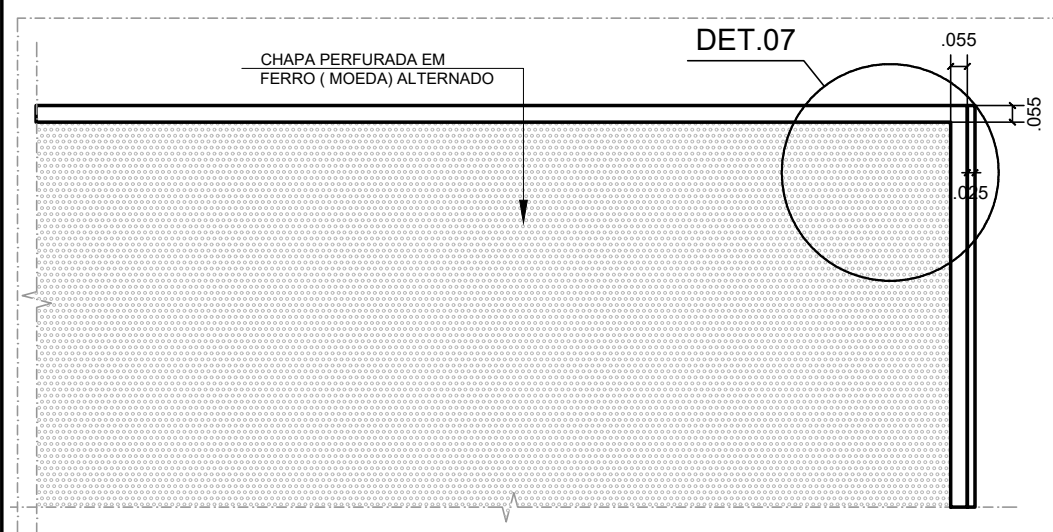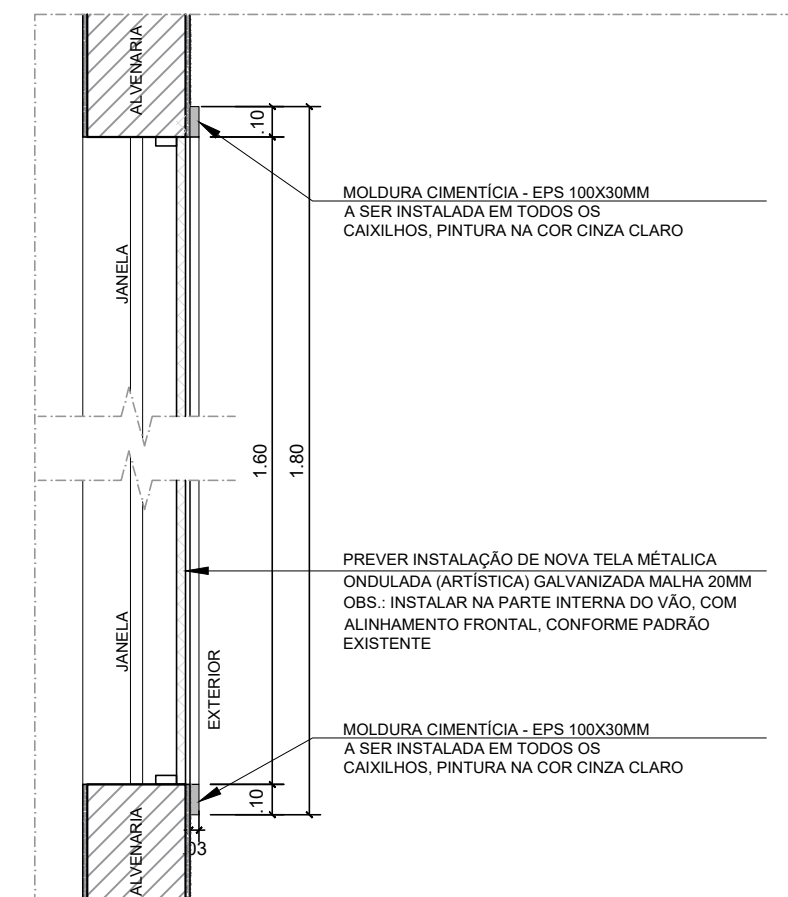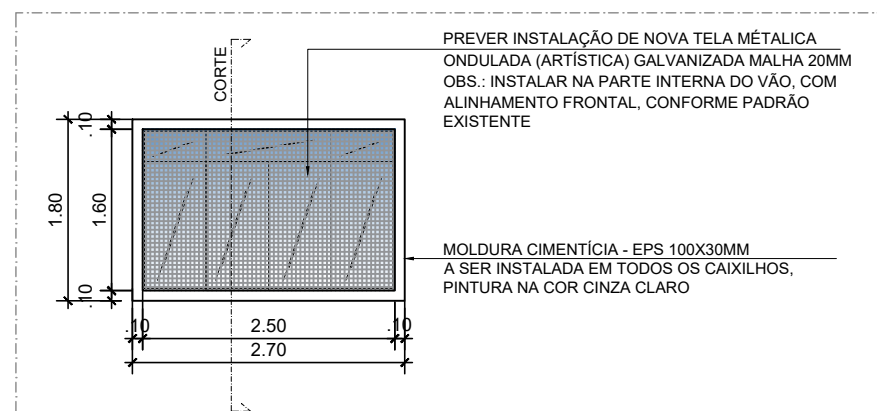





VISTA 02 - MURO EXTERNO
RUA PAULO BREGARO
ESCALA: 1:100

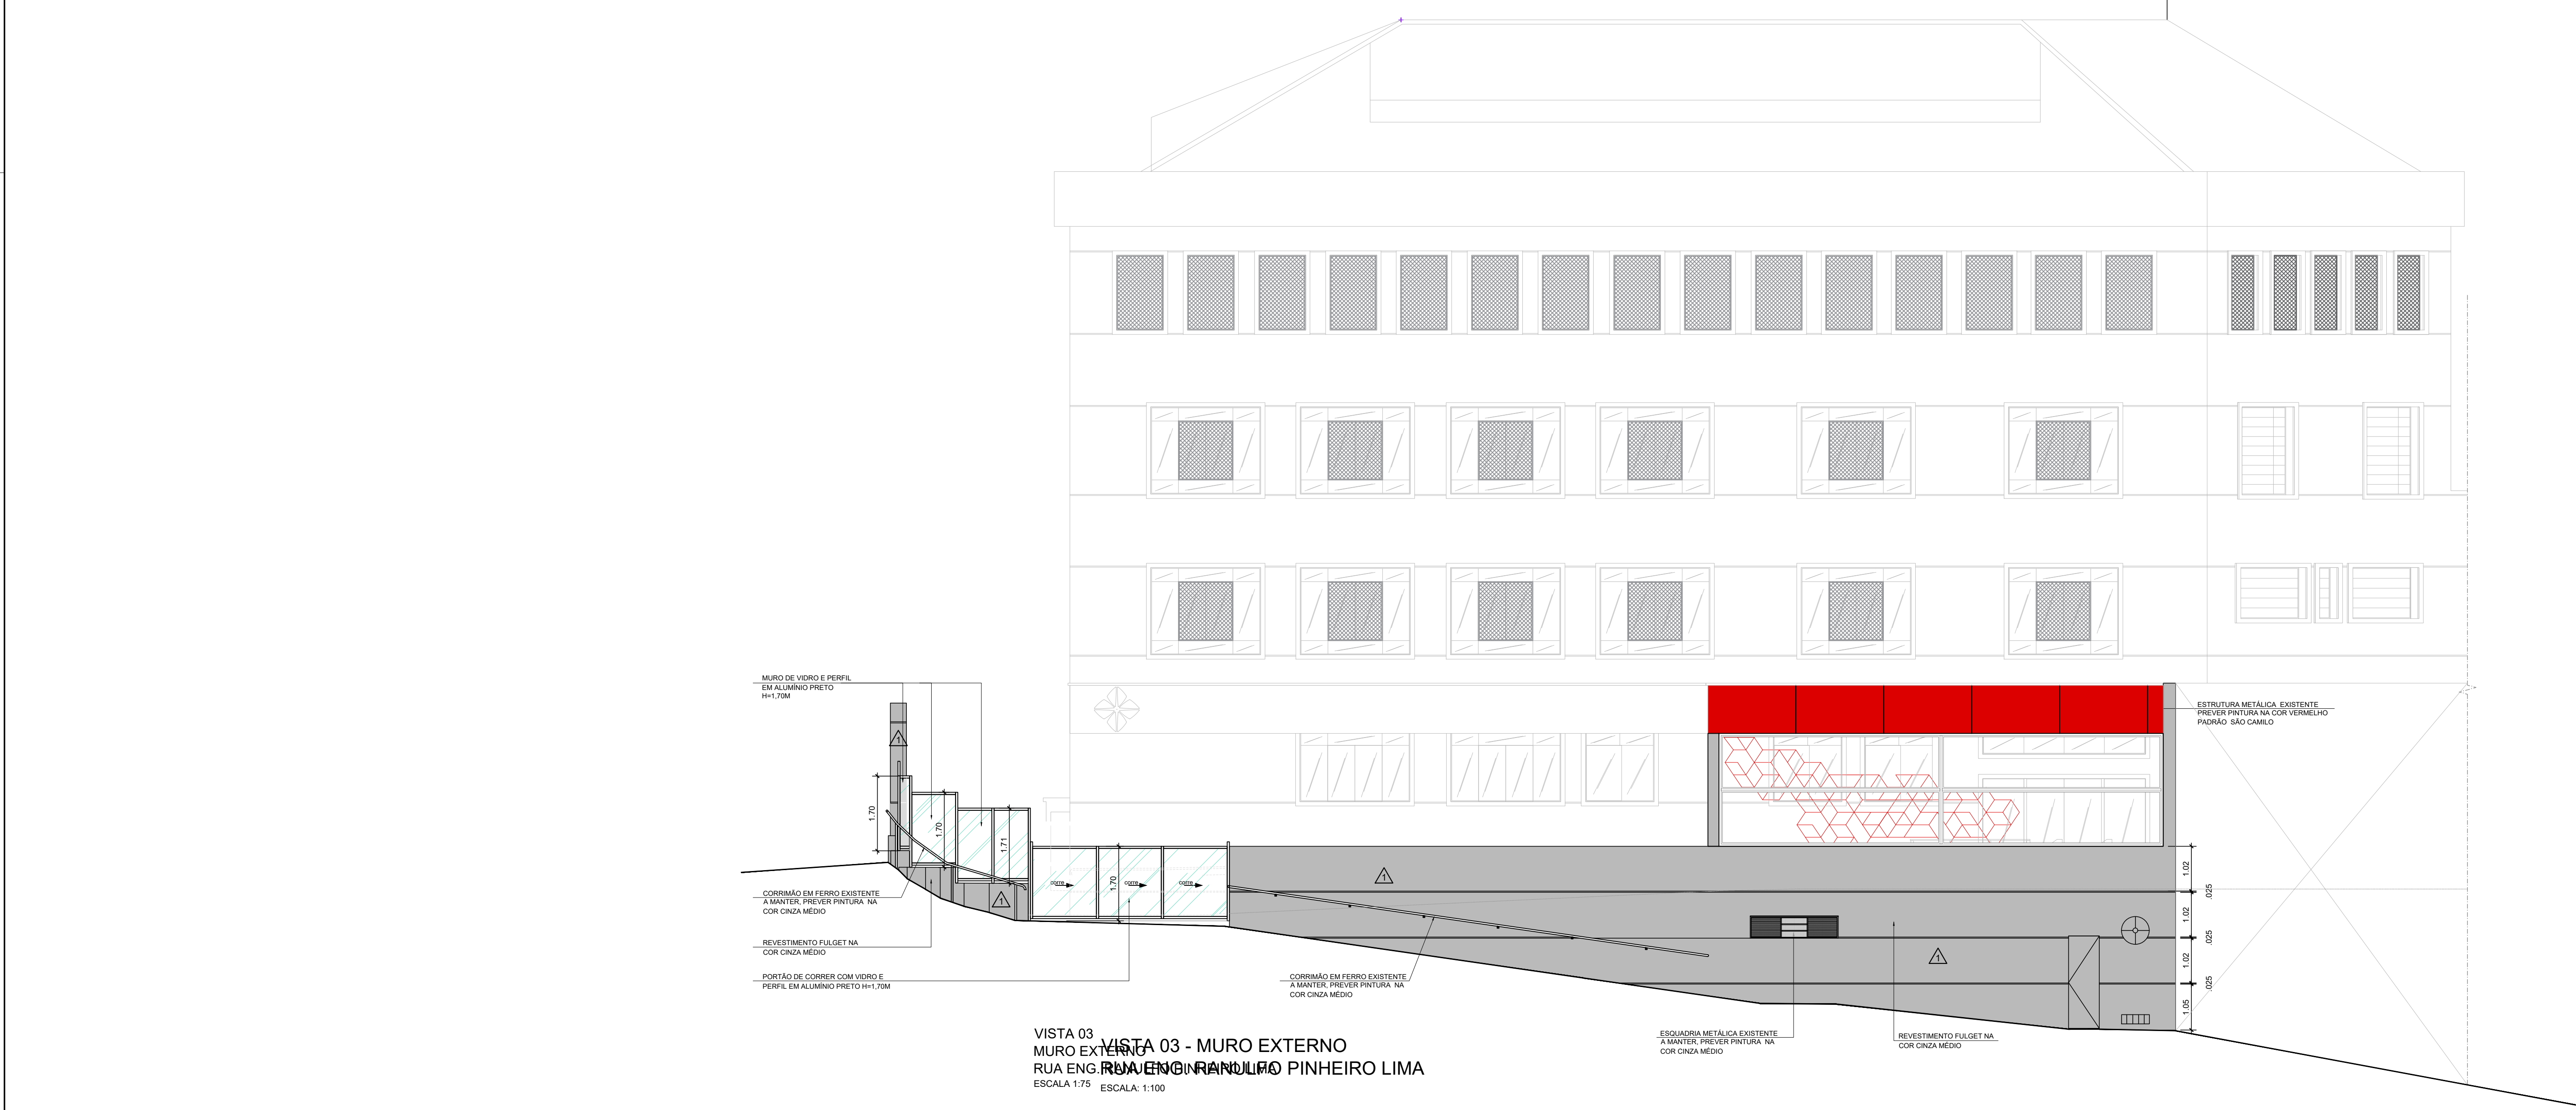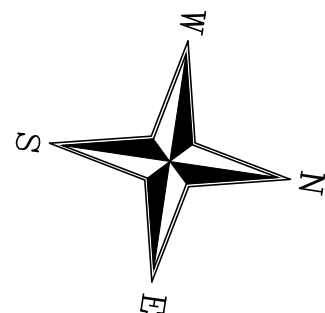

VISTA 03 - MURO EXTERNO
RUA ENG. RANDOLFO PINHEIRO LIMA
ESCALA: 1:100

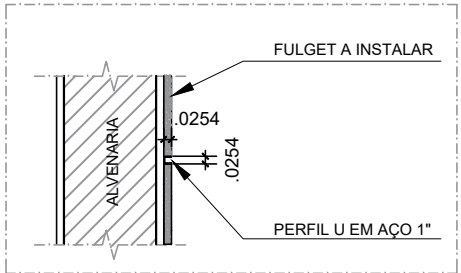

DET. 02
ESCALA: 1:25

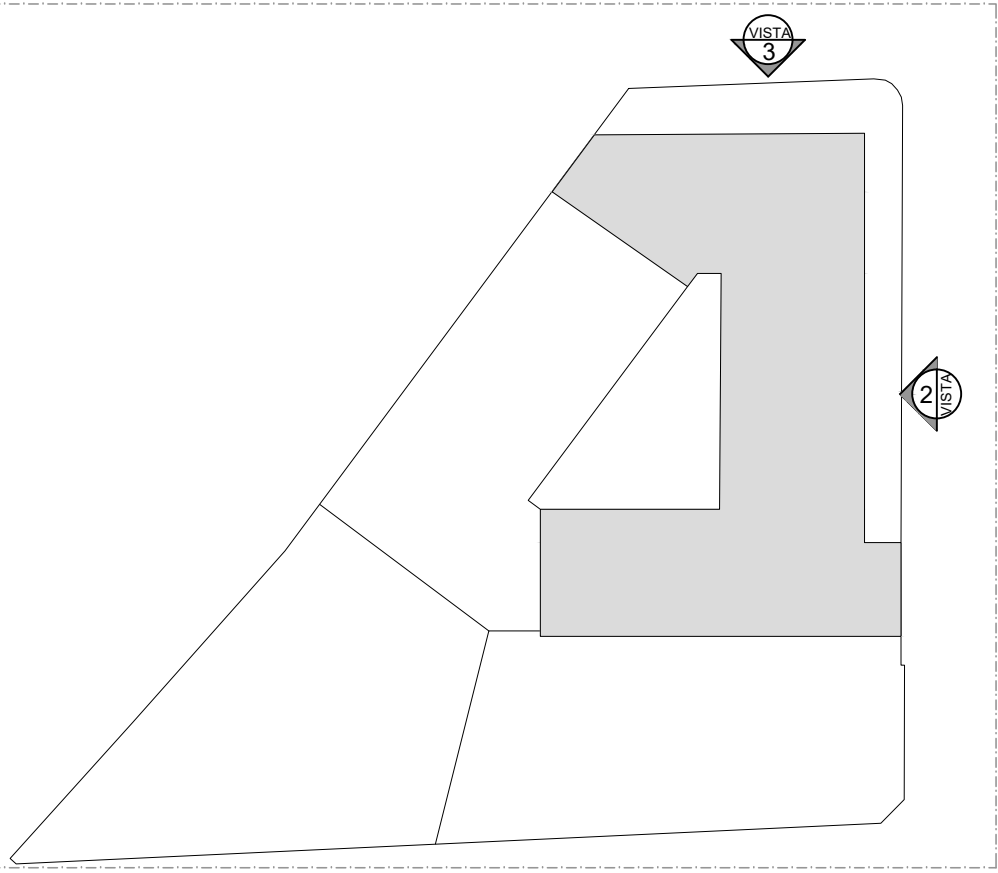

LEGENDA DE ACABAMENTOS	
PAREDES EXTERNAS	
1	REVESTIMENTO FULGET NA COR CINZA MEDIO COM JUNTAS DE DILATAÇÃO HORIZONTAIS DE 1" (2,54CM)
2	REVESTIMENTO FULGET NA COR CINZA CLARO COM JUNTAS DE DILATAÇÃO HORIZONTAIS DE 1" (2,54CM)
3	REVESTIMENTO FULGET NA COR VERMELHO
4	ESTRUTURA METÁLICA FINADA NA FACHADA REVESTIDA COM PAINEL DE ACM NA COR VERMELHO PADRÃO SÃO CAMILO (VER PROJETO ESPECÍFICO)
5	ESTRUTURA METÁLICA FINADA NA FACHADA REVESTIDA COM PAINEL DE ACM NA COR CINZA MEDIO (VER PROJETO ESPECÍFICO)
6	REDE DE FERRILHOS REVESTIDA EM FOLHA DE ALUMINIO INÓXIDIZANTE (VER PROJETO ESPECÍFICO)
7	REDE DE FERRILHOS REVESTIDA EM FOLHA DE ALUMINIO INÓXIDIZANTE (VER PROJETO ESPECÍFICO)
8	CERÂMICA 10X10 EXISTENTE A MANTER
9	MARQUISE EXISTENTE REVESTIDA EM CHAPA METÁLICA, PREVER NOVA PINTURA NA COR VERMELHO PADRÃO SÃO CAMILO
10	RECOMBINAÇÃO EM BARRA COM PINTURA NA COR CINZA MEDIO

PROJETO: UNIVERSIDADE SÃO CAMILO - UNIDADE IPIRANGA PROMOVE		REVISÃO: 01
ASSUNTO: REFORMA DE FACHADA / ESTUDO PRELIMINAR		FOLHA: 07/07
PROJ: FACHADAS 02 / 03 - MUROS EXTERNOS		ESC: 1: 75
RESPONSÁVEL TÉCNICO: MAURO PEREIRA FILHO		DATA: 04.05.23
CAU DO RESPONSÁVEL TÉCNICO: A - 7458-6		RRT
PROJETISTA:		CLIENTE:
02 05.08.25 REVISÃO MURO FRONTAL CONFORME APONTAMENTOS DO SÃO CAMILO		
01 07.11.24 REVISÃO GERAL CONFORME APONTAMENTOS		
REVISÃO: DATA: DESCRIÇÃO:		