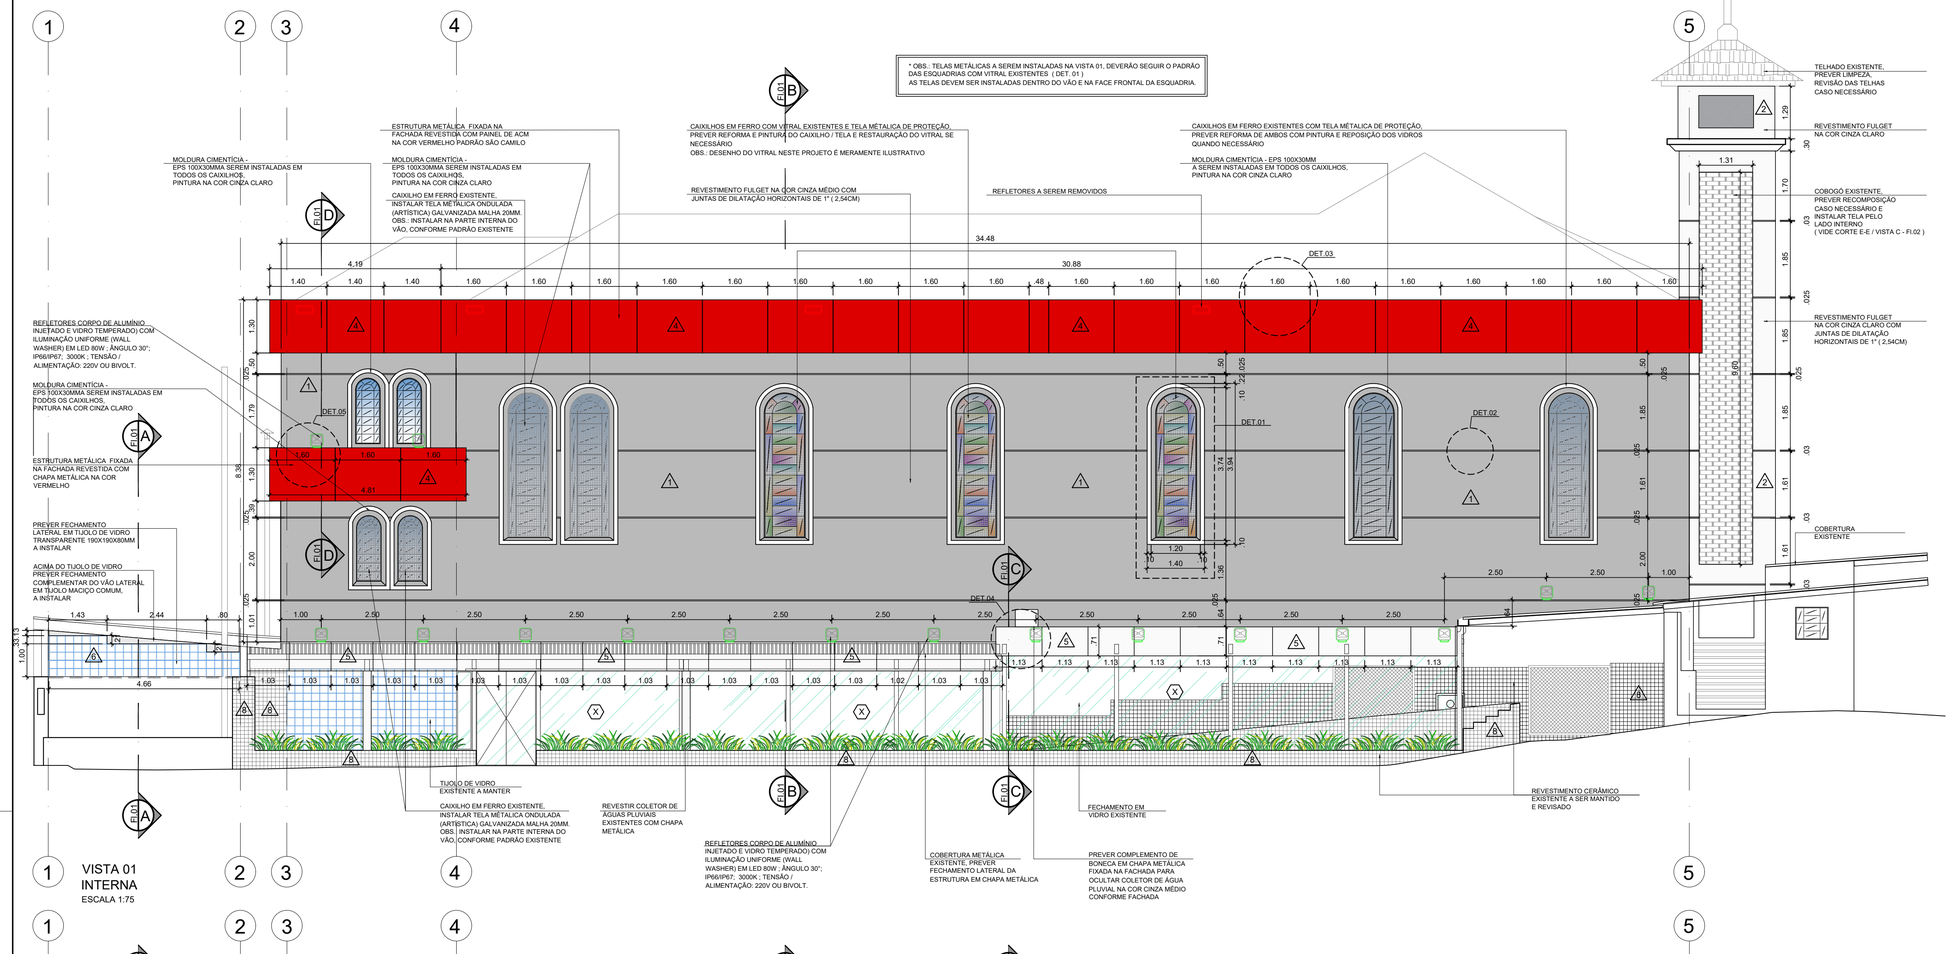


IMPORTANTE:
** NOTA TÉCNICA - PROJETO DE FACHADA,INSTALAÇÃO DE ACM **
A INSTALAÇÃO DE ACM NA FACHADA DO EDIFÍCIO REQUER A ELABORAÇÃO DE UM PROJETO ESPECÍFICO, QUE CONTEMPLE TODOS OS DETALHES TÉCNICOS E ESTRUTURAIS NECESSÁRIOS PARA GARANTIR A EXECUÇÃO SEGURA, EFICIENTE E ESTETICAMENTE SATISFATÓRIA DO MATERIAL. O PROJETO DEVERÁ ESPECIFICAR AS CONDIÇÕES DE FIXAÇÃO, INCLUINDO SUPORTES, ANCORAGENS E DETALHES DE ACABAMENTO, RESPEITANDO AS NORMAS DE SEGURANÇA E DESEMPENHO.

LEGENDA DE ACABAMENTOS

	PAREDES EXTERNAS
1	REVESTIMENTO FULGET NA COR CINZA MÉDIO COM JUNTAS DE DILATAÇÃO HORIZONTAIS DE 1" (2,54CM)
2	REVESTIMENTO FULGET NA COR CINZA CLARO COM JUNTAS DE DILATAÇÃO HORIZONTAIS DE 1" (2,54CM)
3	REVESTIMENTO FULGET NA COR VERMELHO
4	ESTRUTURA METÁLICA FIXADA NA FACHADA REVESTIDA COM PAINEL DE ACM NA COR VERMELHO PADRÃO SÃO CAMILO (VIDE PROJETO ESPECÍFICO)
5	ESTRUTURA METÁLICA FIXADA NA FACHADA REVESTIDA COM PAINEL DE ACM NA CINZA MÉDIO (VIDE PROJETO ESPECÍFICO)
6	TIJOLO DE VIDRO 190X190X80MM ONDULADO INCOLOR, E BARRAS DE AÇO DE 5MM DE DIÂMETRO PARA TRAVAMENTO VERTICAL E HORIZONTAL, A INSTALAR
7	TIJOLO DE VIDRO 200X200X60MM COM VENTILAÇÃO, INCOLOR E BARRAS DE AÇO DE 5MM DE DIÂMETRO PARA TRAVAMENTO VERTICAL E HORIZONTAL, A INSTALAR
8	CERÂMICA 100X100 EXISTENTE,A MANTER
9	MARQUISE EXISTENTE REVESTIDA EM CHAPA METÁLICA, PREVER NOVA PINTURA NA COR VERMELHO PADRÃO SÃO CAMILO
10	RECOMPOSIÇÃO EM MASSA COM PINTURA NA COR CINZA MÉDIO

REVISÃO:	DATA:	DESCRIÇÃO:
02	27.07.26	MUDANÇA NOS FORMATOS CONF. SOLICITAÇÃO DA ENGª DO SÃO CAMILO
01	07.11.24	REVISÃO GERAL CONFORME APONTAMENTOS

PROJETISTA: MP ARQUITETURA – ARQUITETURA & CONSULTORIA
CLIENTE: CENTRO UNIVERSITÁRIO SÃO CAMILO

PROJETO: UNIVERSIDADE SÃO CAMILO - UNIDADE IPIRANGA PROMOVE
REVISÃO: 02
ASSUNTO: REFORMA DE FACHADA / EXECUTIVO
PISO: FACHADA 01- PLANTAS PARCIAIS
ESC.: INDICADA
RESPONSÁVEL TÉCNICO: MAURO PEREIRA FILHO
DATA: 04.05.23
CAU DO RESPONSÁVEL TÉCNICO: A - 7458-6
RRT
FOLHA: 01/12

USC_I_200_EXE_R02_FACHADA_A2_22.07.26.dwg