
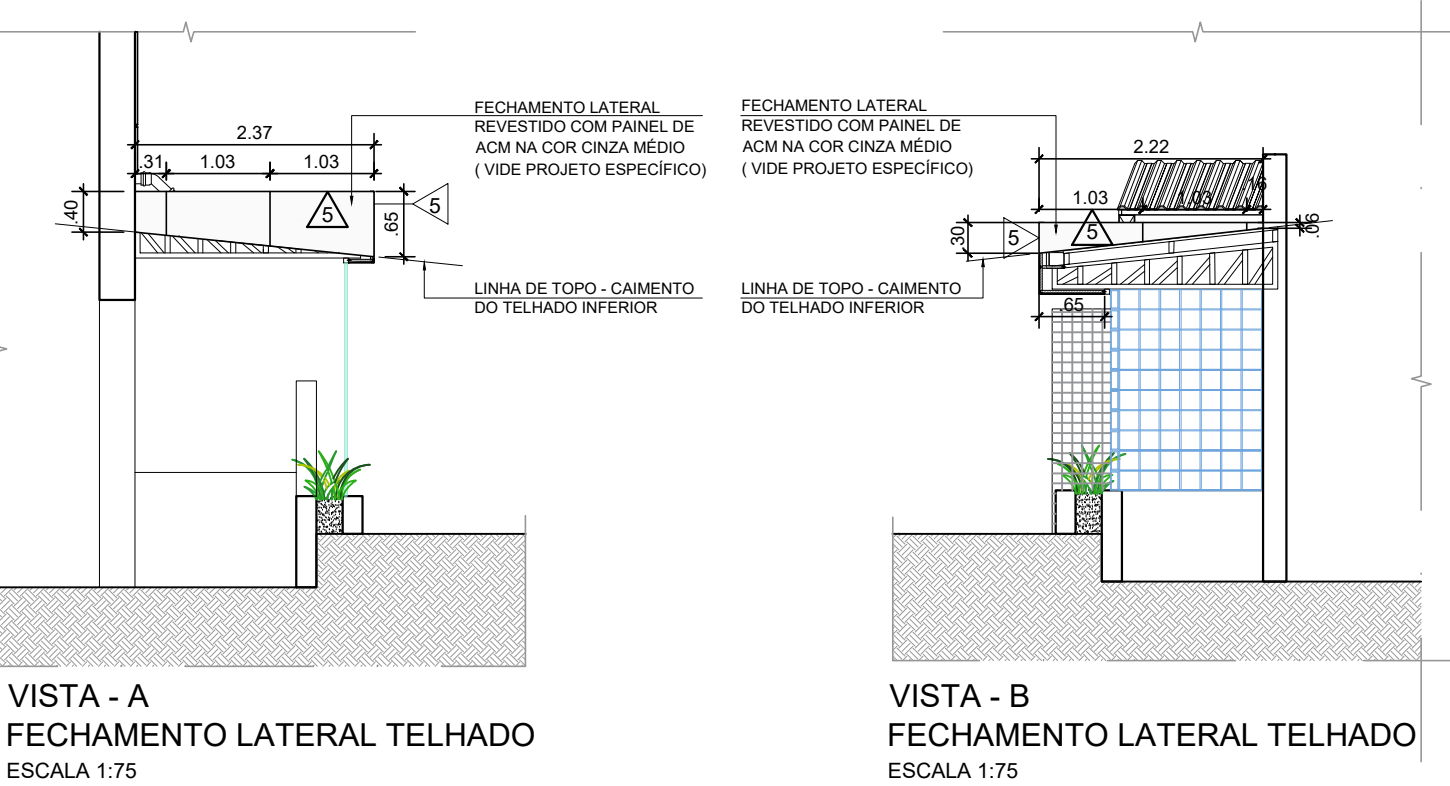


IMPORTANTE:
 ** NOTA TÉCNICA - PROJETO DE FACHADA, INSTALAÇÃO DE ACM **
 A INSTALAÇÃO DE ACM NA FACHADA DO EDIFÍCIO REQUER A ELABORAÇÃO DE UM PROJETO ESPECÍFICO, QUE CONTEMPLE TODOS OS DETALHES TÉCNICOS E ESTRUTURAIS NECESSÁRIOS PARA GARANTIR A EXECUÇÃO SEGURA, EFICIENTE E ESTETICAMENTE SATISFATÓRIA DO MATERIAL. O PROJETO DEVERÁ ESPECIFICAR AS CONDIÇÕES DE FIXAÇÃO, INCLUINDO SUPORTES, ANCORAGENS E DETALHES DE ACABAMENTO, RESPEITANDO AS NORMAS DE SEGURANÇA E DESEMPENHO.


LEGENDA DE ACABAMENTOS

△ PAREDES EXTERNAS	
1	REVESTIMENTO FULGET NA COR CINZA MÉDIO COM JUNTAS DE DILATAÇÃO HORIZONTAIS DE 1" (2,54CM)
2	REVESTIMENTO FULGET NA COR CINZA CLARO COM JUNTAS DE DILATAÇÃO HORIZONTAIS DE 1" (2,54CM)
3	REVESTIMENTO FULGET NA COR VERMELHO
4	ESTRUTURA METÁLICA - FIXADA NA FACHADA REVESTIDA COM PAINEL DE ACM NA COR VERMELHO PADRÃO SÃO CAMILO (VIDE PROJETO ESPECÍFICO)
5	ESTRUTURA METÁLICA - FIXADA NA FACHADA REVESTIDA COM PAINEL DE ACM NA CINZA MÉDIO (VIDE PROJETO ESPECÍFICO)
6	TUJOLO DE VIDRO 190X190X80MM ONDULADO INCOLOR, E BARRAS DE AÇO DE 5MM DE DIÂMETRO PARA TRAVAMENTO VERTICAL E HORIZONTAL.A INSTALAR
7	TUJOLO DE VIDRO 200X200X80MM COM VENTILAÇÃO, INCOLOR E BARRAS DE AÇO DE 5MM DE DIÂMETRO PARA TRAVAMENTO VERTICAL E HORIZONTAL.A INSTALAR
8	CERÂMICA 100X100 EXISTENTE.A MANTER
9	MARQUISE EXISTENTE REVESTIDA EM CHAPA METÁLICA, PREVER NOVA PINTURA NA COR VERMELHO PADRÃO SÃO CAMILO
10	RECOMPOSIÇÃO EM MASSA COM PINTURA NA COR CINZA MÉDIO

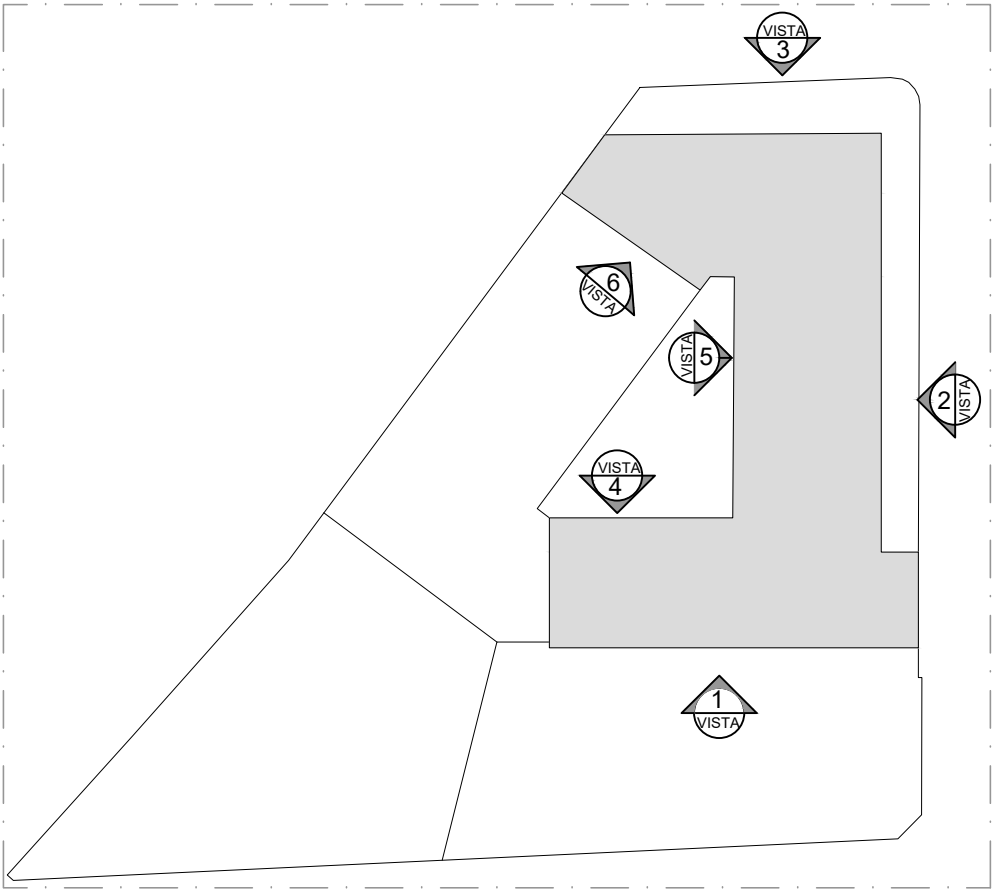


VISTA - A
 FECHAMENTO LATERAL TELHADO
 ESCALA 1:75


VISTA - B
 FECHAMENTO LATERAL TELHADO
 ESCALA 1:75

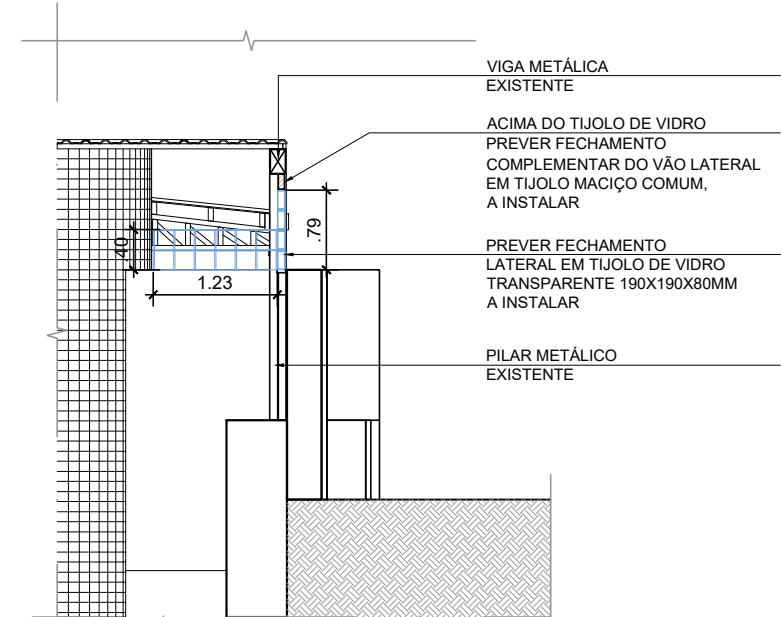


CORTE A-A
 ESCALA 1:75

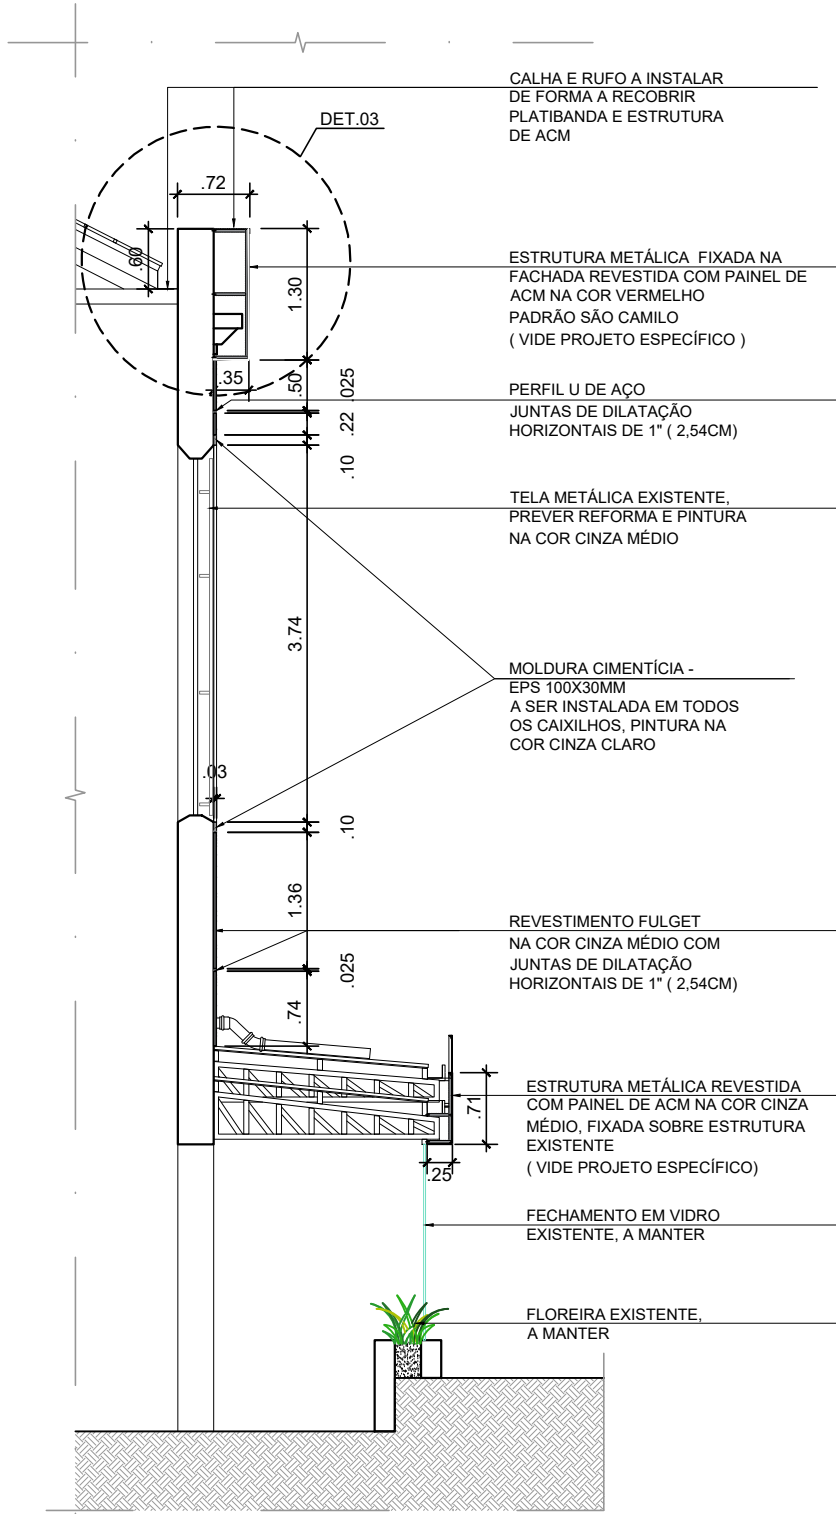


CORTE B-B
 ESCALA 1:75

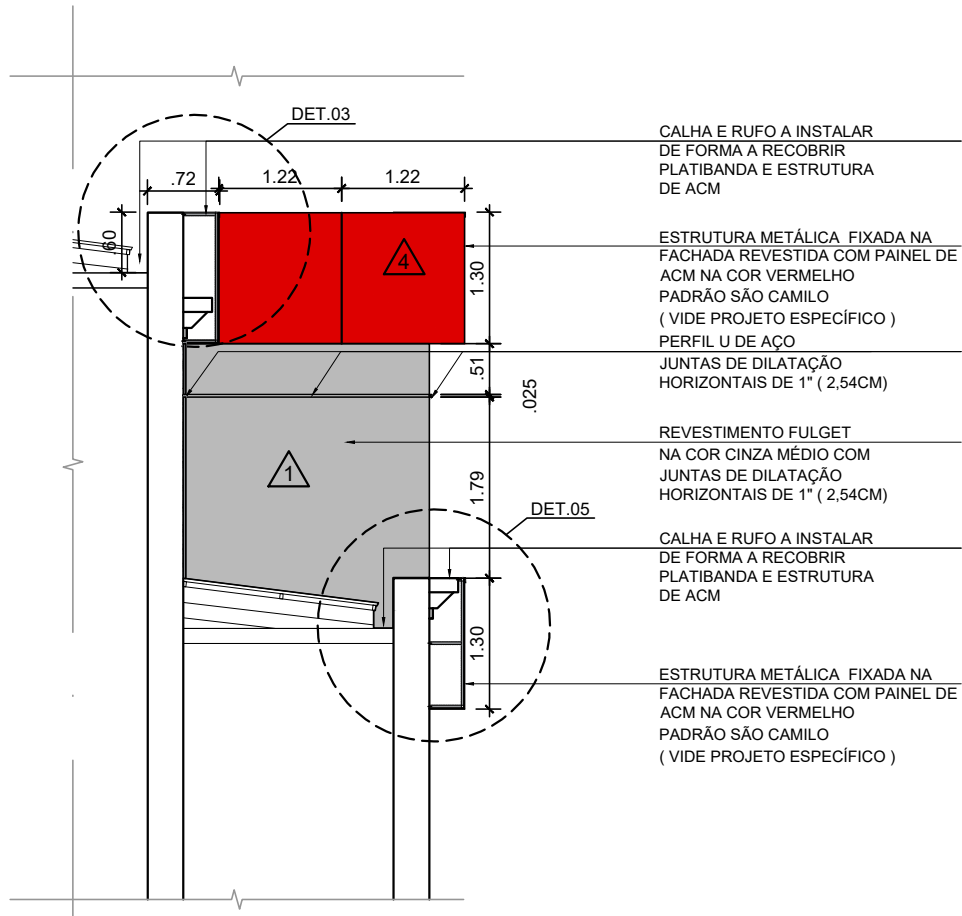

CORTE D-D
 ESCALA 1:75

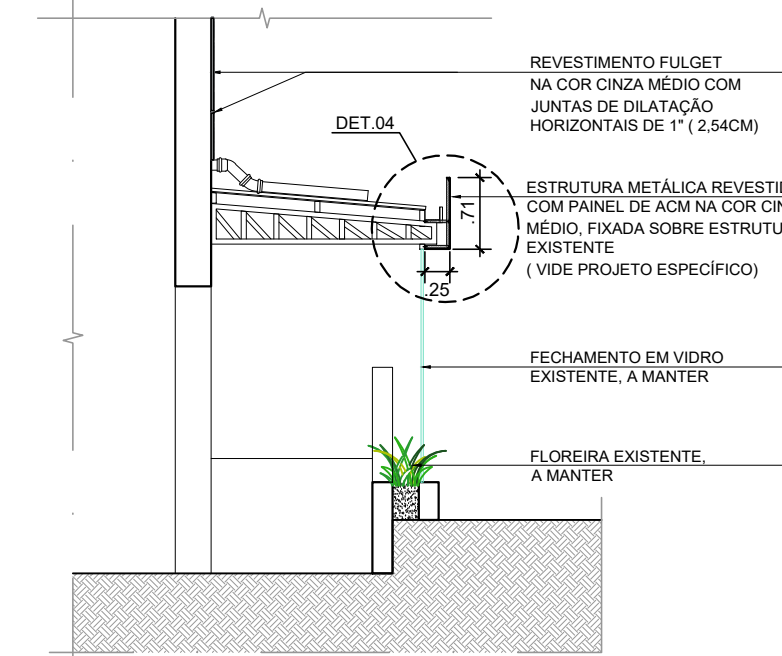

CORTE C-C
 ESCALA 1:75

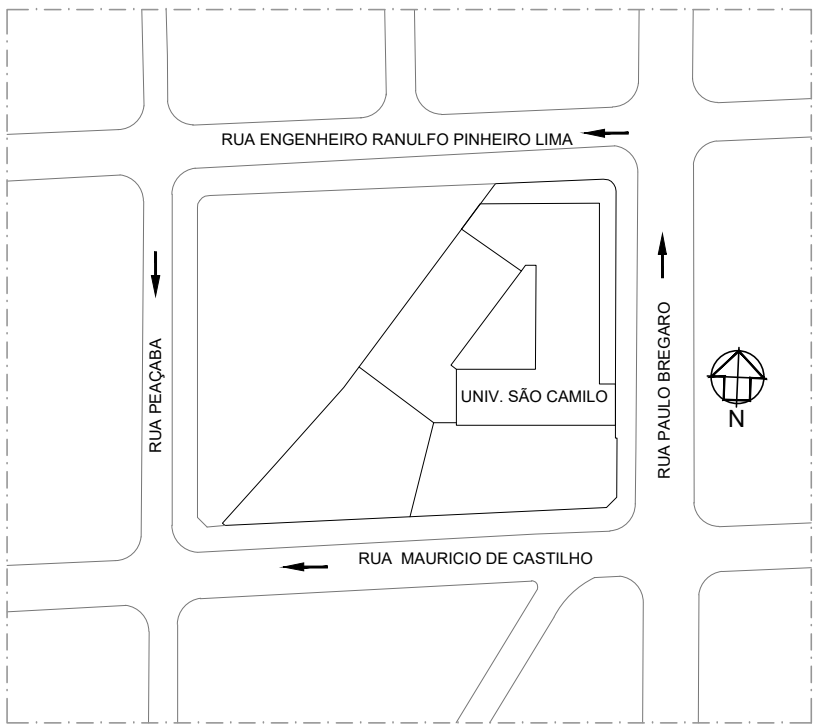

02	27.07.26	MUDANÇA NOS FORMATOS CONF. SOLICITAÇÃO DA ENGª DO SÃO CAMILO
01	07.11.24	REVISÃO GERAL CONFORME APONTAMENTOS
REVISÃO:	DATA:	DESCRIÇÃO:
PROJETISTA:  MP ARQUITETURA ARQUITETURA & CONSULTORIA		CLIENTE:  CENTRO UNIVERSITÁRIO SÃO CAMILO
PROJETO: UNIVERSIDADE SÃO CAMILO - UNIDADE IPIRANGA PROMOVE		REVISÃO:
ASSUNTO: REFORMA DE FACHADA / EXECUTIVO		02
PISO/ FACHADA 01- CORTES	ESC.: INDICADA	FOLHA: 02 / 12
RESPONSÁVEL TÉCNICO: MAURO PEREIRA FILHO	DATA: 04.05.23	
CAU DO RESPONSÁVEL TÉCNICO A - 7458-6	RRT	